


Tekla structures

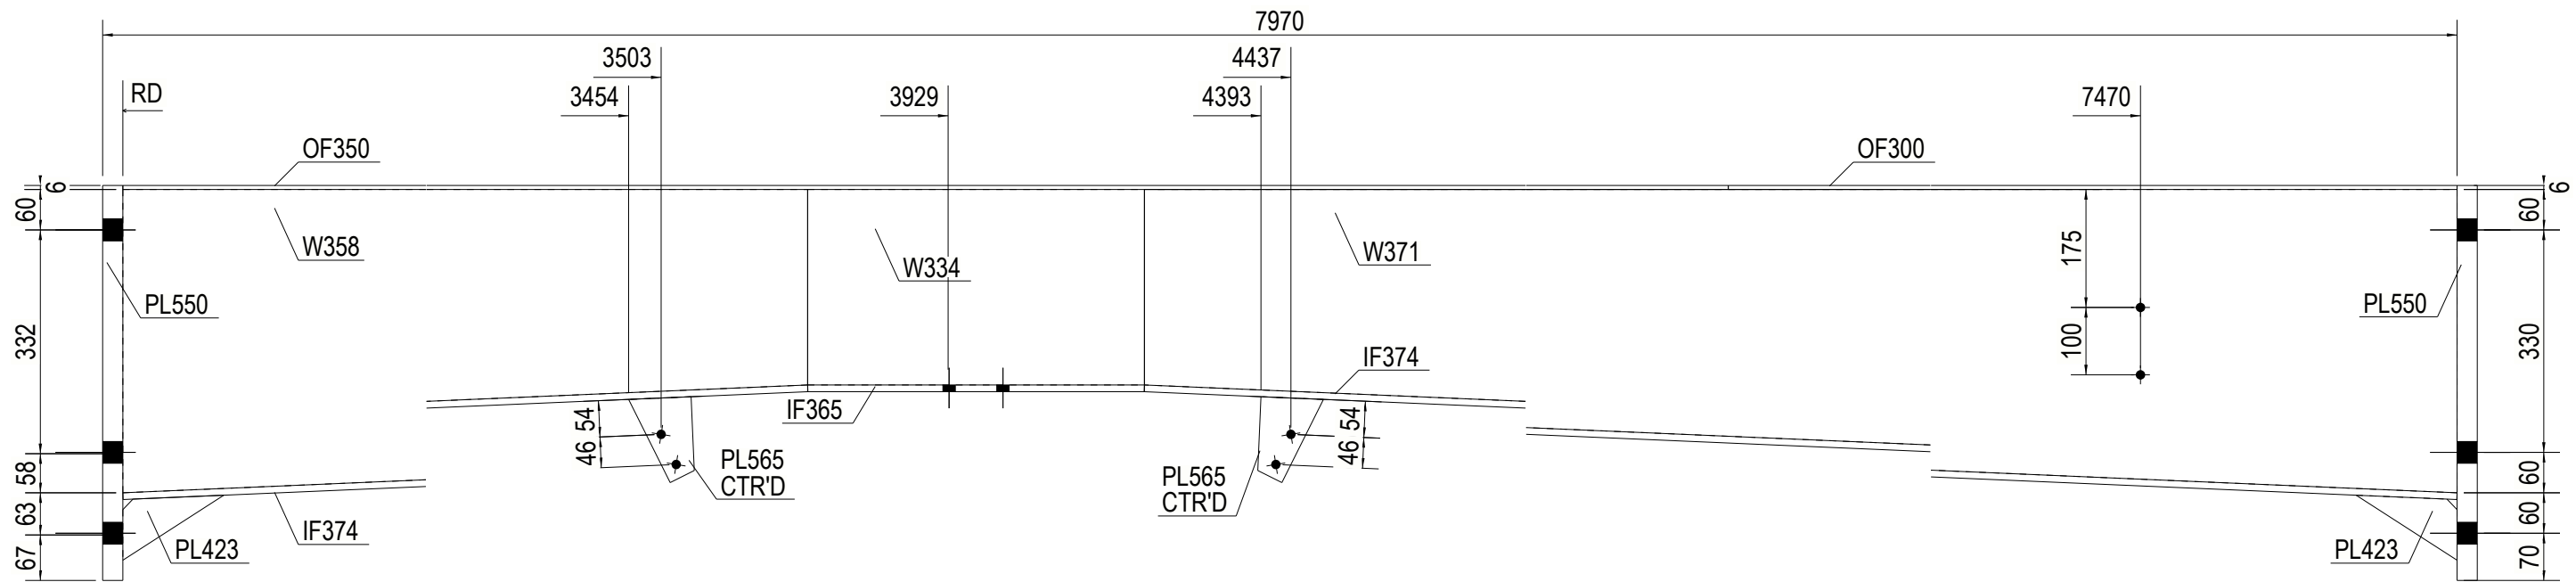

ASSEMBLY MARK	ITEM NO.	DESCRIPTION	LENGTH	MATERIAL	QTY.	UNIT WT. IN Kgs	WT./ITEM IN Kgs	TOTAL WT. IN Kgs	GRAND TOTAL WT.	ITEM TYPE
	IF365	PL 10*200	500	S355JR	1	7.85	7.85	7.85		
	IF374	PL 10*200	3723	S355JR	2	7.85	58.46	116.92		
	OF300	PL 6*200	1950	S355JR	1	7.85	18.37	18.37		
	OF350	PL 6*200	5990	S355JR	1	7.85	56.43	56.43		
	PL423	PLT 12*96.4	150	S355JR	2	7.85	0.62	1.25		
	PL550	PL 30*200	586	S355JR	2	7.85	27.60	55.20		
	PL565	PL 5*84.7	138	S355JR	2	7.85	0.31	0.62		
	W334	PLT 4*290	500	S355JR	1	7.85	4.55	4.55		
	W358	PLT 4*450	3720	S355JR	1	7.85	43.22	43.22		
	W371	PLT 4*450	3720	S355JR	1	7.85	43.22	43.22		
TOTAL IN Kgs.								347.62	347.62	LIGHT_STEEL

BU-19 x 1

QTY= 1 Nos. MEZZ BEAM MKD : BU-19

REV.	DATE	DESCRIPTION	DRW	CHK	APP
ELNAGAR					
DRAWN				DATE	
CHECKED				SCALE	1:10
REVIEWED				REL. NO.	
ASSEMBLY MARK				SHT. NO.	REV. NO.

BU-19