


Tekla structures

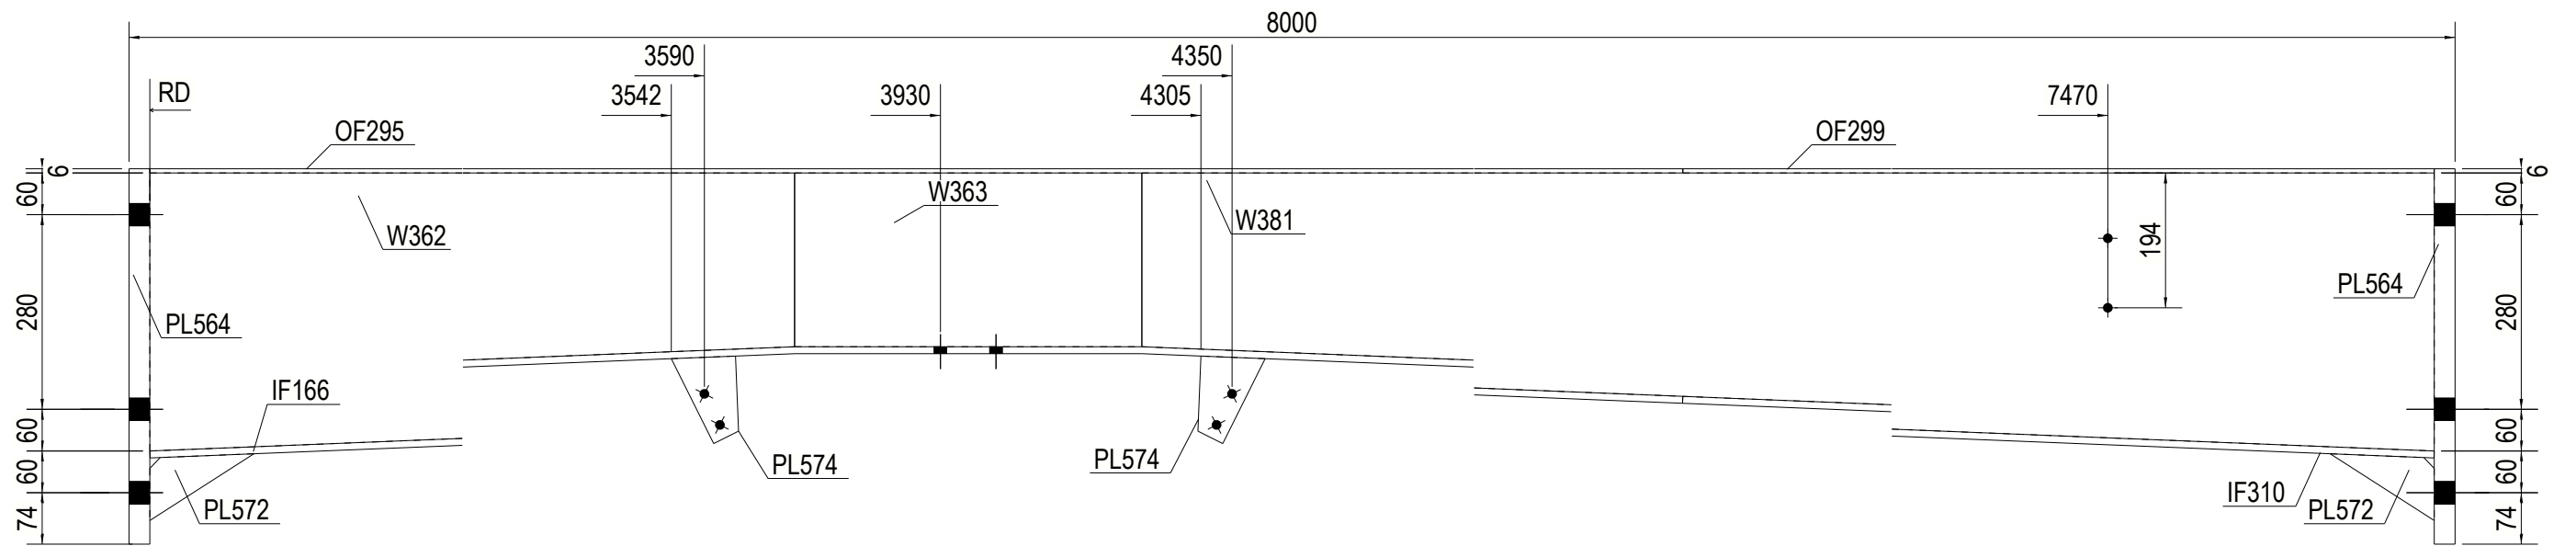

ASSEMBLY MARK	ITEM NO.	DESCRIPTION	LENGTH	MATERIAL	QTY.	UNIT WT. IN Kgs	WT./ITEM IN Kgs	TOTAL WT. IN Kgs	GRAND TOTAL WT.	ITEM TYPE
	IF166	PL 10*200	5994	S355JR	1	7.85	94.11	94.11		
	IF310	PL 10*200	1952	S355JR	1	7.85	30.64	30.64		
	OF295	PL 6*200	5990	S355JR	1	7.85	56.43	56.43		
	OF299	PL 6*200	1950	S355JR	1	7.85	18.37	18.37		
	PL564	PL 30*200	540	S355JR	2	7.85	25.43	50.87		
	PL572	PL 12*96	150	S355JR	2	7.85	0.62	1.25		
	PL574	PL 5*84.4	137	S355JR	2	7.85	0.30	0.61		
	W362	PL 4*400	3720	S355JR	1	7.85	37.96	37.96		
	W363	PL 4*250	500	S355JR	1	7.85	3.93	3.93		
	W381	PL 4*400	3720	S355JR	1	7.85	37.96	37.96		
TOTAL IN Kgs.								332.12	664.23	LIGHT_STEEL

BU-26 x 2

QTY= 2 Nos. MEZZ BEAM MKD : BU-26

REV.	DATE	DESCRIPTION	DRW	CHK	APP
ELNAGAR					
DRAWN			DATE		
CHECKED			SCALE	1:10	
REVIEWED			REL. NO.		
ASSEMBLY MARK	BU-26		SHT. NO.	REV. NO.	