


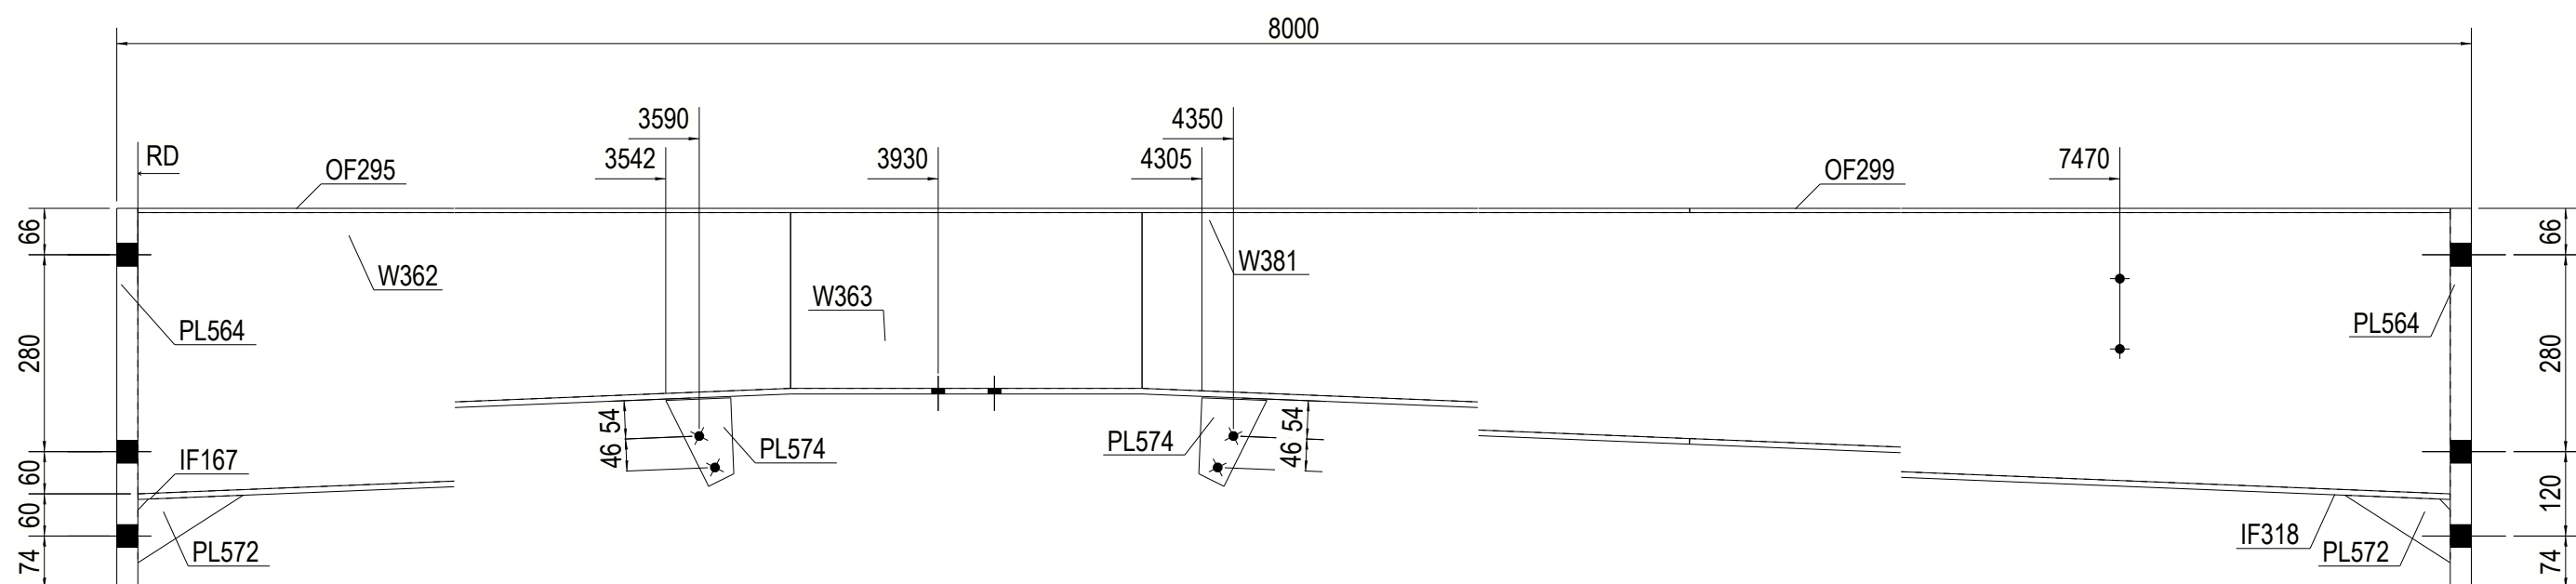

ASSEMBLY MARK	ITEM NO.	DESCRIPTION	LENGTH	MATERIAL	QTY.	UNIT WT. IN Kgs	WT./ITEM IN Kgs	TOTAL WT. IN Kgs	GRAND TOTAL WT.	ITEM TYPE
reka structures	IF167	PL8*200	5994	S355JR	1	7.85	75.29	75.29		
	IF318	PL8*200	1952	S355JR	1	7.85	24.51	24.51		
	OF295	PL6*200	5990	S355JR	1	7.85	56.43	56.43		
	OF299	PL6*200	1950	S355JR	1	7.85	18.37	18.37		
	PL564	PL30*200	540	S355JR	2	7.85	25.43	50.87		
	PL572	PL12*96	150	S355JR	2	7.85	0.62	1.25		
	PL574	PL5*84.4	137	S355JR	2	7.85	0.30	0.61		
	W362	PL4*400	3720	S355JR	1	7.85	37.96	37.96		
	W363	PL4*250	500	S355JR	1	7.85	3.93	3.93		
	W381	PL4*400	3720	S355JR	1	7.85	37.96	37.96		
BU-27 x 1						TOTAL IN Kgs.		307.17	307.17	LIGHT_STEEL

QTY= 1 Nos. MEZZ BEAM MKD : BU-27

REV.	DATE	DESCRIPTION	DRW	CHK	APP
ELNAGAR					
DRAWN			DATE		
CHECKED			SCALE	1:10	
REVIEWED			REL. NO.		
ASSEMBLY MARK			SHT. NO.	REV. NO.	
BU-27					

BU-27