


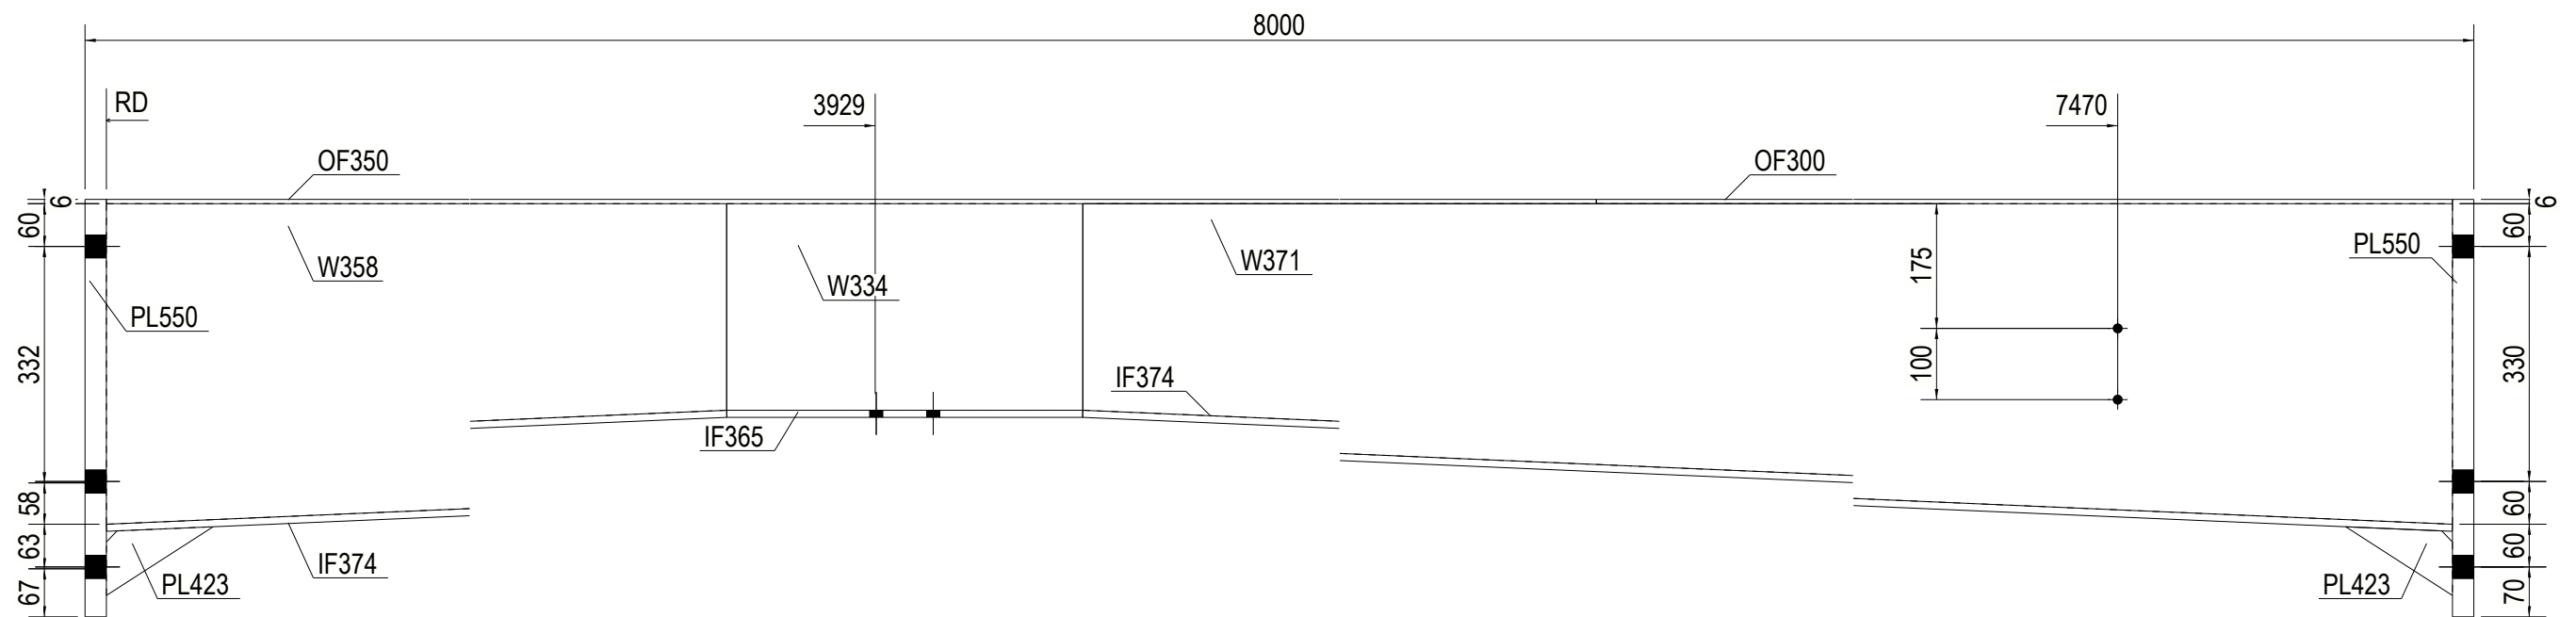

ASSEMBLY MARK	ITEM NO.	DESCRIPTION	LENGTH	MATERIAL	QTY.	UNIT WT. IN Kgs	WT./ITEM IN Kgs	TOTAL WT. IN Kgs	GRAND TOTAL WT.	ITEM TYPE
reka structures	IF365	PL10*200	500	S355JR	1	7.85	7.85	7.85		
	IF374	PL10*200	3723	S355JR	2	7.85	58.46	116.92		
	OF300	PL6*200	1950	S355JR	1	7.85	18.37	18.37		
	OF350	PL6*200	5990	S355JR	1	7.85	56.43	56.43		
	PL423	PLT12*96.4	150	S355JR	2	7.85	0.62	1.25		
	PL550	PL30*200	586	S355JR	2	7.85	27.60	55.20		
	W334	PLT4*290	500	S355JR	1	7.85	4.55	4.55		
	W358	PLT4*450	3720	S355JR	1	7.85	43.22	43.22		
	W371	PLT4*450	3720	S355JR	1	7.85	43.22	43.22		
BU-28 x 4							TOTAL IN Kgs.	347.00	138***	LIGHT_STEEL

REV.	DATE	DESCRIPTION	DRW	CHK	APP
ELNAGAR					
DRAWN			DATE		
CHECKED			SCALE	1:10	
REVIEWED			REL. NO.		
ASSEMBLY MARK				SHT. NO.	REV. NO.
BU-28					