


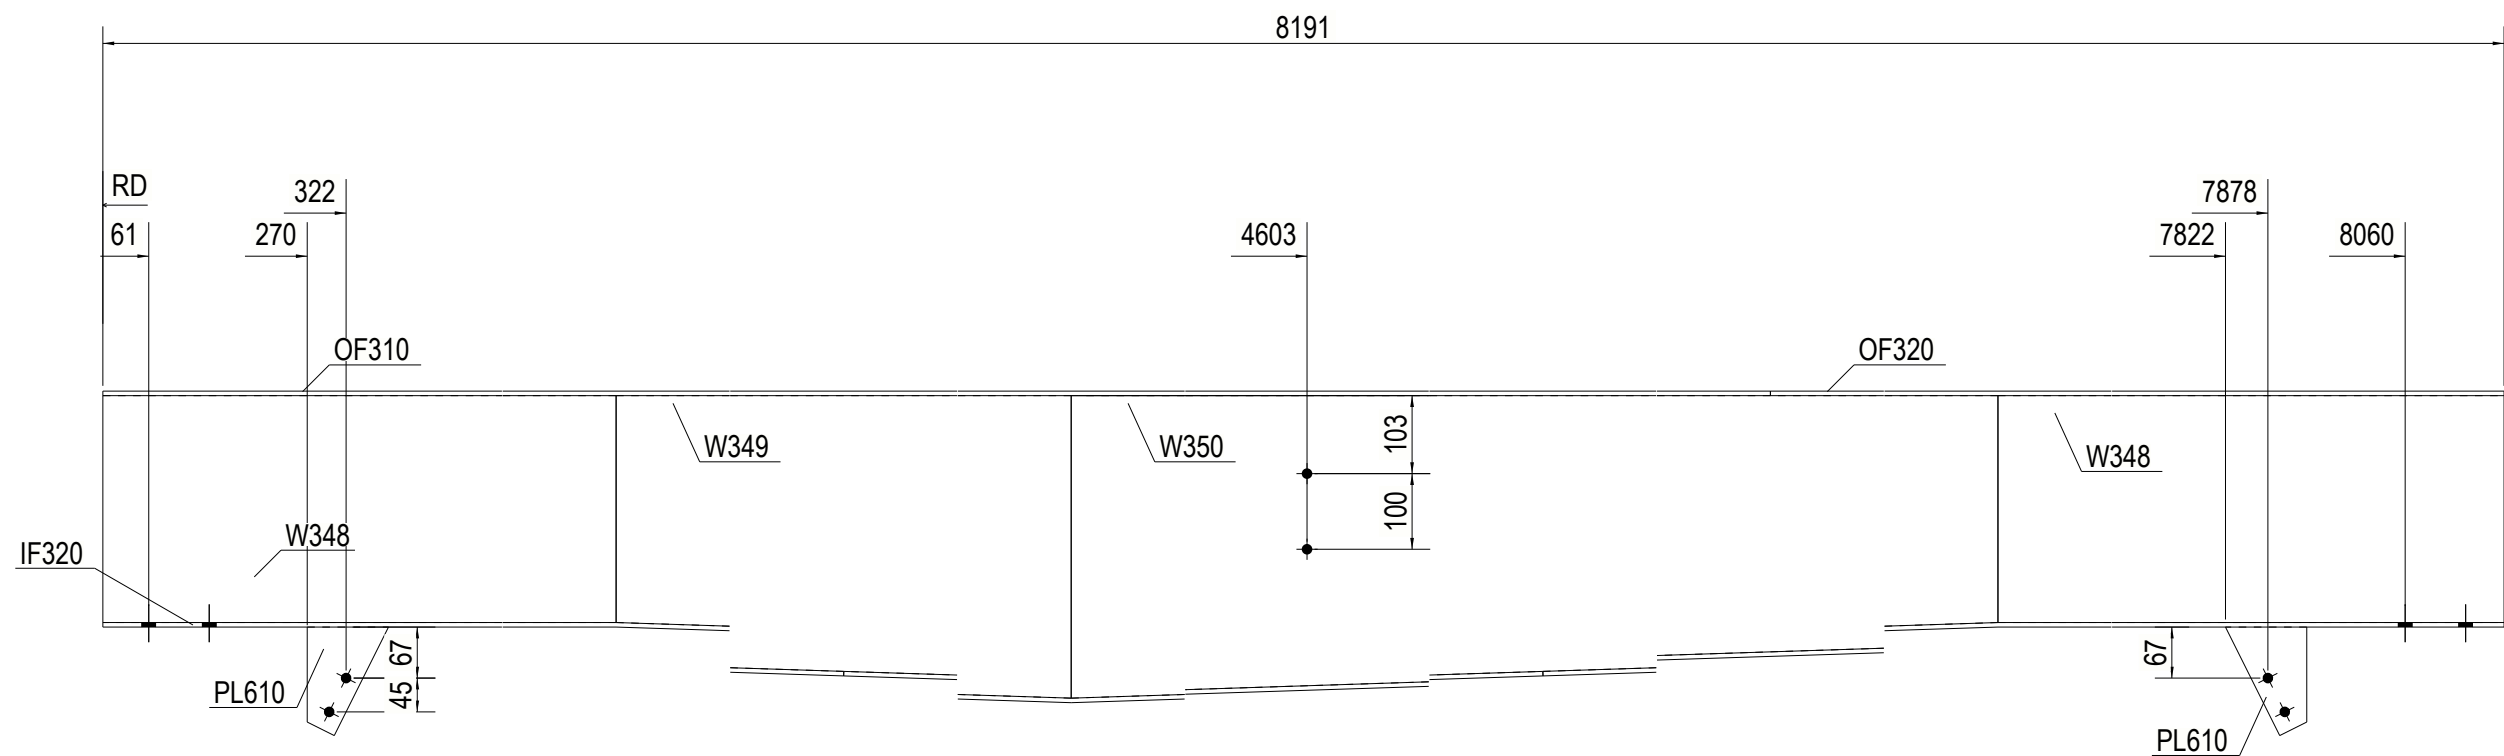

ASSEMBLY MARK	ITEM NO.	DESCRIPTION	LENGTH	MATERIAL	QTY.	UNIT WT. IN Kgs	WT./ITEM IN Kgs	TOTAL WT. IN Kgs	GRAND TOTAL WT.	ITEM TYPE
reka structures	IF319	PL6*125	2192	S355JR	1	7.85	12.91	12.91		
	IF320	PL6*125	3001	S355JR	1	7.85	17.67	17.67		
	IF325	PL6*125	3001	S355JR	1	7.85	17.67	17.67		
	OF310	PL6*125	5990	S355JR	1	7.85	35.27	35.27		
	OF320	PL6*125	2201	S355JR	1	7.85	12.96	12.96		
	PL610	PL5*96.2	160	S355JR	2	7.85	0.39	0.78		
	W348	PL4*300	1000	S355JR	2	7.85	9.42	18.84		
	W349	PL4*400	3095	S355JR	1	7.85	34.02	34.02		
	W350	PL4*400	3095	S355JR	1	7.85	34.02	34.02		
BU-40 x 6							TOTAL IN Kgs.	184.12	110***	LIGHT_STEEL

QTY= 6 Nos. MEZZ BEAM MKD : BU-40

REV.	DATE	DESCRIPTION	DRW	CHK	APP
ELNAGAR					
DRAWN			DATE		
CHECKED			SCALE	1:10	
REVIEWED			REL. NO.		
ASSEMBLY MARK				SHT. NO.	REL. NO.
BU-40					

BU-40