


Tekla structures

ASSEMBLY MARK	ITEM NO.	DESCRIPTION	LENGTH	MATERIAL	QTY.	UNIT WT. IN Kgs	WT./ITEM IN Kgs	TOTAL WT. IN Kgs	GRAND TOTAL WT.	ITEM TYPE
	IF358	PL8*200	1083	S355JR	1	7.85	13.60	13.60		
	IF373	PL8*200	3004	S355JR	1	7.85	37.73	37.73		
	OF349	PL6*200	4083	S355JR	1	7.85	38.46	38.46		
	PL423	PLT12*97.5	150	S355JR	1	7.85	0.62	0.62		
	PL550	PL30*200	586	S355JR	1	7.85	27.60	27.60		
	W352	PLT4*300	1083	S355JR	1	7.85	10.20	10.20		
	W353	PLT4*450	3000	S355JR	1	7.85	35.32	35.32		
TOTAL IN Kgs.								163.53	654.11	LIGHT_STEEL

BU-41 x 4

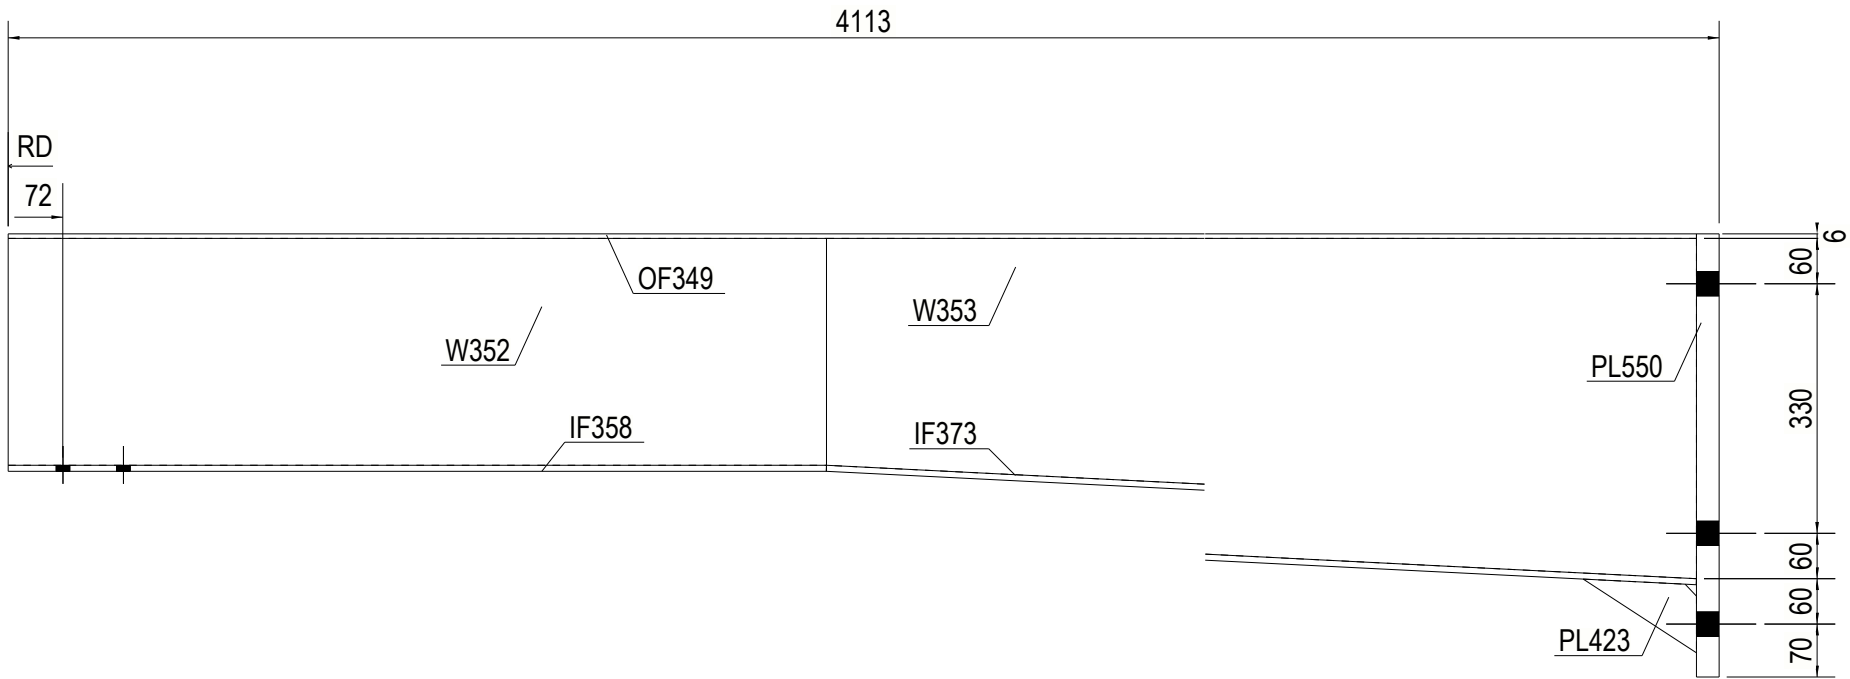

QTY= 4 Nos. MEZZ BEAM MKD : BU-41

REV.	DATE	DESCRIPTION	DRW	CHK	APP
ELNAGAR					
DRAWN			DATE		
CHECKED			SCALE		1:10
REVIEWED			REL. NO.		
ASSEMBLY MARK			SHT. NO.	REV. NO.	
BU-41					