


Tekla structures

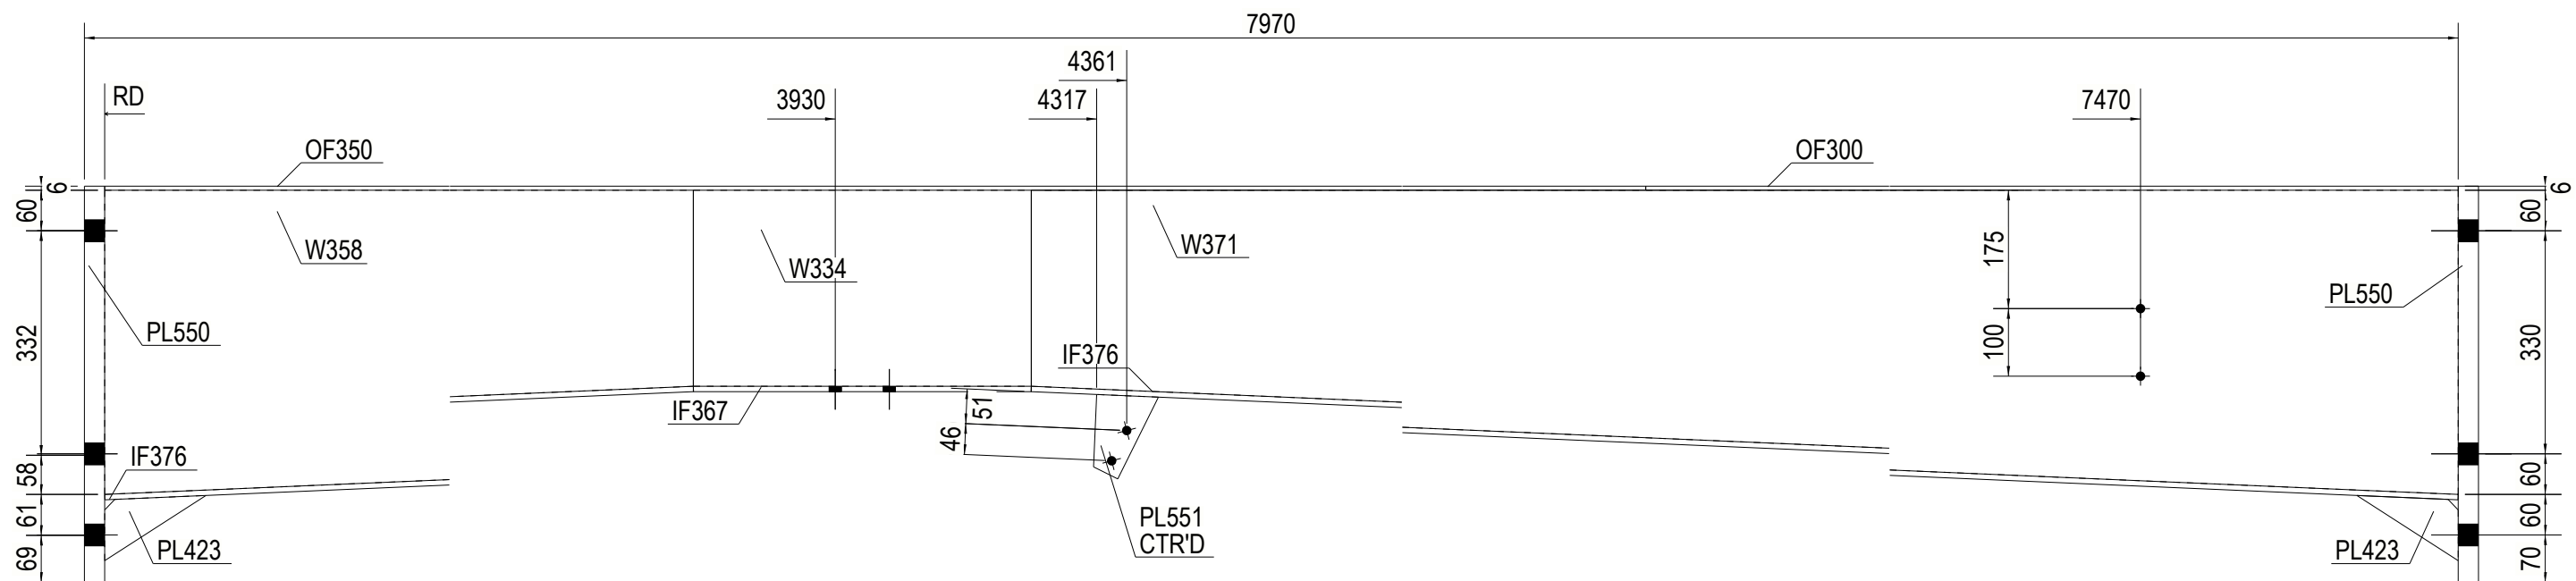

ASSEMBLY MARK	ITEM NO.	DESCRIPTION	LENGTH	MATERIAL	QTY.	UNIT WT. IN Kgs	WT./ITEM IN Kgs	TOTAL WT. IN Kgs	GRAND TOTAL WT.	ITEM TYPE
	IF367	PL8*200	500	S355JR	1	7.85	6.28	6.28		
	IF376	PL8*200	3723	S355JR	2	7.85	46.77	93.53		
	OF300	PL6*200	1950	S355JR	1	7.85	18.37	18.37		
	OF350	PL6*200	5990	S355JR	1	7.85	56.43	56.43		
	PL423	PLT12*96.4	150	S355JR	2	7.85	0.62	1.25		
	PL550	PL30*200	586	S355JR	2	7.85	27.60	55.20		
	PL551	PL5*83.6	135	S355JR	1	7.85	0.30	0.30		
	W334	PLT4*290	500	S355JR	1	7.85	4.55	4.55		
	W358	PLT4*450	3720	S355JR	1	7.85	43.22	43.22		
	W371	PLT4*450	3720	S355JR	1	7.85	43.22	43.22		
TOTAL IN Kgs.								322.35	322.35	LIGHT_STEEL

BU-51 x 1

QTY= 1 Nos. MEZZ BEAM MKD : BU-51

REV.	DATE	DESCRIPTION	DRW	CHK	APP
ELNAGAR					
DRAWN				DATE	
CHECKED				SCALE	1:10
REVIEWED				REL. NO.	
ASSEMBLY MARK				SHT. NO.	REV. NO.

BU-51