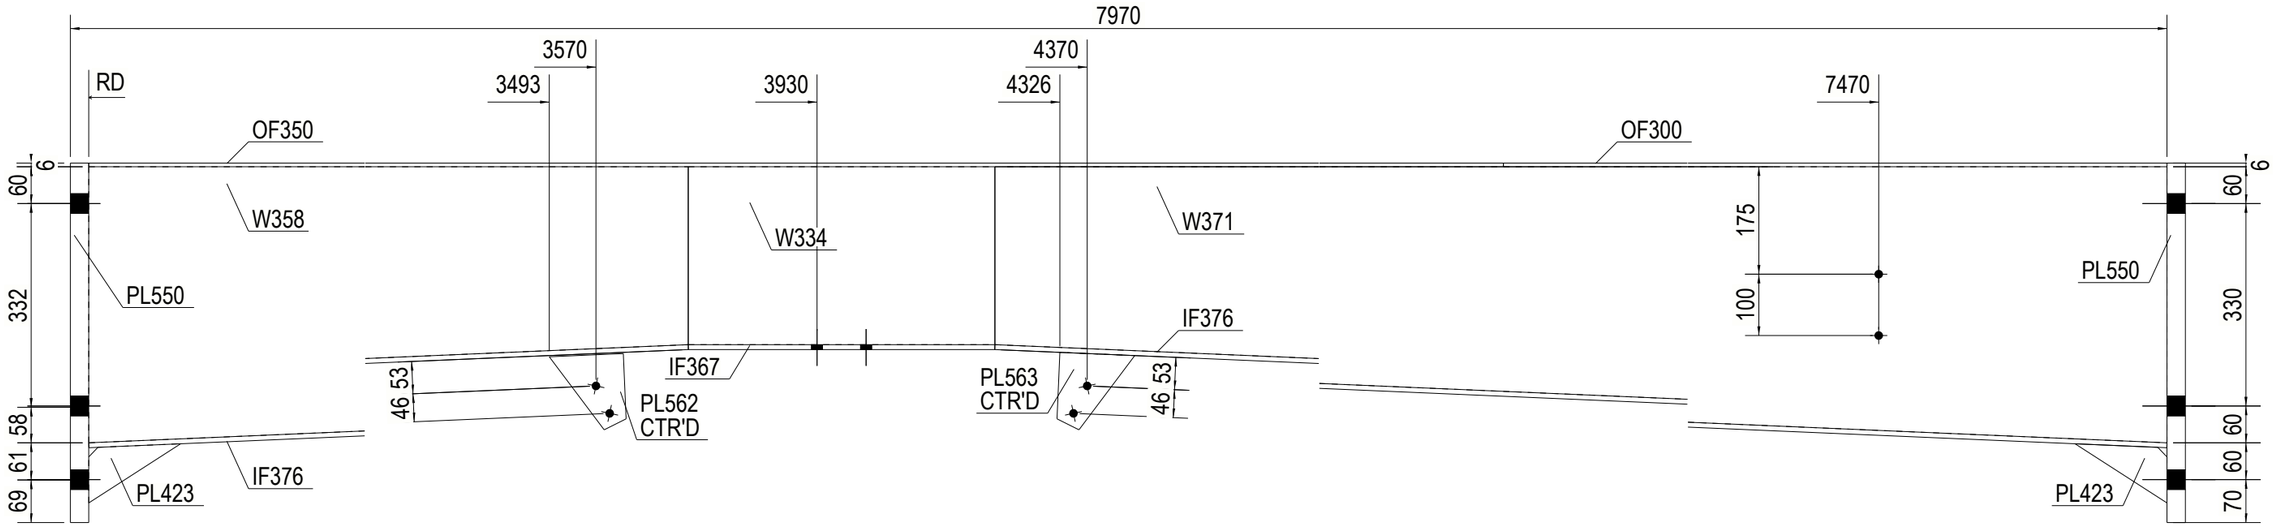

ASSEMBLY MARK	ITEM NO.	DESCRIPTION	LENGTH	MATERIAL	QTY.	UNIT WT. IN Kgs	WT./ITEM IN Kgs	TOTAL WT. IN Kgs	GRAND TOTAL WT.	ITEM TYPE
	IF367	PL8*200	500	S355JR	1	7.85	6.28	6.28		
	IF376	PL8*200	3723	S355JR	2	7.85	46.77	93.53		
	OF300	PL6*200	1950	S355JR	1	7.85	18.37	18.37		
	OF350	PL6*200	5990	S355JR	1	7.85	56.43	56.43		
	PL423	PLT12*96.4	150	S355JR	2	7.85	0.62	1.25		
	PL550	PL30*200	586	S355JR	2	7.85	27.60	55.20		
	PL562	PL5*120.8	123	S355JR	1	7.85	0.37	0.37		
	PL563	PL5*122.2	125	S355JR	1	7.85	0.38	0.38		
	W334	PLT4*290	500	S355JR	1	7.85	4.55	4.55		
	W358	PLT4*450	3720	S355JR	1	7.85	43.22	43.22		
	W371	PLT4*450	3720	S355JR	1	7.85	43.22	43.22		
BU-53 x 2						TOTAL IN Kgs.		322.79	645.59	LIGHT_STEEL

QTY= 2 Nos. MEZZ BEAM MKD : BU-53

REV.	DATE	DESCRIPTION	DRW	CHK	APP

ELNAGAR

DRAWN			DATE	
CHECKED			SCALE	1:10
REVIEWED			REL. NO.	
ASSEMBLY MARK	**BU-53**		SHT. NO.	REV. NO.

Tekla structures