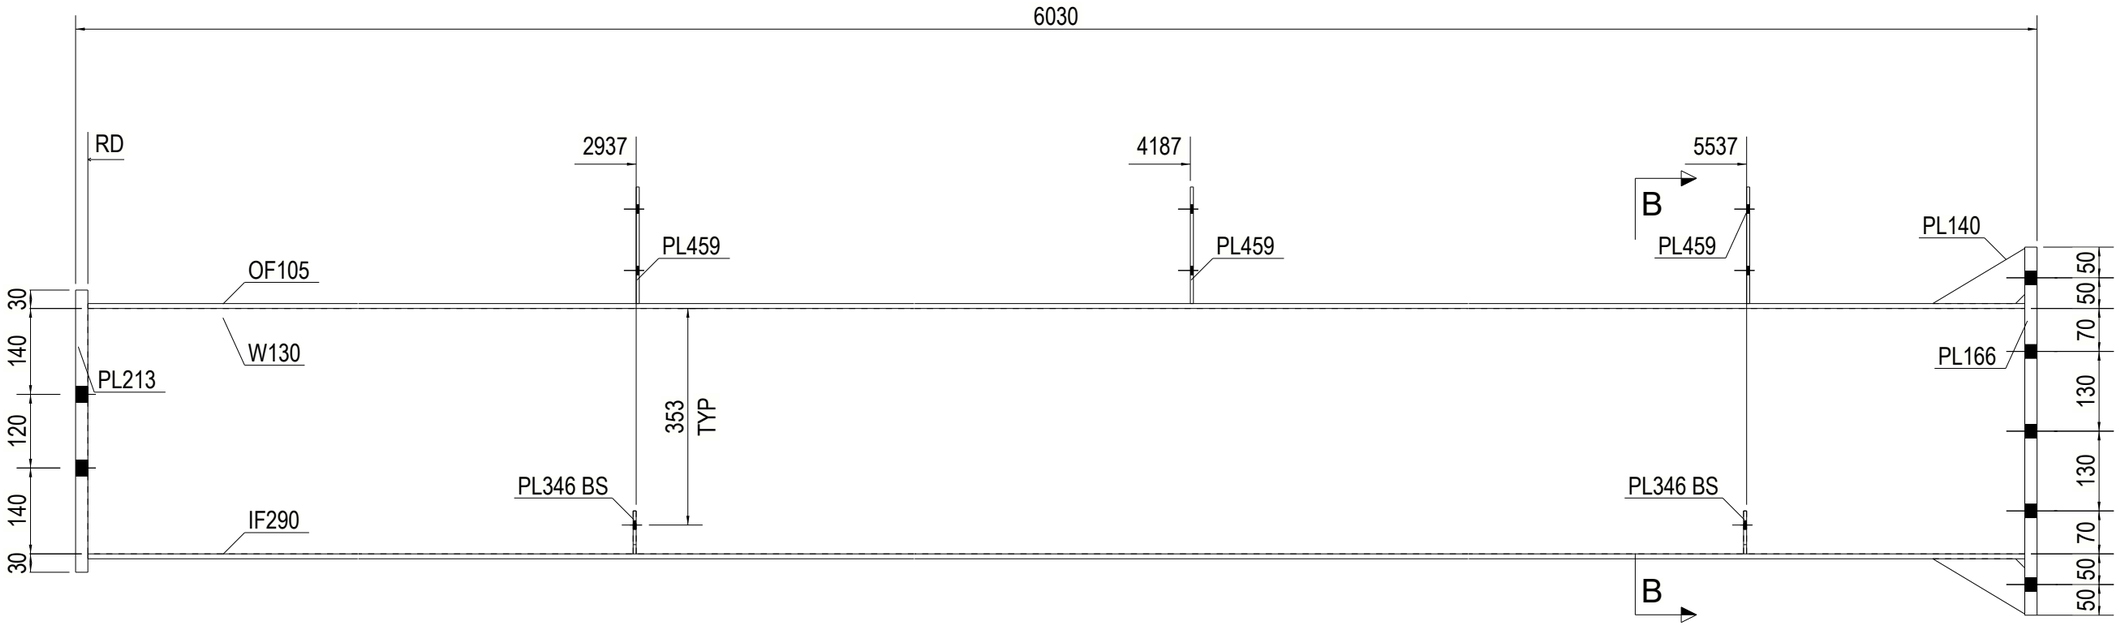

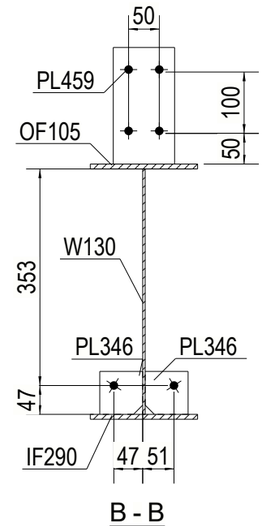

B - B

ASSEMBLY MARK	ITEM NO.	DESCRIPTION	LENGTH	MATERIAL	QTY.	UNIT WT. IN Kgs	WT./ITEM IN Kgs	TOTAL WT. IN Kgs	GRAND TOTAL WT.	ITEM TYPE
	IF290	PLT8*175	5990	S355JR	1	7.85	65.83	65.83		
	OF105	PLT8*175	5990	S355JR	1	7.85	65.83	65.83		
	PL140	PL12*90	150	S355JR	2	7.85	0.63	1.25		
	PL166	PL20*250	600	S355JR	1	7.85	23.55	23.55		
	PL213	PL20*250	460	S355JR	1	7.85	18.06	18.06		
	PL346	PL5*70	70	S355JR	4	7.85	0.19	0.75		
	PL459	PL5*100	190	S355JR	3	7.85	0.75	2.24		
	W130	PLT4*400	5990	S355JR	1	7.85	75.23	75.23		
C135 x 1						TOTAL IN Kgs.		252.74	252.74	LIGHT_STEEL

QTY= 1 Nos. COLUMN MKD : C135

REV.	DATE	DESCRIPTION	DRW	CHK	APP

ELNAGAR

DRAWN			DATE	
CHECKED			SCALE	1:10
REVIEWED			REL. NO.	
ASSEMBLY MARK	C135		SHT. NO.	REV. NO.

Tekla structures