
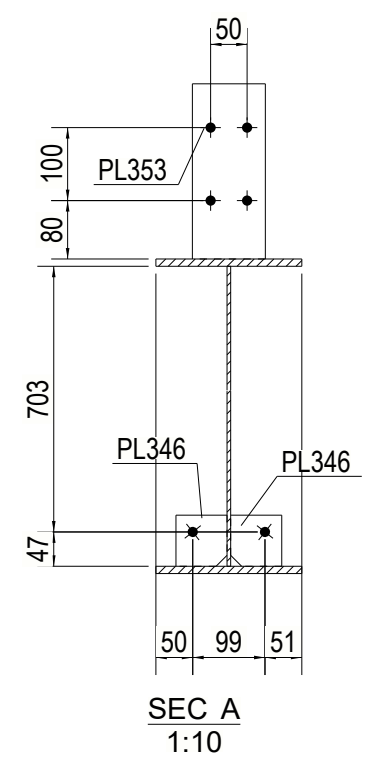


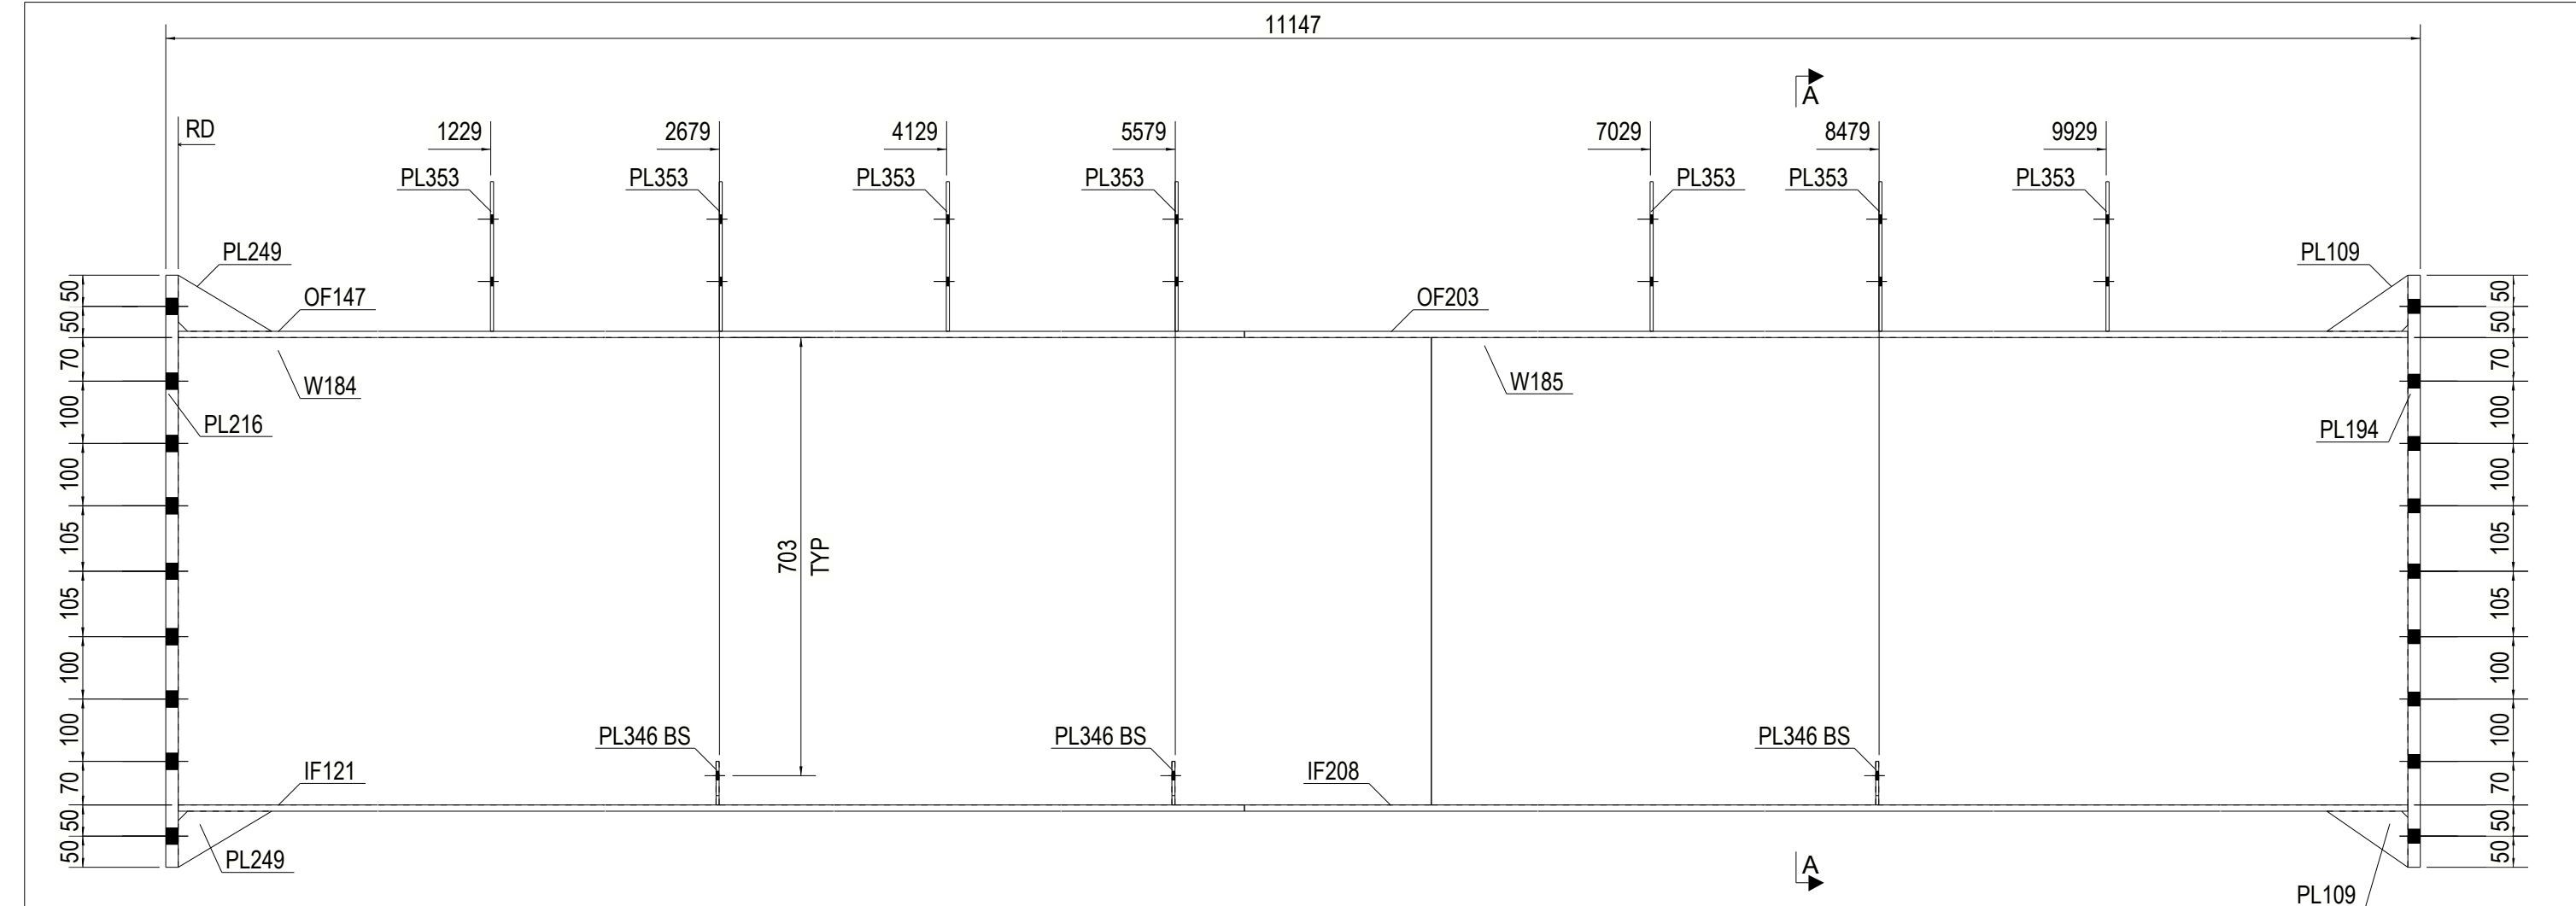

ASSEMBLY MARK	ITEM NO.	DESCRIPTION	LENGTH	MATERIAL	QTY.	UNIT WT. IN Kgs	WT./ITEM IN Kgs	TOTAL WT. IN Kgs	GRAND TOTAL WT.	ITEM TYPE
Tekla structures	IF121	PL10*200	5690	S355JR	1	7.85	89.33	89.33		
	IF208	PL10*200	5417	S355JR	1	7.85	85.05	85.05		
	OF147	PL10*200	5690	S355JR	1	7.85	89.33	89.33		
	OF203	PL10*200	5417	S355JR	1	7.85	85.05	85.05		
	PL109	PL10*90	130	S355JR	2	7.85	0.46	0.91		
	PL194	PL20*400	950	S355JR	1	7.85	59.66	59.66		
	PL216	PL20*250	950	S355JR	1	7.85	37.29	37.29		
	PL249	PL10*90	150	S355JR	2	7.85	0.52	1.04		
	PL346	PL5*70	70	S355JR	6	7.85	0.19	1.13		
	PL353	PL5*100	240	S355JR	7	7.85	0.94	6.59		
	W184	PLT5*750	5990	S355JR	1	7.85	176.33	176.33		
	W185	PLT5*750	5117	S355JR	1	7.85	150.64	150.64		
TOTAL IN Kgs.								782.37	782.37	LIGHT STEEL

QTY= 1 Nos. COLUMN MKD : C149

00	26.02.2026	ISSUED FOR FABRICATION	ZAC	MMD	MMG
REV.	DATE	DESCRIPTION	DRW	CHK	APP
ELNAGAR					
DRAWN	ZAC		DATE	28.04.2026	
CHECKED	MMD		SCALE	1:10	
REVIEWED	MMG		REL. NO.		
ASSEMBLY MARK			SHT. NO.	REV. NO.	
C149				00	