



Tekla structures

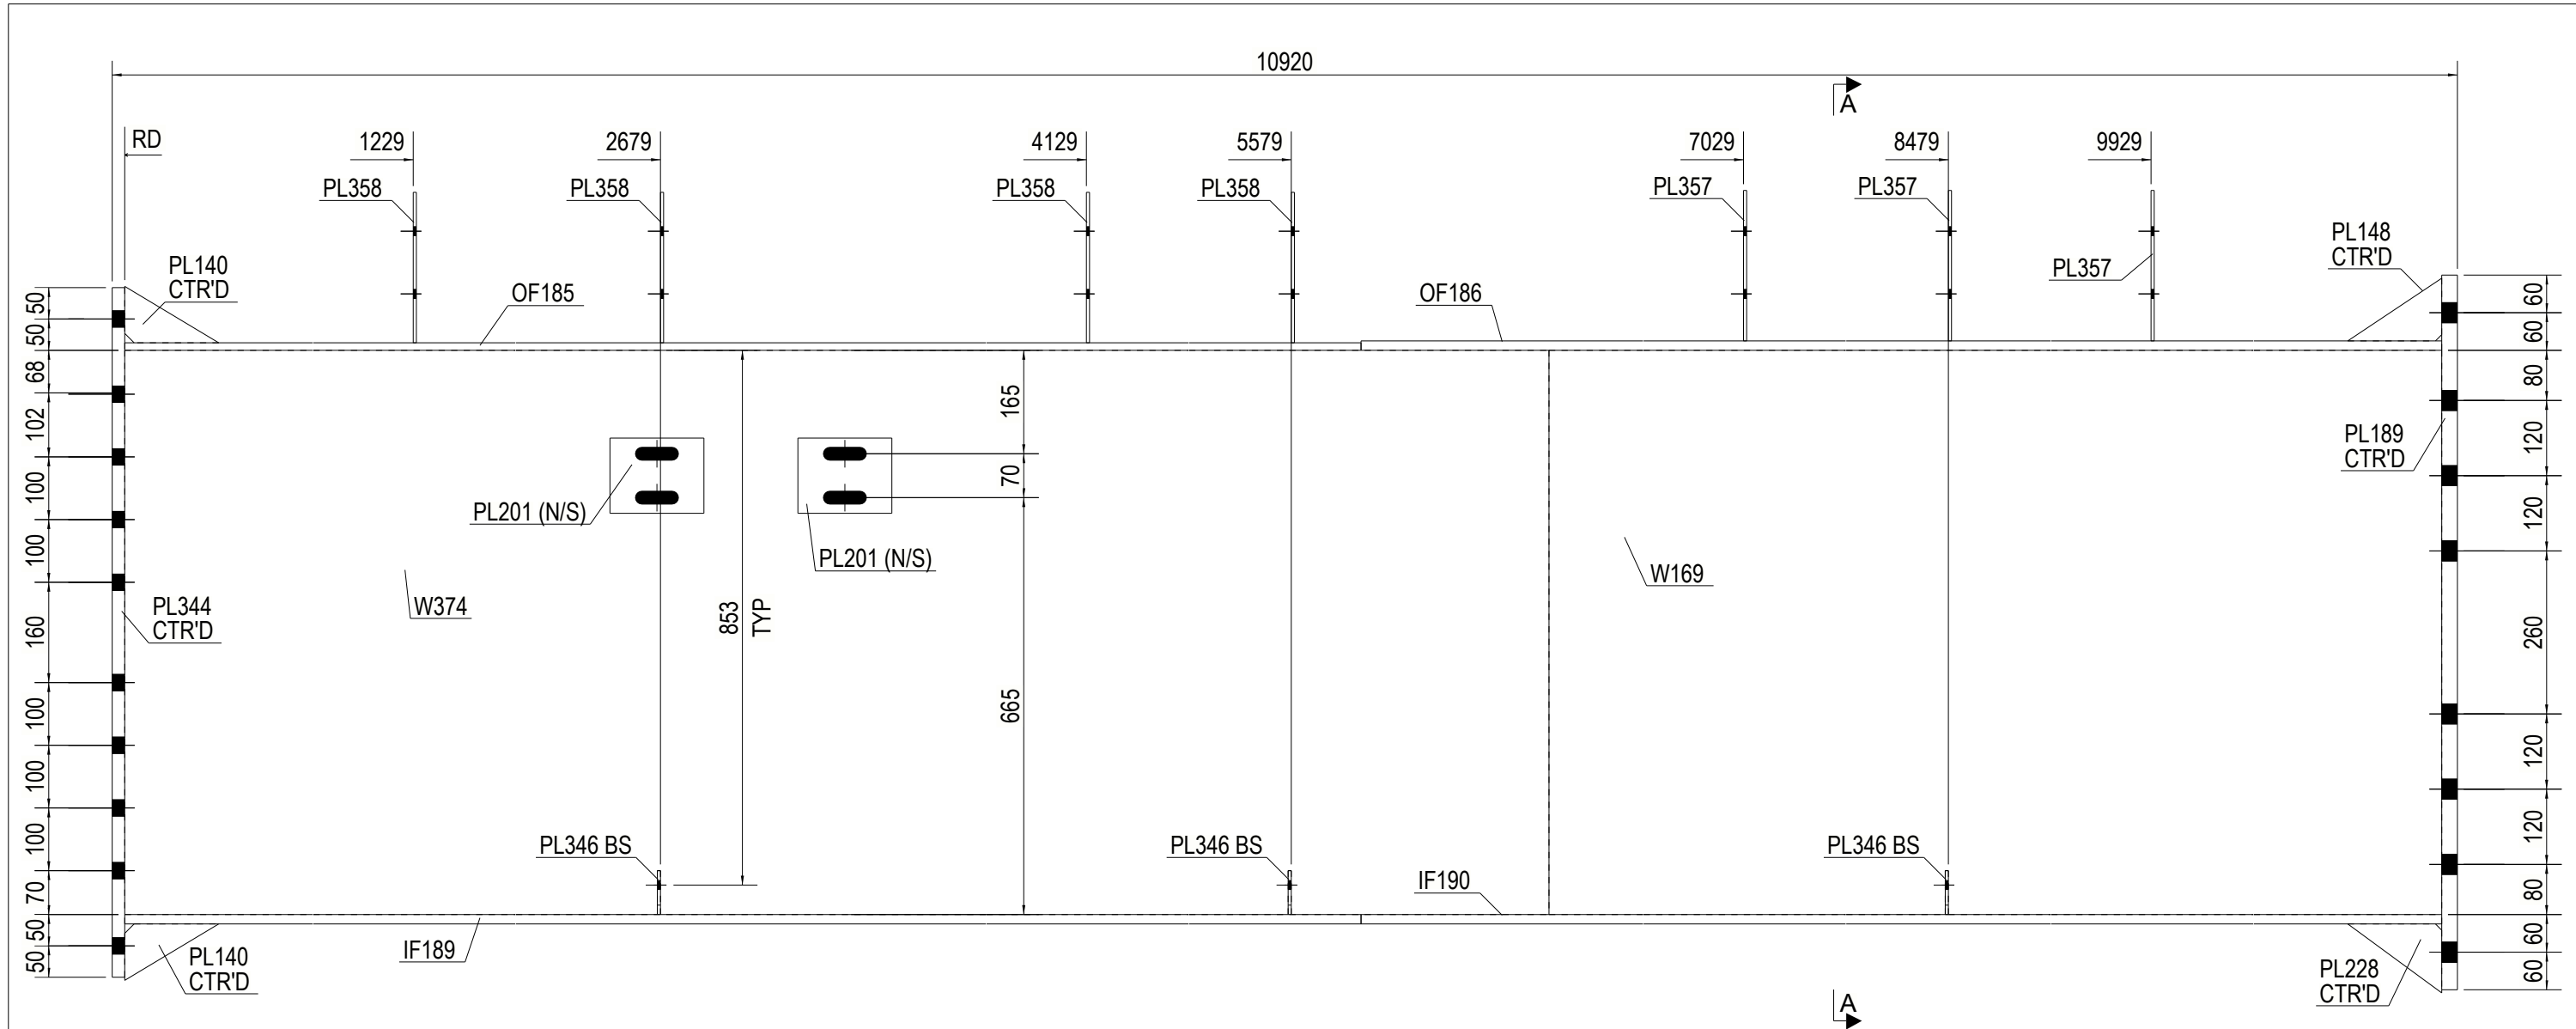

ASSEMBLY MARK	ITEM NO.	DESCRIPTION	LENGTH	MATERIAL	QTY.	UNIT WT. IN Kgs	WT./ITEM IN Kgs	TOTAL WT. IN Kgs	GRAND TOTAL WT.	ITEM TYPE
	IF189	PLT15*225	5690	S355JR	1	7.85	150.75	150.75		
	IF190	PLT15*225	5185	S355JR	1	7.85	137.37	137.37		
	OF185	PLT12*225	5690	S355JR	1	7.85	120.60	120.60		
	OF186	PLT15*225	5185	S355JR	1	7.85	137.37	137.37		
	PL140	PL12*90	150	S355JR	2	7.85	0.63	1.25		
	PL148	PL10*100	150	S355JR	1	7.85	0.58	0.58		
	PL189	PL25*300	1140	S355JR	1	7.85	67.12	67.12		
	PL201	PL6*120	150	S355JR	2	7.85	0.85	1.70		
	PL228	PL10*110	150	S355JR	1	7.85	0.64	0.64		
	PL344	PL20*300	1100	S355JR	1	7.85	51.81	51.81		
	PL346	PL5*70	70	S355JR	6	7.85	0.19	1.13		
	PL357	PL5*100	240	S355JR	3	7.85	0.94	2.83		
	PL358	PL5*100	240	S355JR	4	7.85	0.94	3.77		
	W169	PLT8*900	4885	S355JR	1	7.85	276.10	276.10		
	W374	PLT6*900	5990	S355JR	1	7.85	253.92	253.92		
TOTAL IN Kgs.								1206.93	120***	LIGHT STEEL

C162 x 1

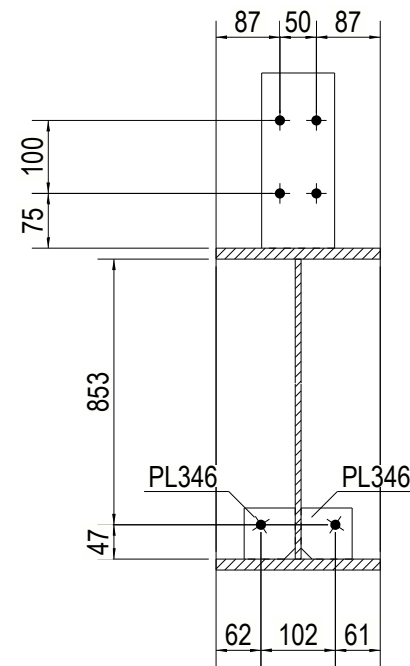

SEC A
1:10

QTY= 1 Nos. COLUMN MKD : C162

00	26.02.2026	ISSUED FOR FABRICATION	ZAC	MMD	MMG
REV.	DATE	DESCRIPTION	DRW	CHK	APP
ELNAGAR					
DRAWN	ZAC		DATE	28.04.2026	
CHECKED	MMD		SCALE	1:10	
REVIEWED	MMG		REL. NO.		
ASSEMBLY MARK			SHT. NO.	REV. NO.	
C162				00	