


Tekla structures

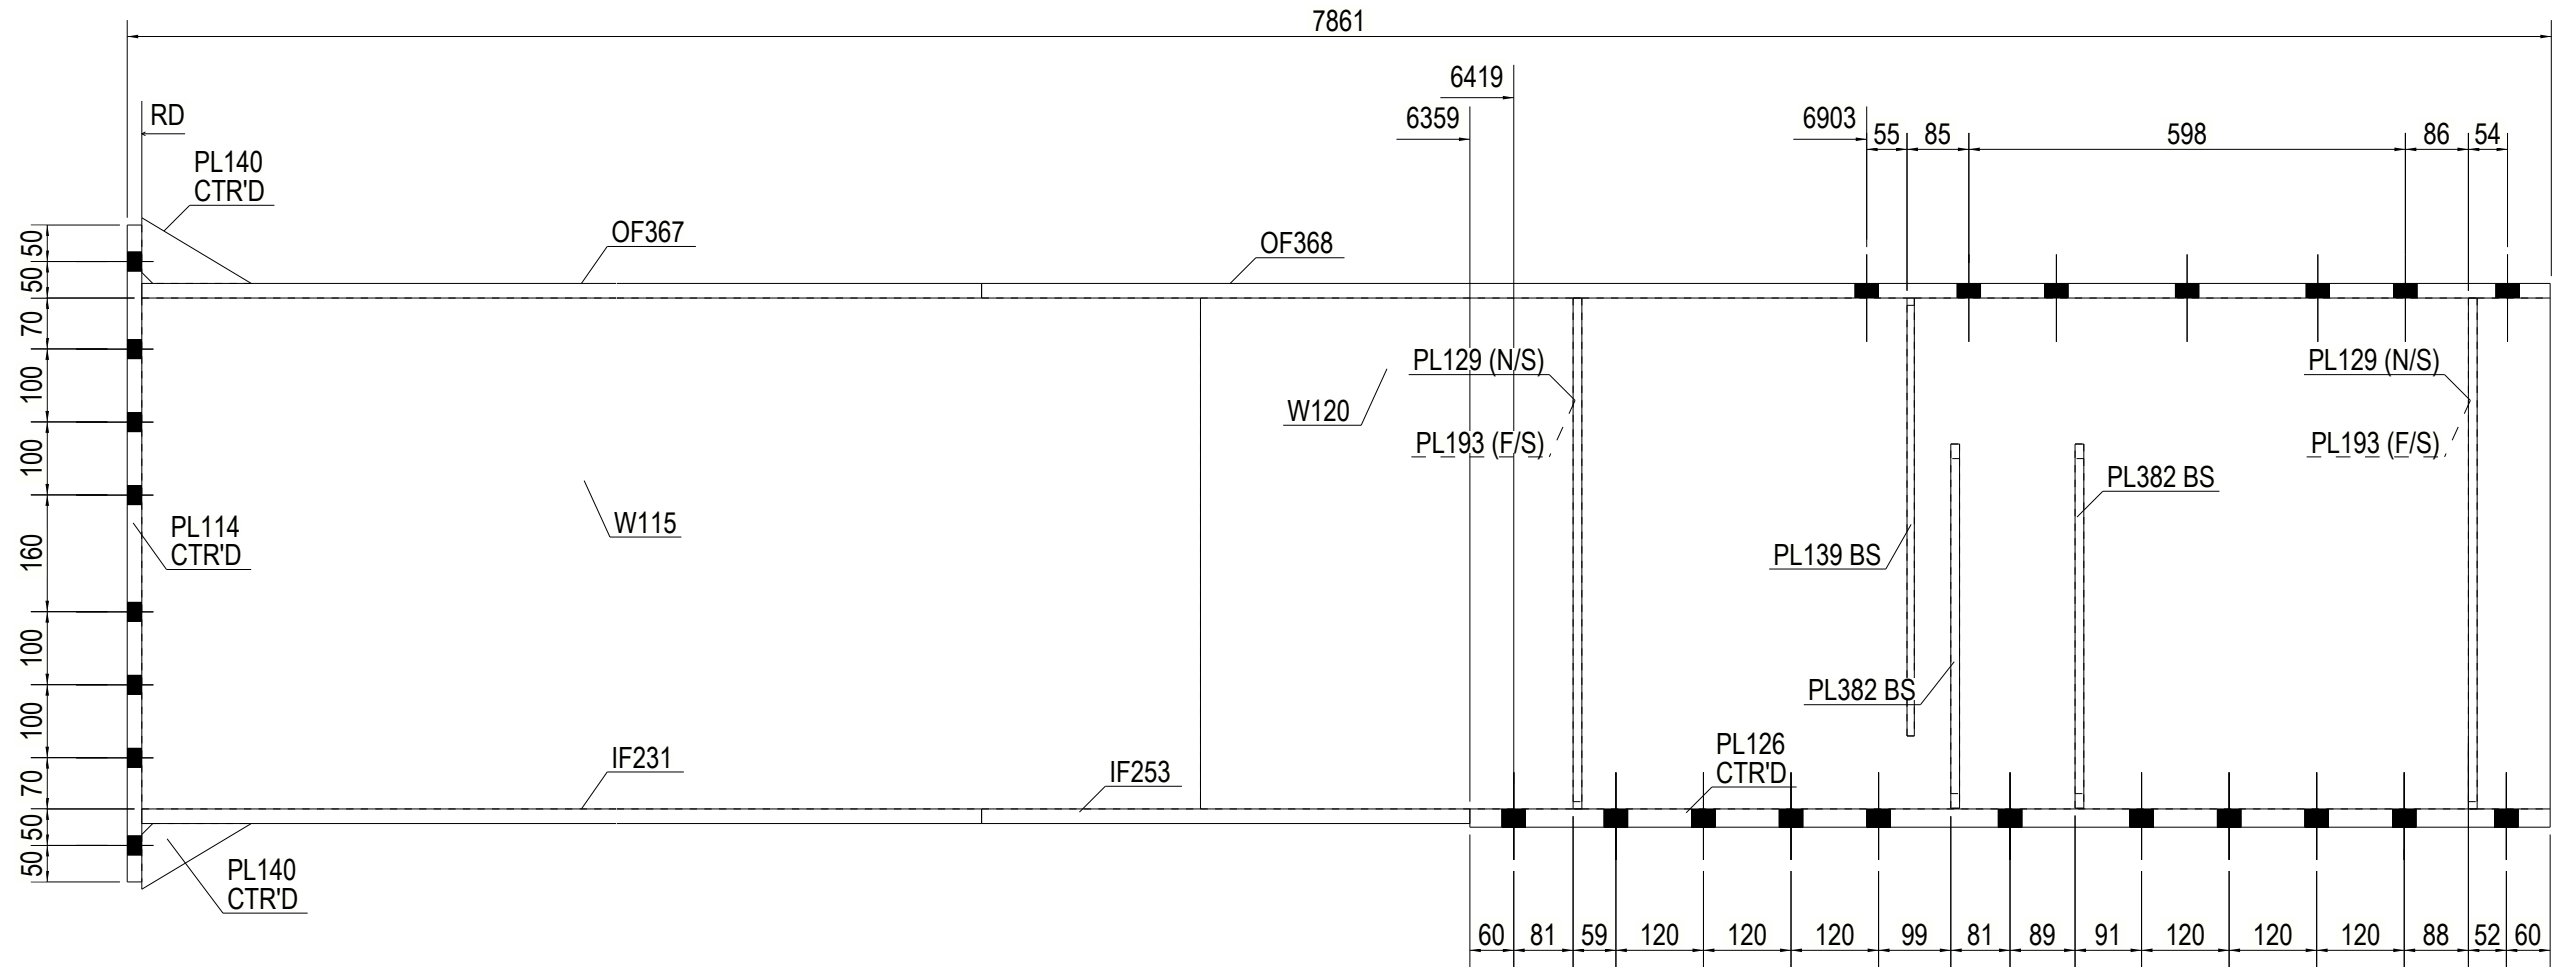

ASSEMBLY MARK	ITEM NO.	DESCRIPTION	LENGTH	MATERIAL	QTY.	UNIT WT. IN Kgs	WT./ITEM IN Kgs	TOTAL WT. IN Kgs	GRAND TOTAL WT.	ITEM TYPE
C20 x 1	IF231	PL20*450	5690	S355JR	1	7.85	402.00	402.00		
	IF253	PL20*450	669	S355JR	1	7.85	47.28	47.28		
	OF367	PL20*450	5690	S355JR	1	7.85	402.00	402.00		
	OF368	PL20*450	2150	S355JR	1	7.85	151.89	151.89		
	PL114	PL20*450	900	S355JR	1	7.85	63.59	63.59		
	PL126	PL25*450	1481	S355JR	1	7.85	130.76	130.76		
	PL129	PLT12*219	700	S355JR	2	7.85	14.44	28.87		
	PL139	PLT10*194	600	S355JR	2	7.85	9.13	18.27		
	PL140	PL12*90	150	S355JR	2	7.85	0.63	1.25		
	PL193	PLT12*194	700	S355JR	2	7.85	12.79	25.58		
	PL382	PL12*190	499	S355JR	4	7.85	8.89	35.57		
	W115	PLT8*700	5990	S355JR	1	7.85	263.32	263.32		
	W120	PLT12*700	1850	S355JR	1	7.85	121.98	121.98		
					TOTAL IN Kgs.		1692.34	169***	LIGHT_STEEL	

QTY= 1 Nos. COLUMN MKD : C20

00	26.02.2026	ISSUED FOR FABRICATION	ZAC	MMD	MMG
REV.	DATE	DESCRIPTION	DRW	CHK	APP
ELNAGAR					
DRAWN	ZAC		DATE	28.04.2026	
CHECKED	MMD		SCALE	1:10	
REVIEWED	MMG		REL. NO.		
ASSEMBLY MARK			SHT. NO.	REV. NO.	
C20				00	