


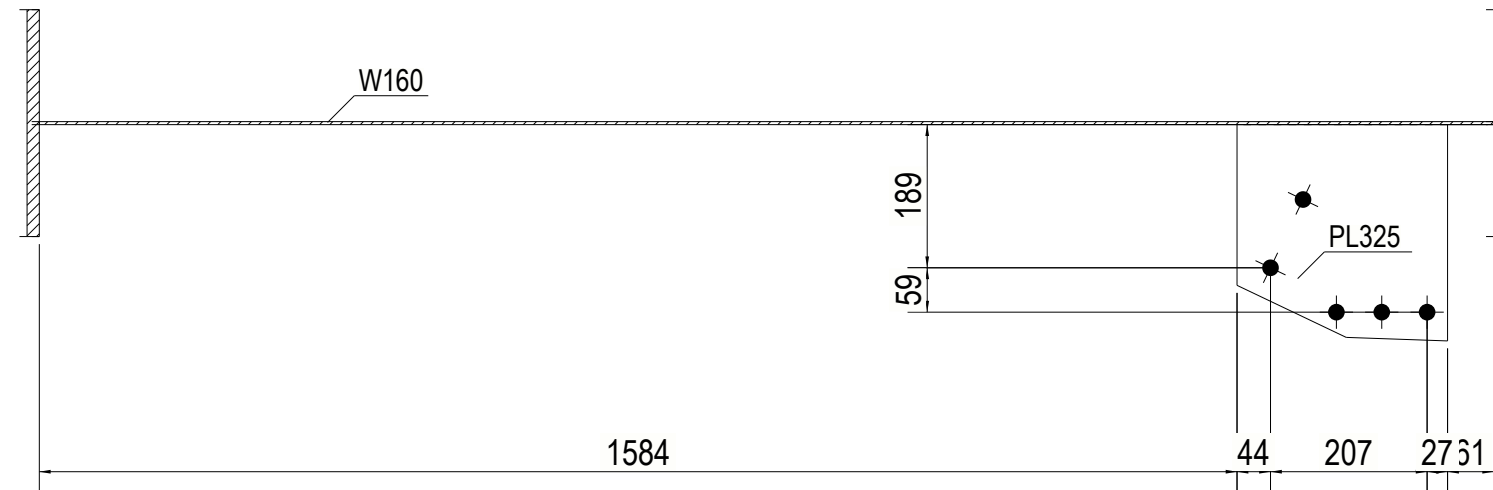

ASSEMBLY MARK	ITEM NO.	DESCRIPTION	LENGTH	MATERIAL	QTY.	UNIT WT. IN Kgs	WT./ITEM IN Kgs	TOTAL WT. IN Kgs	GRAND TOTAL WT.	ITEM TYPE
reka structures	IF176	PLT6*125	1923	S355JR	1	7.85	11.32	11.32		
	OF170	PLT6*125	1923	S355JR	1	7.85	11.32	11.32		
	PL181	PLT16*240	300	S355JR	2	7.85	9.04	18.09		
	PL325	PL12*278.5	286	S355JR	1	7.85	6.94	6.94		
	W160	PLT4*200	1956	S355JR	1	7.85	12.08	12.08		
C25 x 3						TOTAL IN Kgs.		59.75	179.26	LIGHT_STEEL

QTY= 3 Nos. COLUMN MKD : C25

REV.	DATE	DESCRIPTION	DRW	CHK	APP
ELNAGAR					
DRAWN			DATE		
CHECKED			SCALE	1:5	
REVIEWED			REL. NO.		
ASSEMBLY MARK			SHT. NO.	REV. NO.	
C25					