



Tekla structures

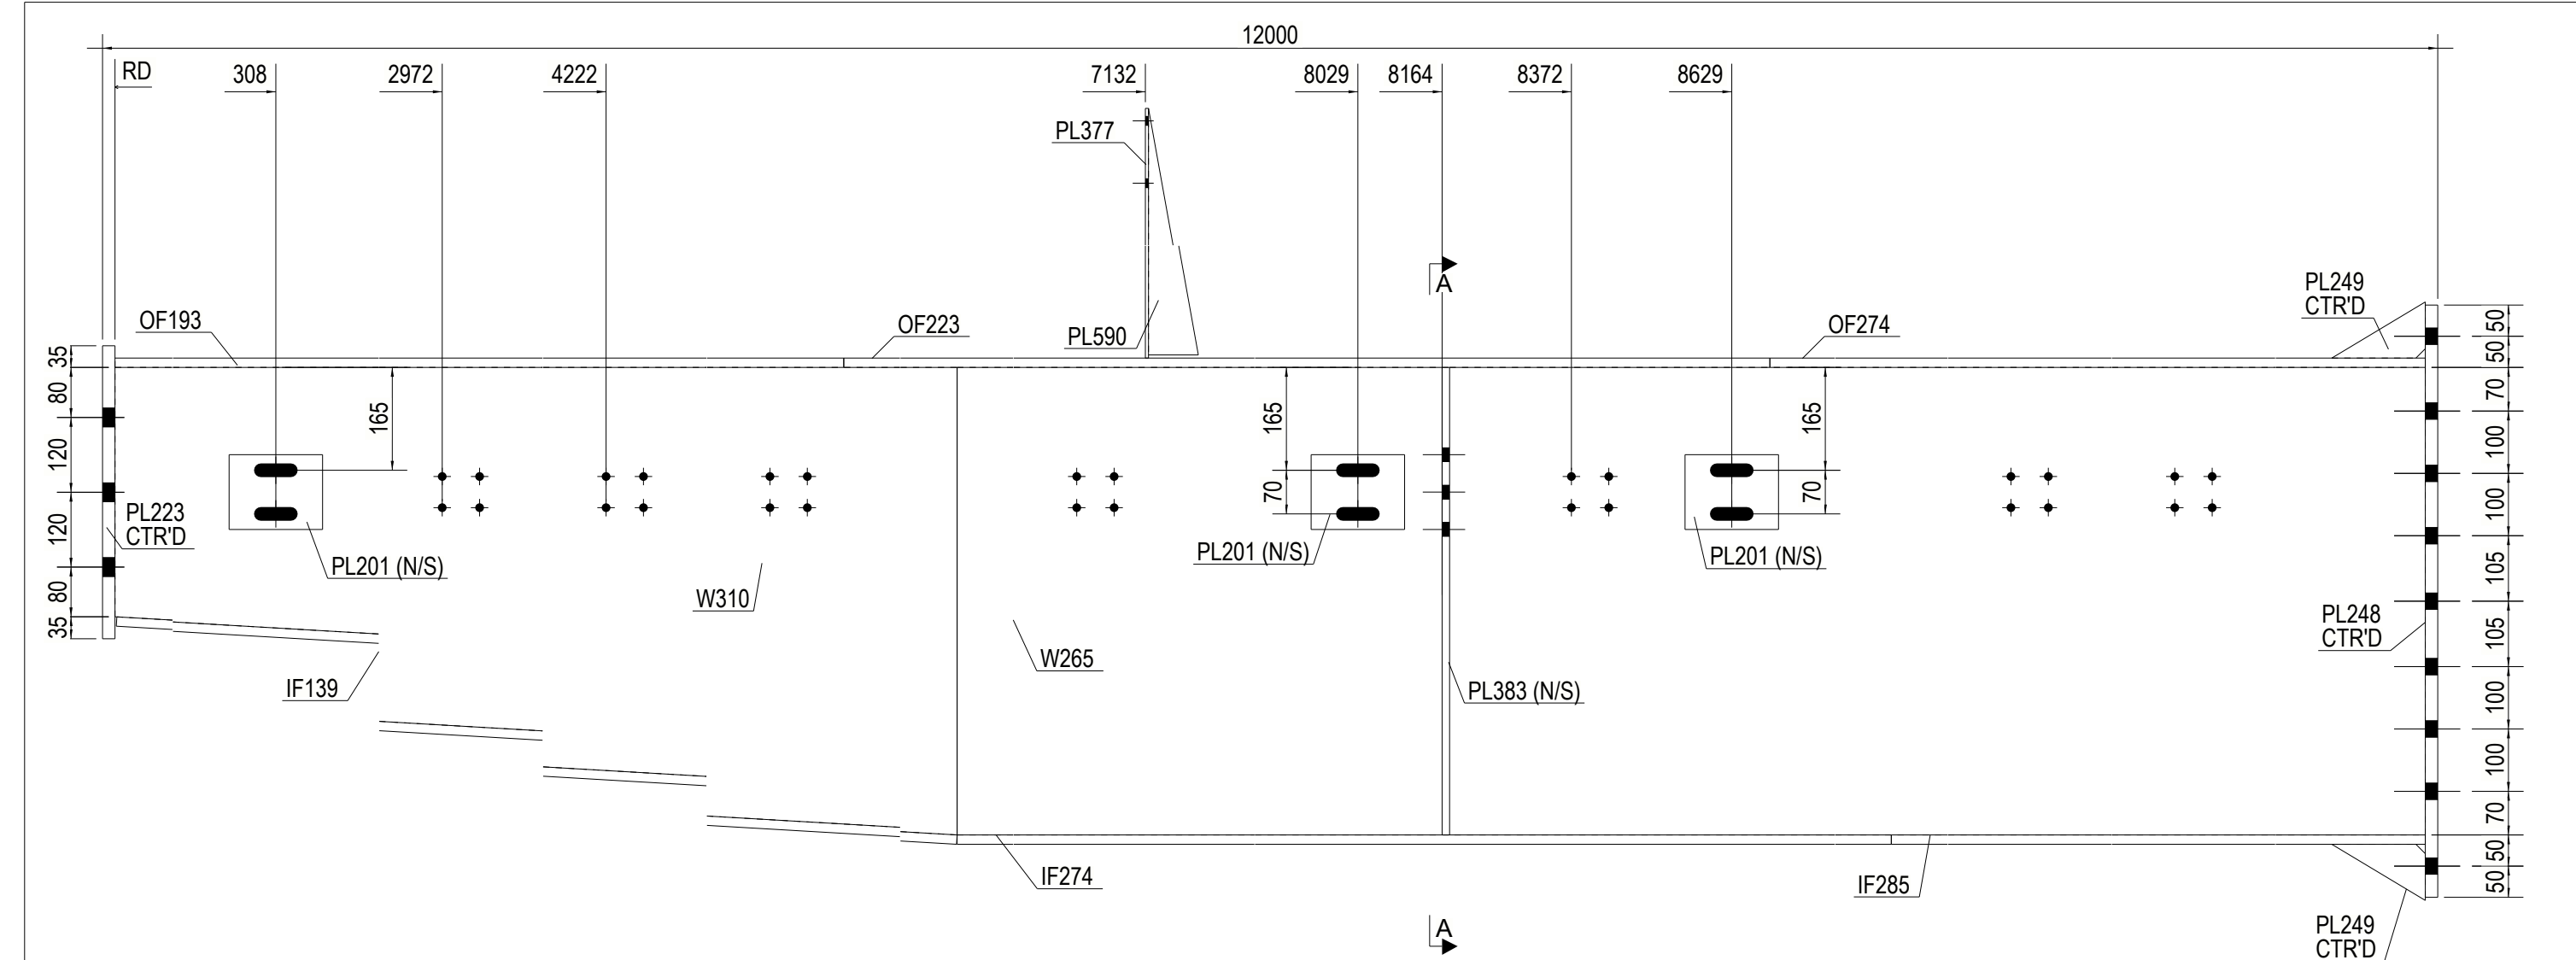

ASSEMBLY MARK	ITEM NO.	DESCRIPTION	LENGTH	MATERIAL	QTY.	UNIT WT. IN Kgs	WT./ITEM IN Kgs	TOTAL WT. IN Kgs	GRAND TOTAL WT.	ITEM TYPE
	IF139	PL15*400	5997	S355JR	1	7.85	282.47	282.47		
	IF274	PL15*400	3000	S355JR	1	7.85	141.30	141.30		
	IF285	PL15*400	2970	S355JR	1	7.85	139.89	139.89		
	OF193	PL15*400	5690	S355JR	1	7.85	268.00	268.00		
	OF223	PL15*400	3000	S355JR	1	7.85	141.30	141.30		
	OF274	PL15*400	3270	S355JR	1	7.85	154.02	154.02		
	PL201	PL6*120	150	S355JR	3	7.85	0.85	2.54		
	PL223	PL20*500	470	S355JR	1	7.85	36.90	36.90		
	PL248	PL20*400	950	S355JR	1	7.85	59.66	59.66		
	PL249	PL10*90	150	S355JR	2	7.85	0.52	1.04		
	PL377	PL5*100	450	S355JR	1	7.85	1.77	1.77		
	PL383	PL12*130	750	S355JR	1	7.85	9.18	9.18		
	PL590	PL5*80	445	S355JR	1	7.85	0.70	0.70		
	W265	PLT6*750	5970	S355JR	1	7.85	210.89	210.89		
	W310	PLT6*750	5990	S355JR	1	7.85	162.22	162.22		
TOTAL IN Kgs.								1611.88	161***	LIGHT_STEEL

C28 x 1

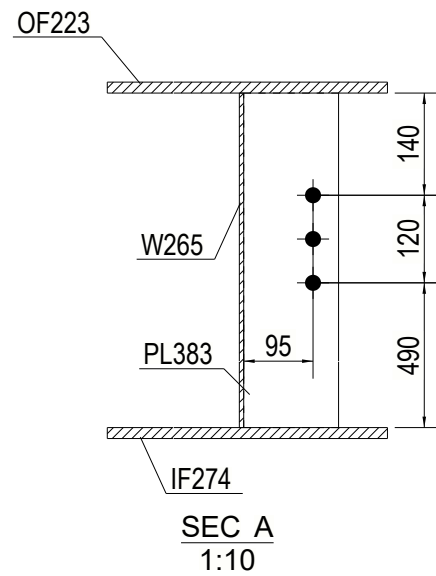

SEC A
1:10

QTY= 1 Nos. COLUMN MKD : C28

REV.	DATE	DESCRIPTION	DRW	CHK	APP
ELNAGAR					
DRAWN			DATE		
CHECKED			SCALE	1:10	
REVIEWED			REL. NO.		
ASSEMBLY MARK			SHT. NO.	REV. NO.	

C28