


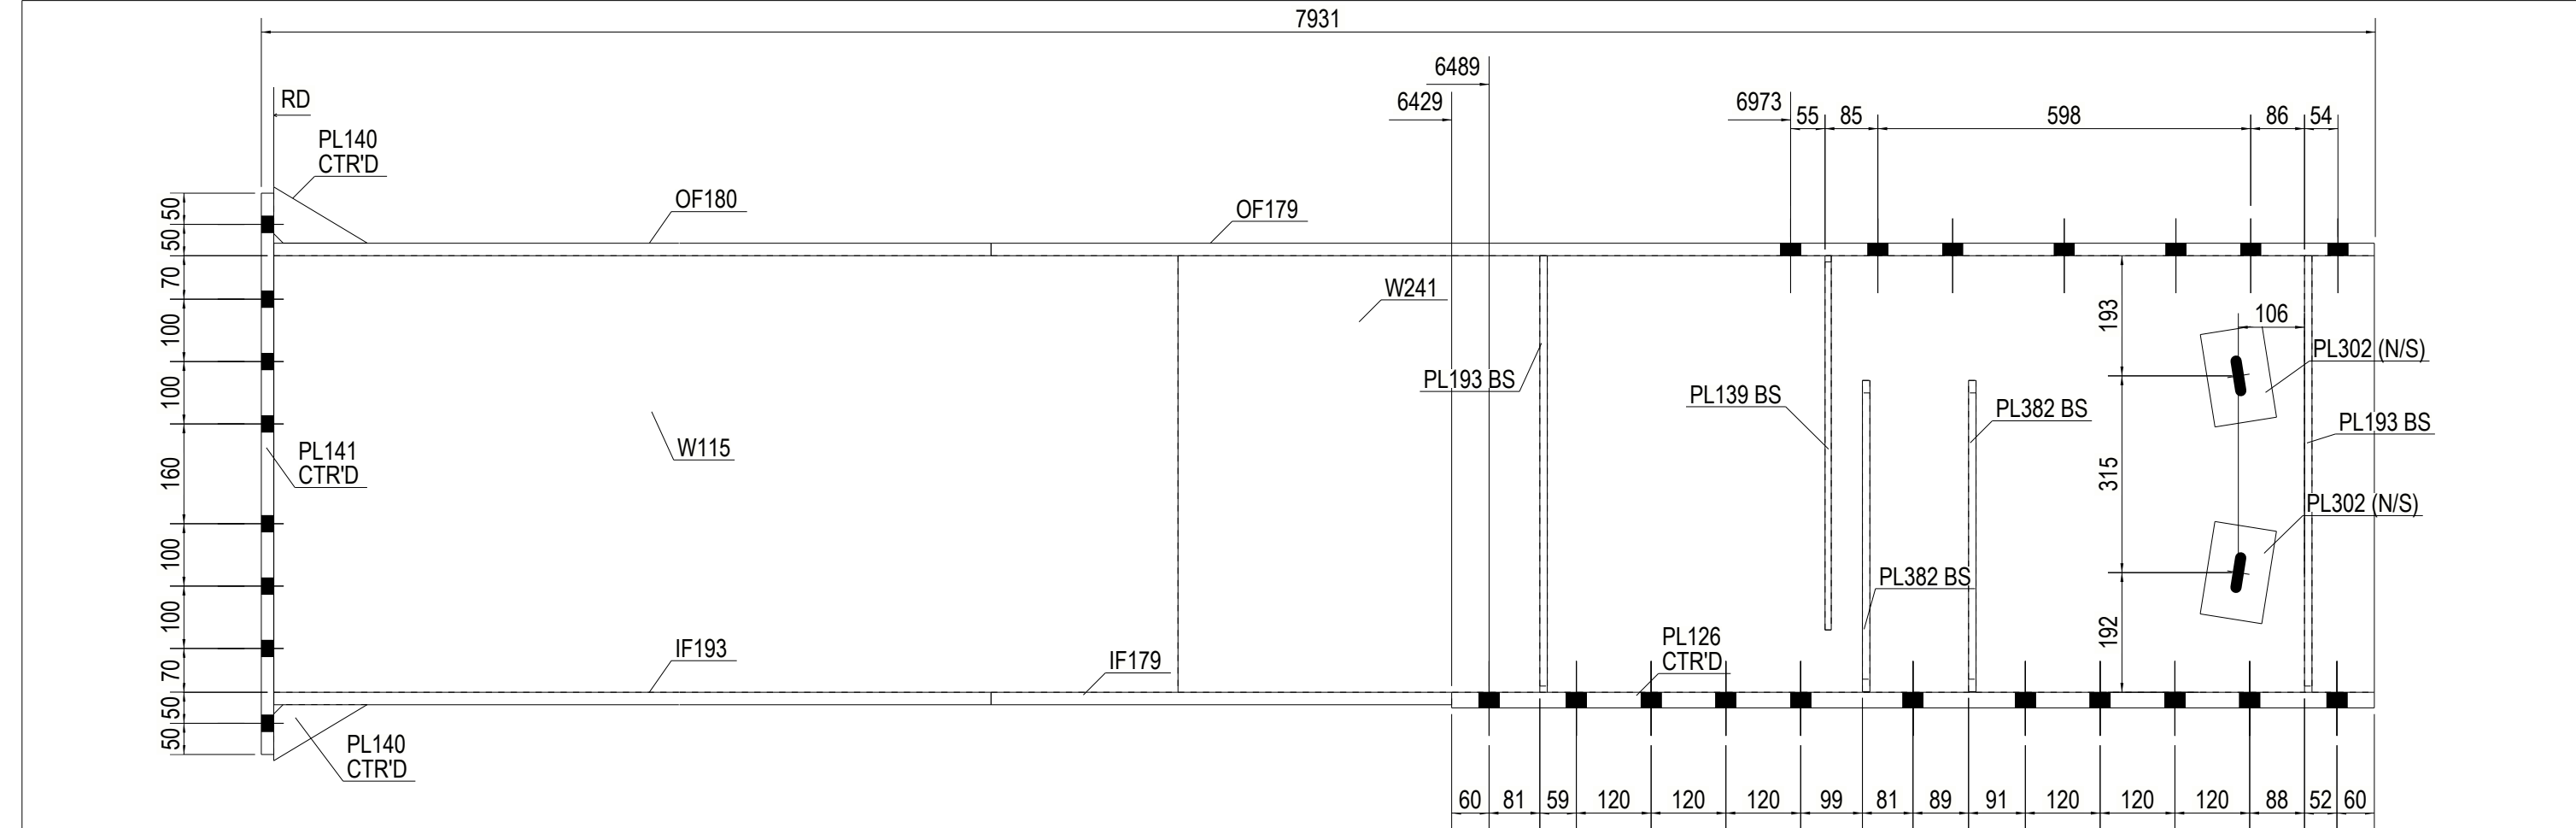

ASSEMBLY MARK	ITEM NO.	DESCRIPTION	LENGTH	MATERIAL	QTY.	UNIT WT. IN Kgs	WT./ITEM IN Kgs	TOTAL WT. IN Kgs	GRAND TOTAL WT.	ITEM TYPE
Tekla structures	IF179	PL20*400	739	S355JR	1	7.85	46.42	46.42		
	IF193	PL20*400	5690	S355JR	1	7.85	357.33	357.33		
	OF179	PL20*400	2220	S355JR	1	7.85	139.40	139.40		
	OF180	PL20*400	5690	S355JR	1	7.85	357.33	357.33		
	PL126	PL25*450	1481	S355JR	1	7.85	130.76	130.76		
	PL139	PLT10*194	600	S355JR	2	7.85	9.13	18.27		
	PL140	PL12*90	150	S355JR	2	7.85	0.63	1.25		
	PL141	PL20*400	900	S355JR	1	7.85	56.52	56.52		
	PL193	PLT12*194	700	S355JR	4	7.85	12.79	51.15		
	PL302	PL6*100	150	S355JR	2	7.85	0.71	1.41		
	PL382	PL12*190	499	S355JR	4	7.85	8.89	35.57		
	W115	PLT8*700	5990	S355JR	1	7.85	263.32	263.32		
	W241	PLT12*700	1920	S355JR	1	7.85	126.59	126.59		
TOTAL IN Kgs.								1585.35	317***	LIGHT_STEEL

QTY= 2 Nos. COLUMN MKD : C33

00	26.02.2026	ISSUED FOR FABRICATION	ZAC	MMD	MMG
REV.	DATE	DESCRIPTION	DRW	CHK	APP
ELNAGAR					
DRAWN	ZAC		DATE	28.04.2026	
CHECKED	MMD		SCALE	1:10	
REVIEWED	MMG		REL. NO.		
ASSEMBLY MARK			SHT. NO.	REV. NO.	
C33				00	