
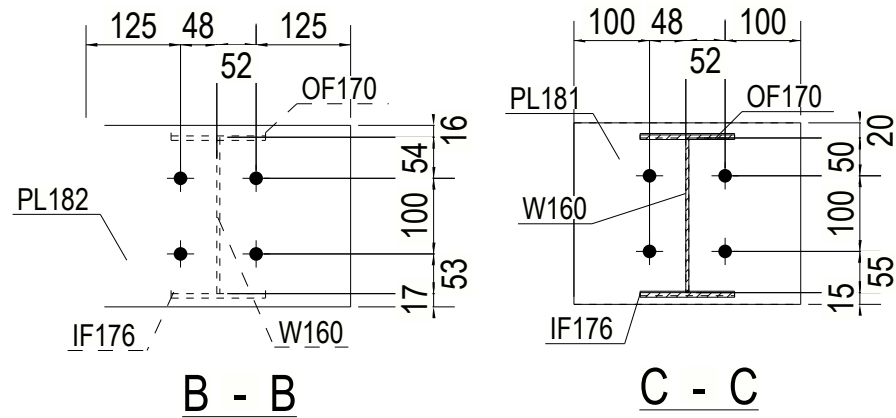


Tekla structures

ASSEMBLY MARK	ITEM NO.	DESCRIPTION	LENGTH	MATERIAL	QTY.	UNIT WT. IN Kgs	WT./ITEM IN Kgs	TOTAL WT. IN Kgs	GRAND TOTAL WT.	ITEM TYPE
C35 x 1	IF176	PLT6*125	1923	S355JR	1	7.85	11.32	11.32		
	OF170	PLT6*125	1923	S355JR	1	7.85	11.32	11.32		
	PL181	PLT16*240	300	S355JR	1	7.85	9.04	9.04		
	PL182	PLT16*240	350	S355JR	1	7.85	10.55	10.55		
	PL325	PL12*278.5	286	S355JR	1	7.85	6.94	6.94		
	W160	PLT4*200	1956	S355JR	1	7.85	12.08	12.08		
TOTAL IN Kgs.								61.26	61.26	LIGHT_STEEL

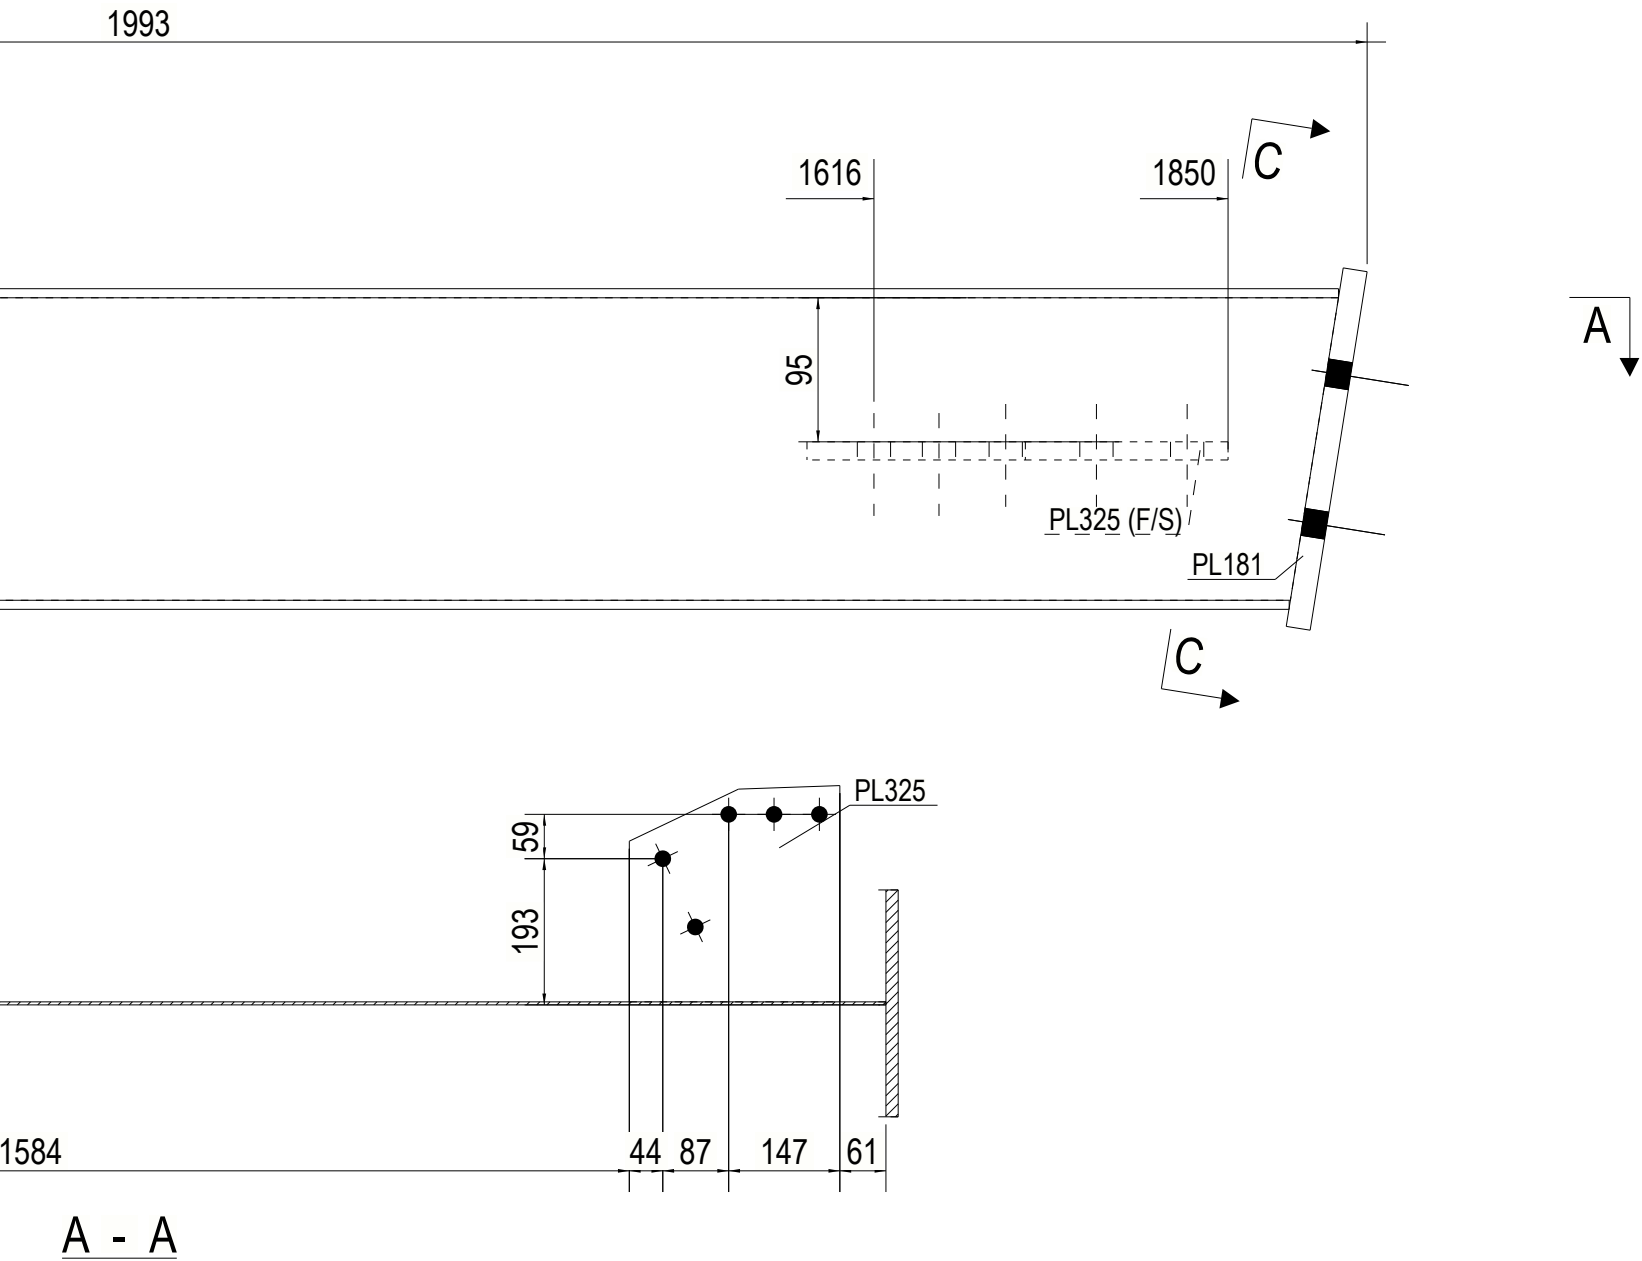

QTY= 1 Nos. COLUMN MKD : C35

REV.	DATE	DESCRIPTION	DRW	CHK	APP
ELNAGAR					
DRAWN		DATE			
CHECKED		SCALE		1:5	
REVIEWED		REL. NO.			
ASSEMBLY MARK		SHT. NO.		REV. NO.	