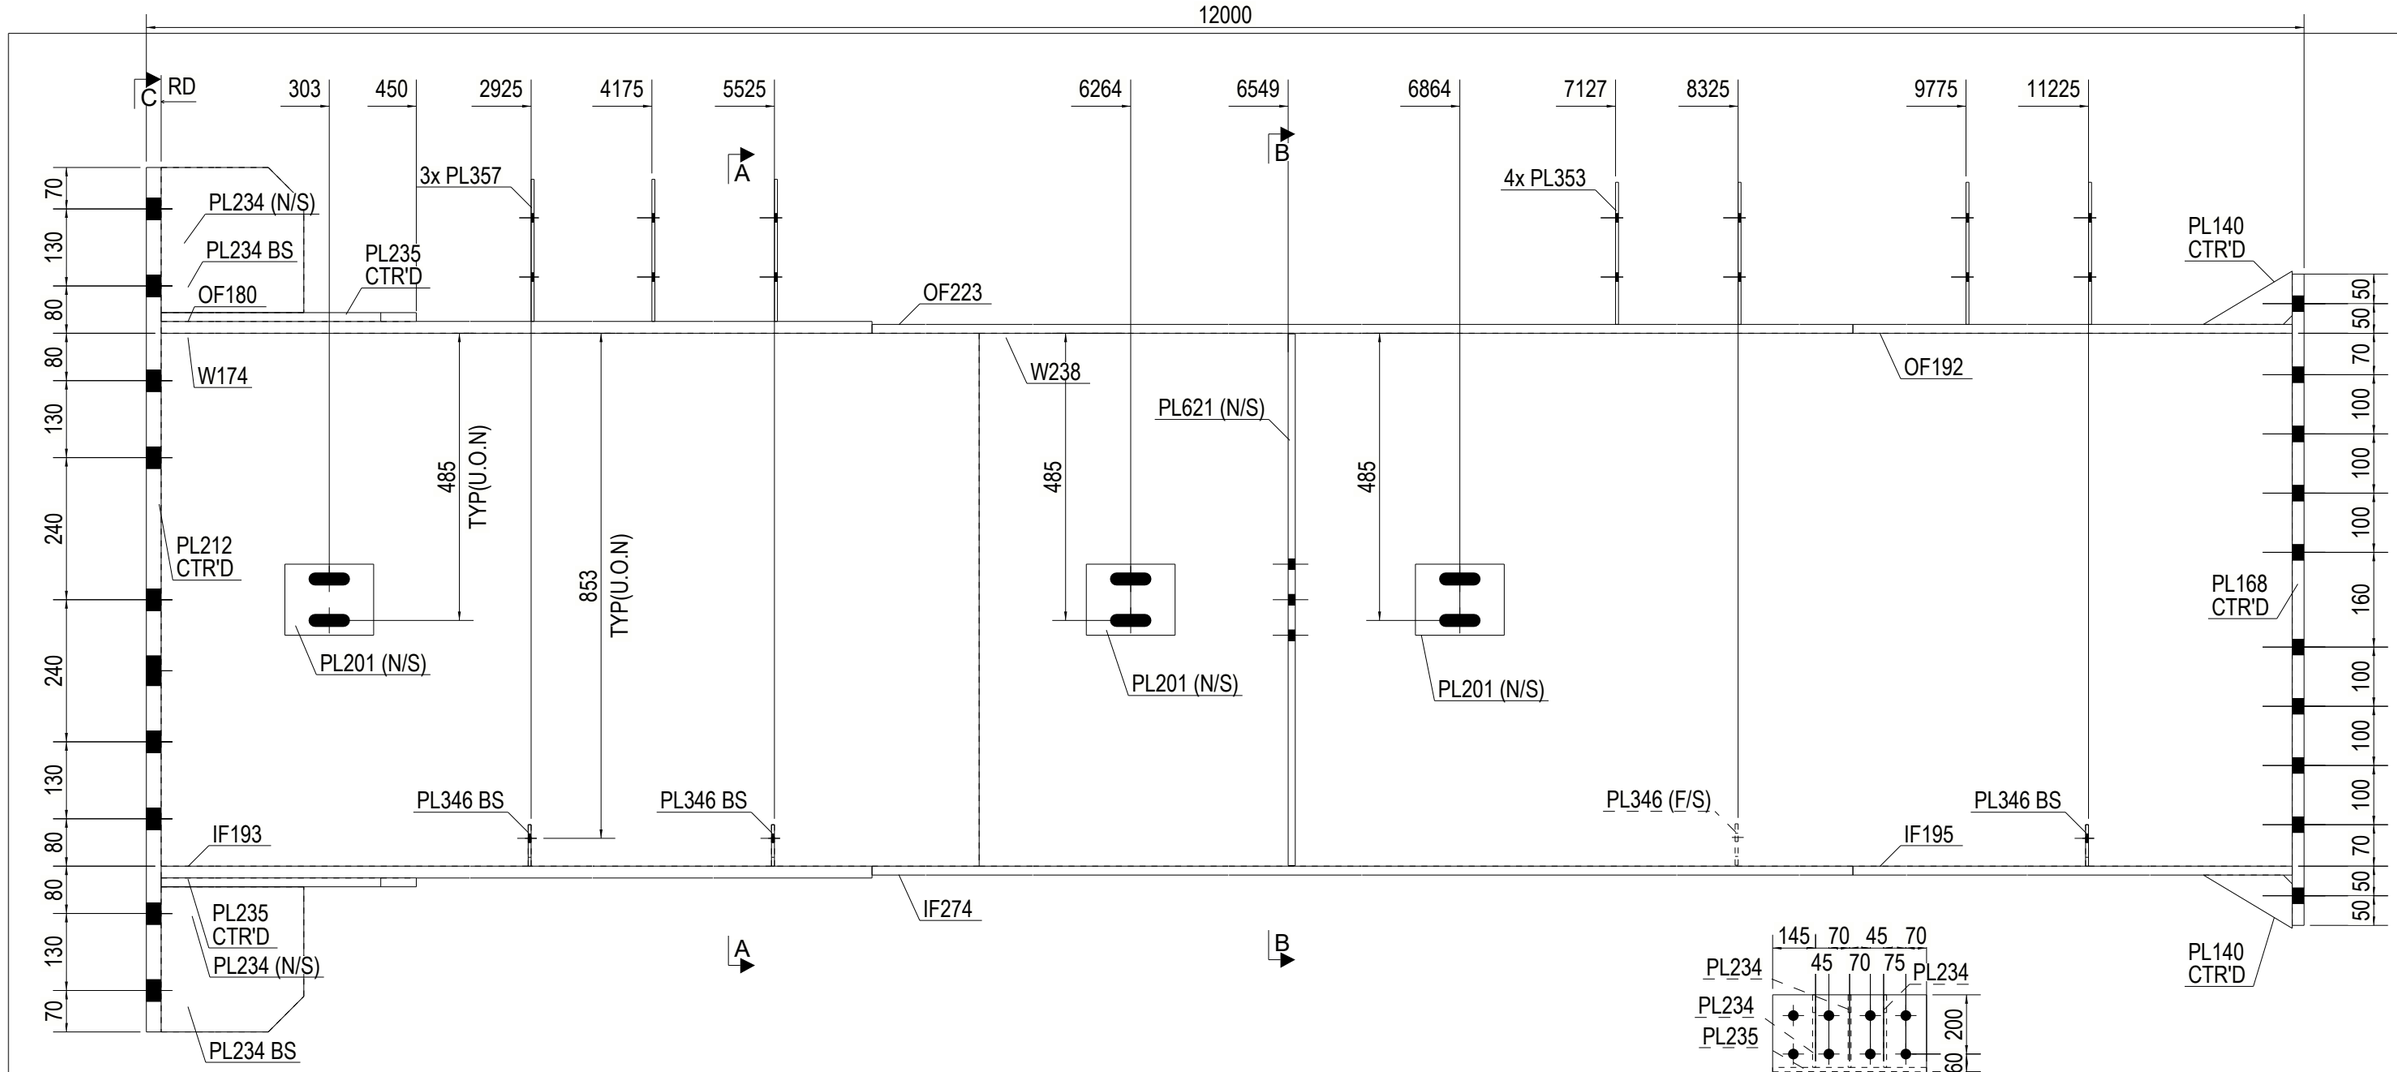

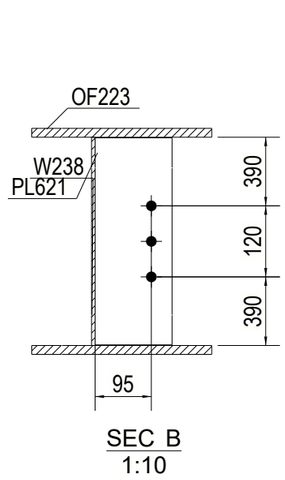

SEC B
1:10

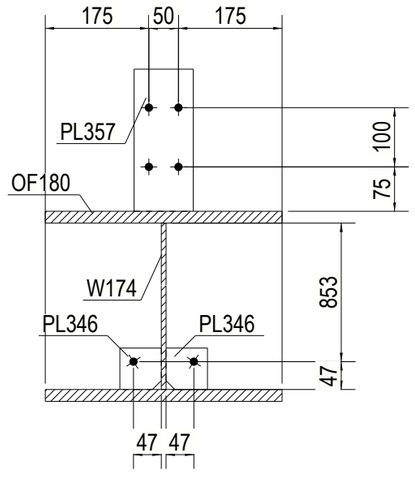

SEC A
1:10

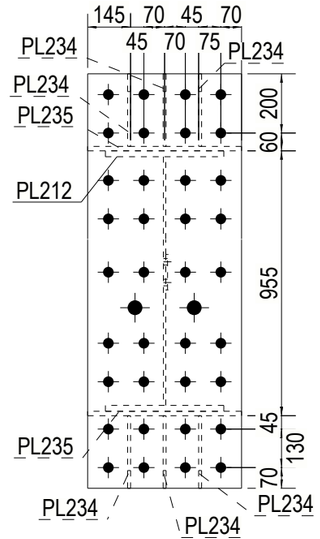

SEC C
1:20

ASSEMBLY MARK	ITEM NO.	DESCRIPTION	LENGTH	MATERIAL	QTY.	UNIT WT. IN Kgs	WT./ITEM IN Kgs	TOTAL WT. IN Kgs	GRAND TOTAL WT.	ITEM TYPE
	IF193	PL20*400	5690	S355JR	1	7.85	357.33	357.33		
	IF195	PL15*400	3265	S355JR	1	7.85	153.78	153.78		
	IF274	PL15*400	3000	S355JR	1	7.85	141.30	141.30		
	OF180	PL20*400	5690	S355JR	1	7.85	357.33	357.33		
	OF192	PL15*400	3265	S355JR	1	7.85	153.78	153.78		
	OF223	PL15*400	3000	S355JR	1	7.85	141.30	141.30		
	PL140	PL12*90	150	S355JR	2	7.85	0.63	1.25		
	PL168	PL20*400	1100	S355JR	1	7.85	69.08	69.08		
	PL201	PL6*120	150	S355JR	3	7.85	0.85	2.54		
	PL212	PL25*520	1460	S355JR	1	7.85	148.99	148.99		
	PL234	PL10*245	260	S355JR	6	7.85	4.86	29.15		
	PL235	PL15*450	520	S355JR	2	7.85	27.13	54.26		
	PL346	PL5*70	70	S355JR	7	7.85	0.19	1.32		
	PL353	PL5*100	240	S355JR	4	7.85	0.94	3.77		
	PL357	PL5*100	240	S355JR	3	7.85	0.94	2.83		
	PL621	PL12*130	898	S355JR	1	7.85	11.00	11.00		
	W174	PLT8*900	5990	S355JR	1	7.85	338.55	338.55		
	W238	PLT6*900	5965	S355JR	1	7.85	252.86	252.86		
C46 x 1						TOTAL IN Kgs.		2220.43	222***	LIGHT_STEEL

QTY= 1 Nos. COLUMN MKD : C46

REV.	DATE	DESCRIPTION	DRW	CHK	APP

ELNAGAR

DRAWN			DATE	
CHECKED			SCALE	1:10
REVIEWED			REL. NO.	
ASSEMBLY MARK	C46		SHT. NO.	REV. NO.

Tekla structures