


Tekla structures

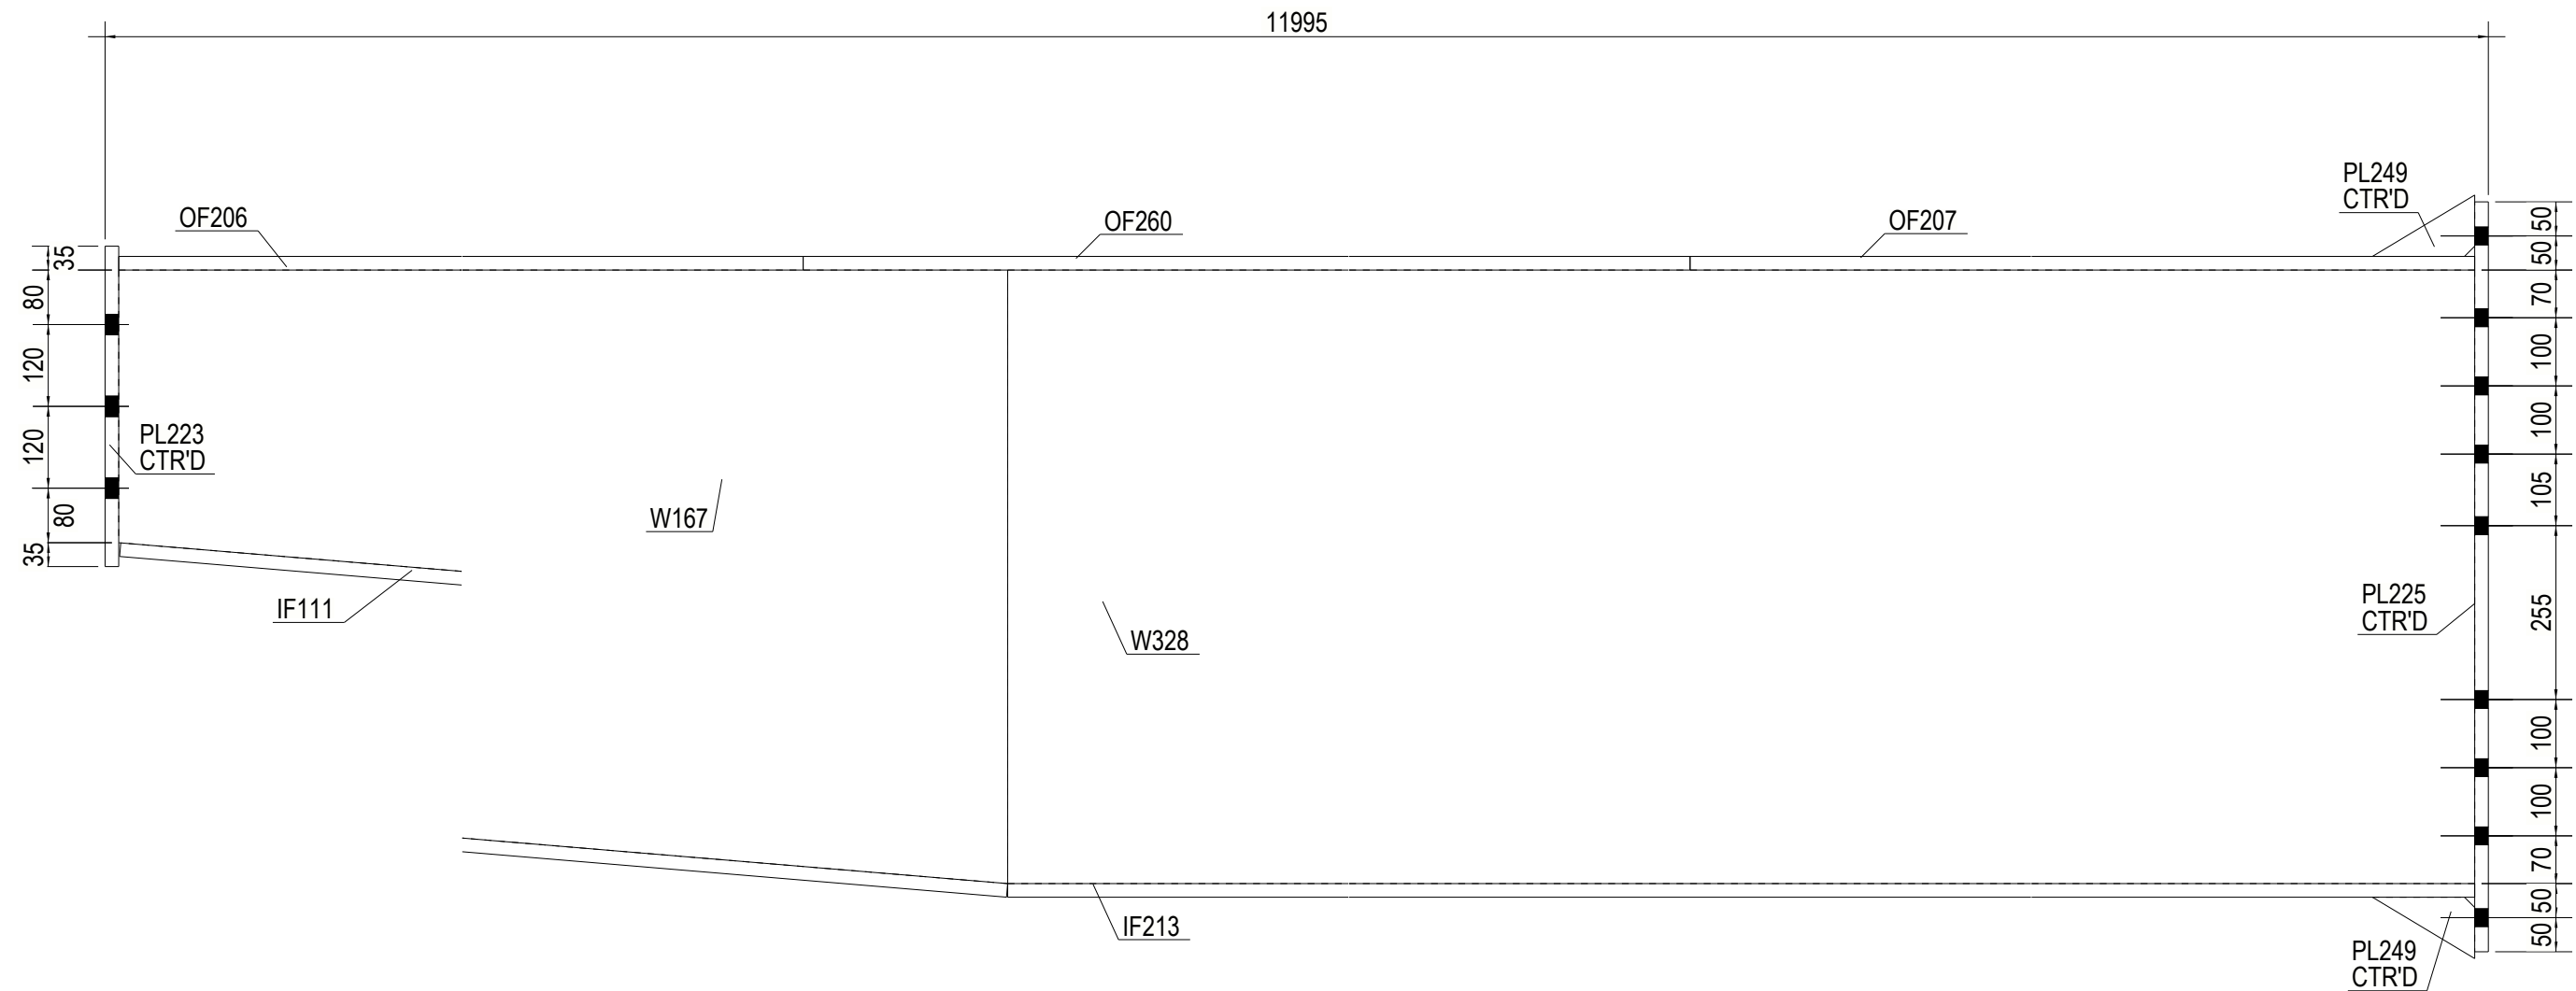

ASSEMBLY MARK	ITEM NO.	DESCRIPTION	LENGTH	MATERIAL	QTY.	UNIT WT. IN Kgs	WT./ITEM IN Kgs	TOTAL WT. IN Kgs	GRAND TOTAL WT.	ITEM TYPE
	IF111	PL20*500	6008	S355JR	1	7.85	471.61	471.61		
	IF213	PL20*500	5965	S355JR	1	7.85	468.25	468.25		
	OF206	PL20*500	5690	S355JR	1	7.85	446.67	446.67		
	OF207	PL20*500	3265	S355JR	1	7.85	256.30	256.30		
	OF260	PL20*500	3000	S355JR	1	7.85	235.50	235.50		
	PL223	PL20*500	470	S355JR	1	7.85	36.90	36.90		
	PL225	PL20*500	1100	S355JR	1	7.85	86.35	86.35		
	PL249	PL10*90	150	S355JR	2	7.85	0.52	1.04		
	W167	PLT8*900	5990	S355JR	1	7.85	244.51	244.51		
	W328	PLT10*900	5965	S355JR	1	7.85	421.43	421.43		
TOTAL IN Kgs.								2668.56	266***	LIGHT_STEEL

C49 x 1

QTY= 1 Nos. COLUMN MKD : C49

REV.	DATE	DESCRIPTION	DRW	CHK	APP
ELNAGAR					
DRAWN			DATE		
CHECKED			SCALE		1:10
REVIEWED			REL. NO.		
ASSEMBLY MARK			SHT. NO.		REV. NO.

C49