



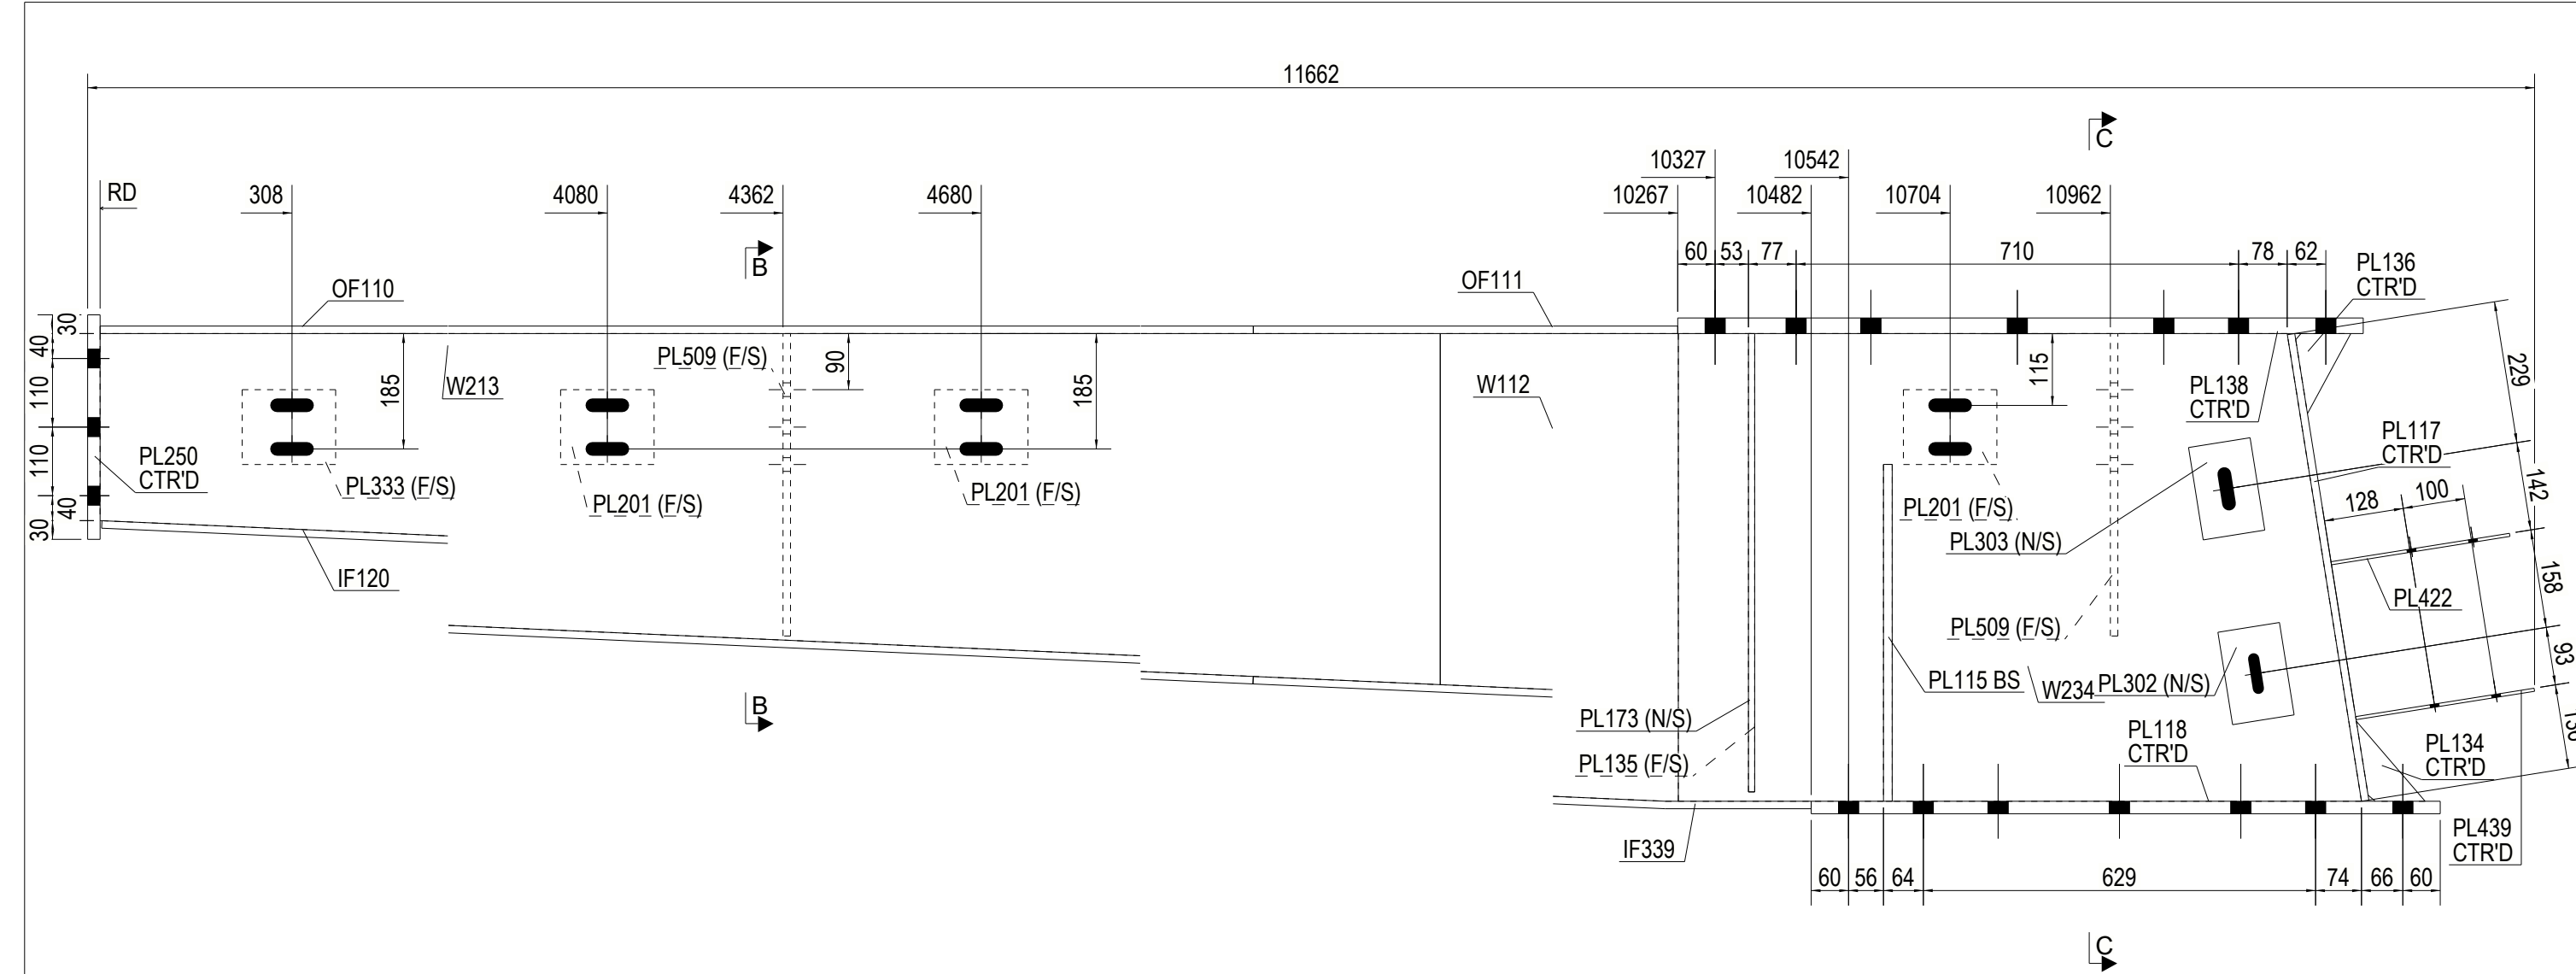

ASSEMBLY MARK	ITEM NO.	DESCRIPTION	LENGTH	MATERIAL	QTY.	UNIT WT. IN Kgs	WT./ITEM IN Kgs	TOTAL WT. IN Kgs	GRAND TOTAL WT.	ITEM TYPE
	IF120	PL12*350	5692	S355JR	1	7.85	187.68	187.68		
	IF339	PL12*350	4796	S355JR	1	7.85	158.13	158.13		
	OF110	PL12*350	5690	S355JR	1	7.85	187.60	187.60		
	OF111	PL12*350	4577	S355JR	1	7.85	150.92	150.92		
	PL115	PLT14*190	540	S355JR	2	7.85	11.28	22.56		
	PL117	PL12*350	758	S355JR	1	7.85	24.98	24.98		
	PL118	PL20*400	1009	S355JR	1	7.85	63.39	63.39		
	PL134	PLT14*110.4	128	S355JR	1	7.85	0.63	0.63		
	PL135	PLT10*172.5	735	S355JR	1	7.85	9.95	9.95		
	PL136	PLT14*88.4	128	S355JR	1	7.85	0.63	0.63		
	PL138	PL25*350	1100	S355JR	1	7.85	75.56	75.56		
	PL173	PLT10*177.5	735	S355JR	1	7.85	10.24	10.24		
	PL201	PL6*120	150	S355JR	3	7.85	0.85	2.54		
	PL250	PL20*350	360	S355JR	1	7.85	19.78	19.78		
	PL302	PL6*100	150	S355JR	1	7.85	0.71	0.71		
	PL303	PL6*100	150	S355JR	1	7.85	0.71	0.71		
	PL333	PL6*120	150	S355JR	1	7.85	0.85	0.85		
	PL422	PL5*100	290	S355JR	1	7.85	1.14	1.14		
	PL439	PL5*100	290	S355JR	1	7.85	1.14	1.14		
	PL509	PL12*130	485	S355JR	2	7.85	5.94	11.88		
	W112	PLT6*750	4278	S355JR	1	7.85	132.39	132.39		
	W213	PLT6*563	5990	S355JR	1	7.85	121.74	121.74		
	W234	PLT12*750	1096	S355JR	1	7.85	73.24	73.24		
TOTAL IN Kgs.								1258.37	125***	LIGHT STEEL

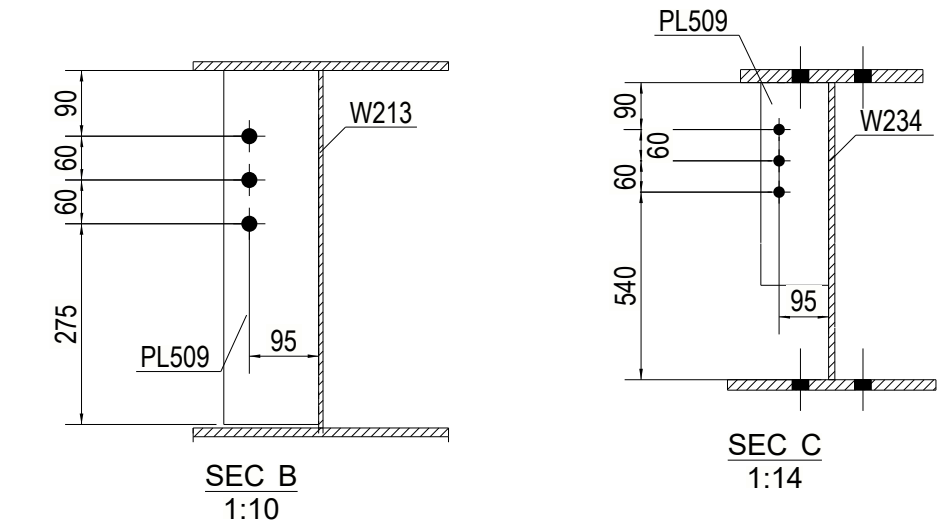

QTY= 1 Nos. COLUMN MKD : C90

REV.	DATE	DESCRIPTION	DRW	CHK	APP
ELNAGAR					
DRAWN			DATE		
CHECKED			SCALE	1:10	
REVIEWED			REL. NO.		
ASSEMBLY MARK			SHT. NO.	REV. NO.	

Tekla structures

C90 x 1