


Tekla structures

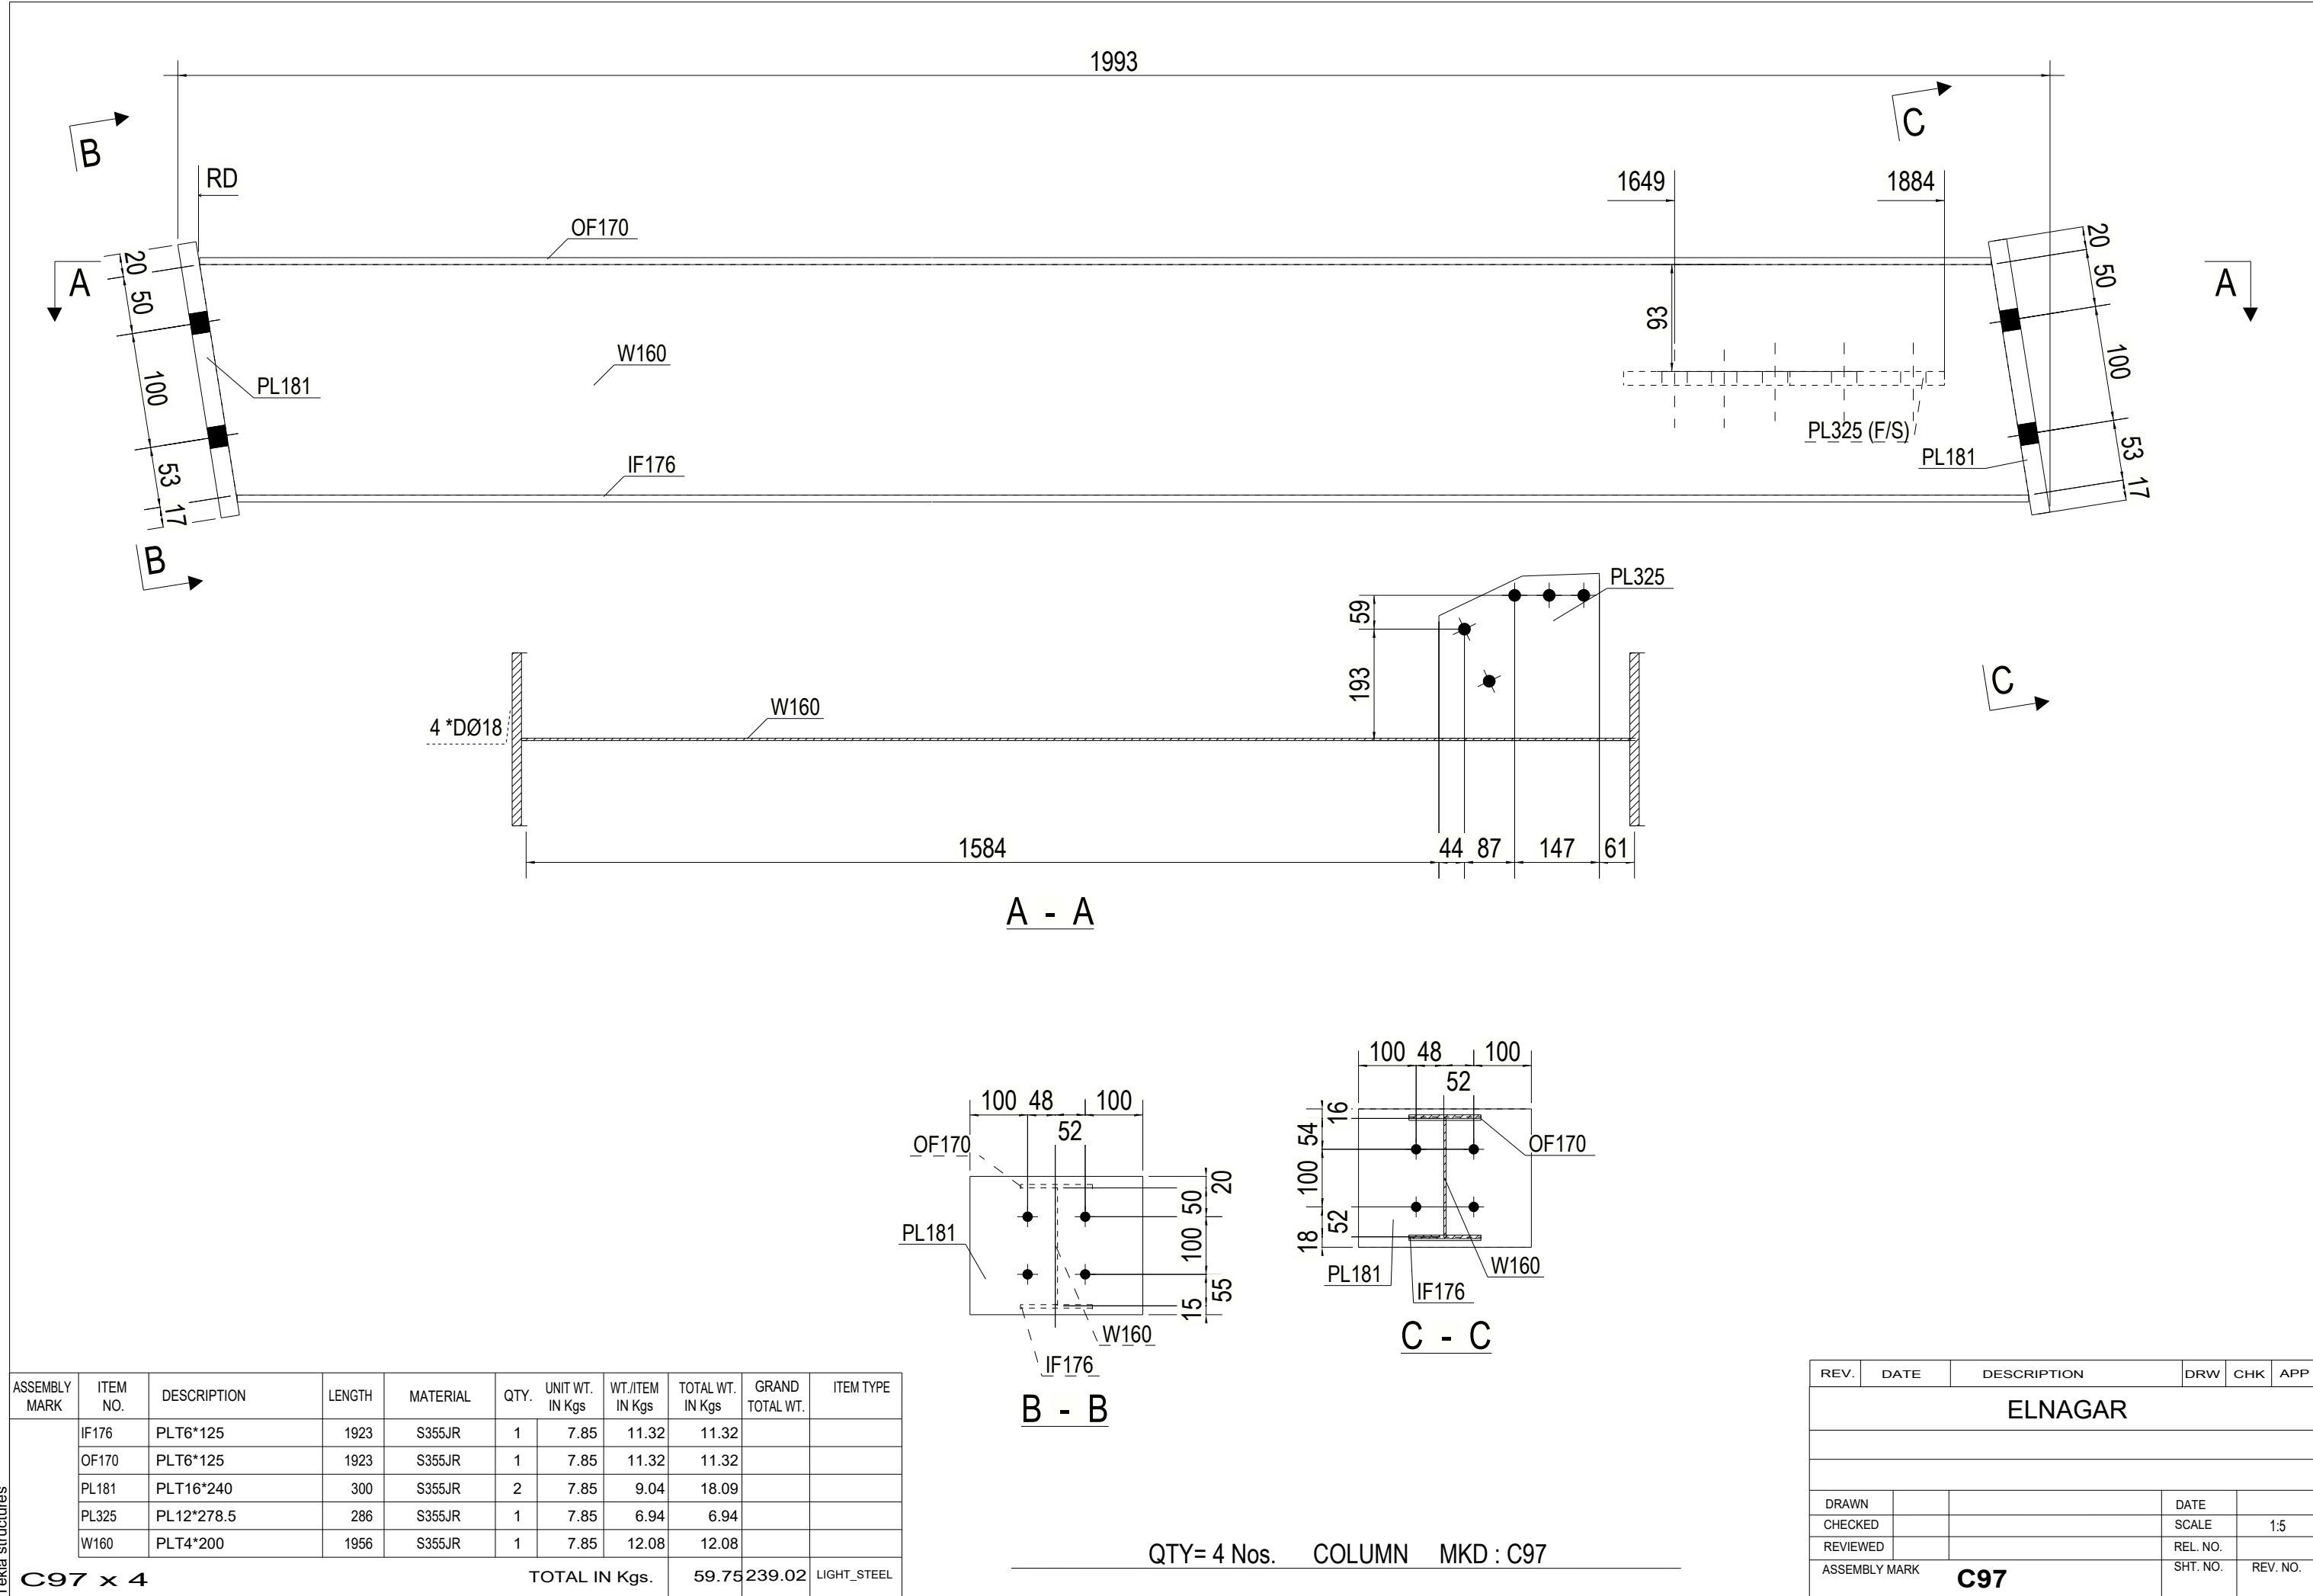

REV.	DATE	DESCRIPTION	DRW	CHK	APP
ELNAGAR					
DRAWN			DATE		
CHECKED			SCALE		1:5
REVIEWED			REL. NO.		
ASSEMBLY MARK			SHT. NO.		REV. NO.
C97					