
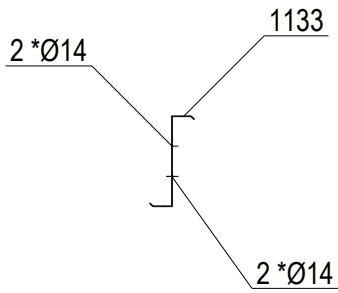


Tekla structures

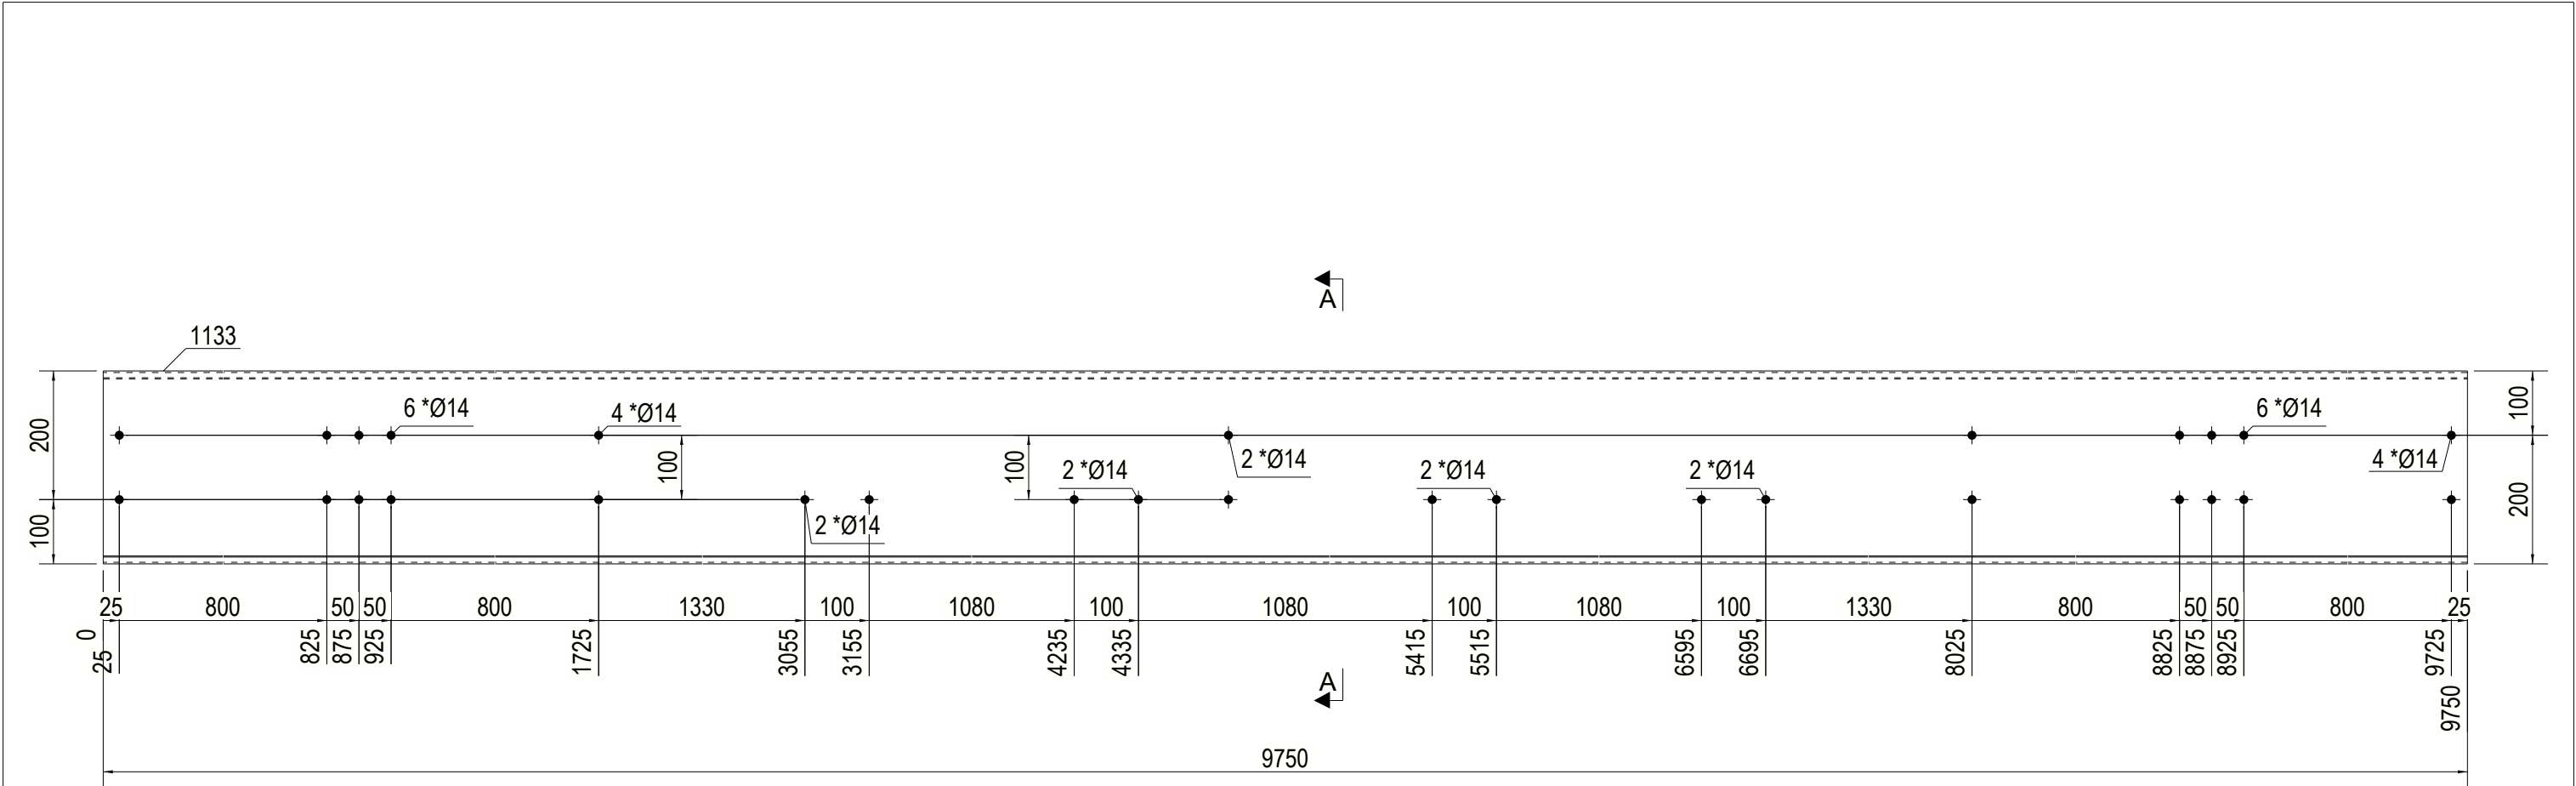

SEC A
1:25

ASSEMBLY MARK	ITEM NO.	DESCRIPTION	LENGTH	MATERIAL	QTY.	UNIT WT. IN Kgs	WT./ITEM IN Kgs	TOTAL WT. IN Kgs	GRAND TOTAL WT.	ITEM TYPE
	1133	Z300-65-15-2.5	9750	S355JR	1	0.00	86.67	86.67		
P30 x 2				TOTAL IN Kgs.			86.67	173.33		LIGHT_STEEL

QTY= 2 Nos. GUSSET PLATE MKD : P30

REV.	DATE	DESCRIPTION	DRW	CHK	APP
ELNAGAR					
DRAWN		DATE			
CHECKED		SCALE		1:10	
REVIEWED		REL. NO.			
ASSEMBLY MARK			SHT. NO.	REV. NO.	
P30					