
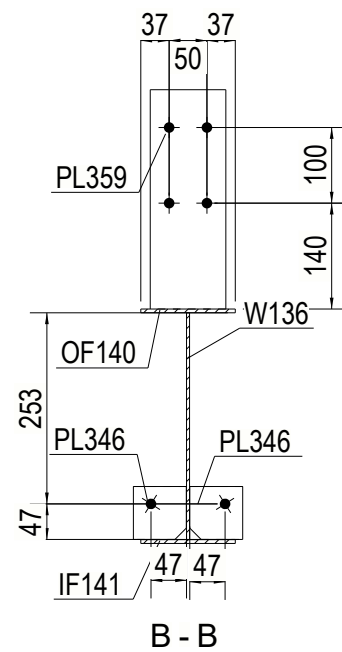


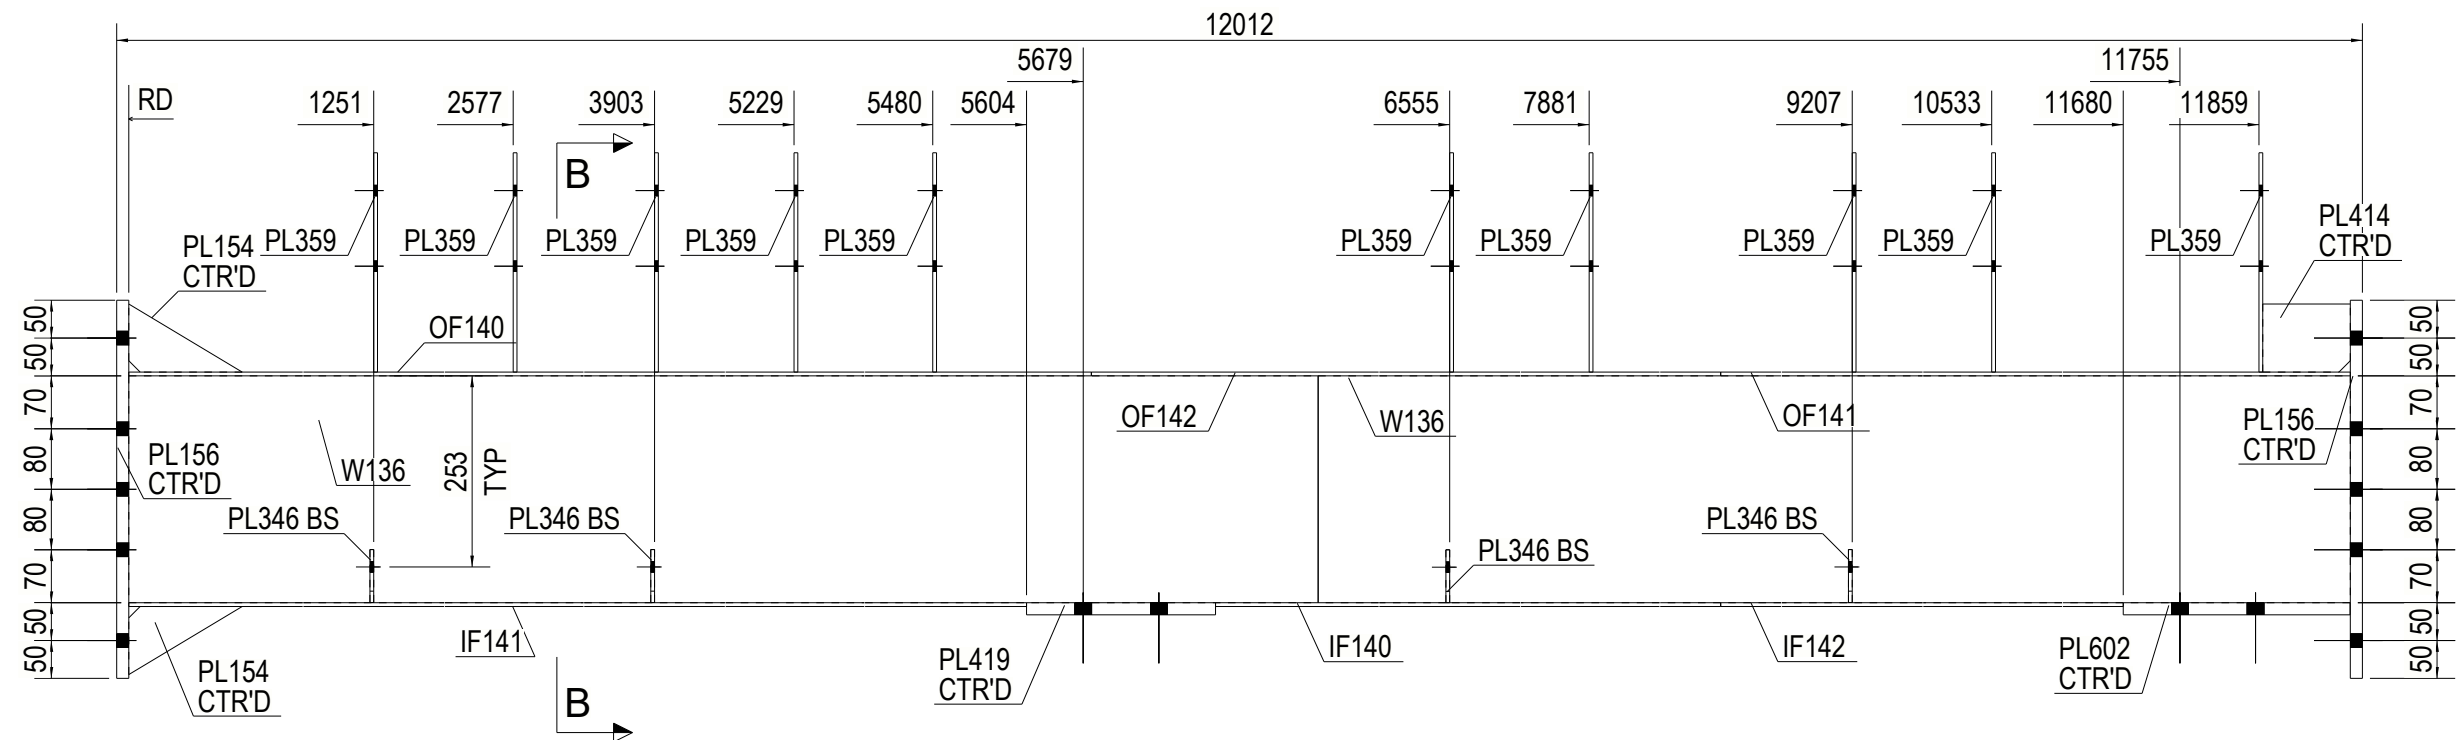

ASSEMBLY MARK	ITEM NO.	DESCRIPTION	LENGTH	MATERIAL	QTY.	UNIT WT. IN Kgs	WT./ITEM IN Kgs	TOTAL WT. IN Kgs	GRAND TOTAL WT.	ITEM TYPE
ekia Structures	IF140	PLT5*125	2836	S355JR	1	7.85	13.91	13.91		
	IF141	PLT5*125	5604	S355JR	1	7.85	27.50	27.50		
	IF142	PLT5*125	2990	S355JR	1	7.85	14.67	14.67		
	OF140	PLT5*125	5690	S355JR	1	7.85	27.92	27.92		
	OF141	PLT5*125	3290	S355JR	1	7.85	16.14	16.14		
	OF142	PLT5*125	3000	S355JR	1	7.85	14.72	14.72		
	PL154	PL8*90	150	S355JR	2	7.85	0.42	0.83		
	PL156	PLT16*200	500	S355JR	2	7.85	12.56	25.12		
	PL346	PL5*70	70	S355JR	8	7.85	0.19	1.50		
	PL359	PL5*100	290	S355JR	10	7.85	1.14	11.38		
	PL414	PL8*90	116	S355JR	1	7.85	0.65	0.65		
	PL419	PLT16*250	440	S355JR	1	7.85	13.82	13.82		
	PL602	PLT16*300	440	S355JR	1	7.85	16.58	16.58		
	W136	PLT4*300	5990	S355JR	2	7.85	56.43	112.85		
	TOTAL IN Kgs.							297.59	297.59	LIGHT_STEEL

QTY= 1 Nos. RAFTER MKD : RF15

REV.	DATE	DESCRIPTION	DRW	CHK	APP
ELNAGAR					
DRAWN			DATE		
CHECKED			SCALE	1:10	
REVIEWED			REL. NO.		
ASSEMBLY MARK			SHT. NO.	REL. NO.	
RF15					