


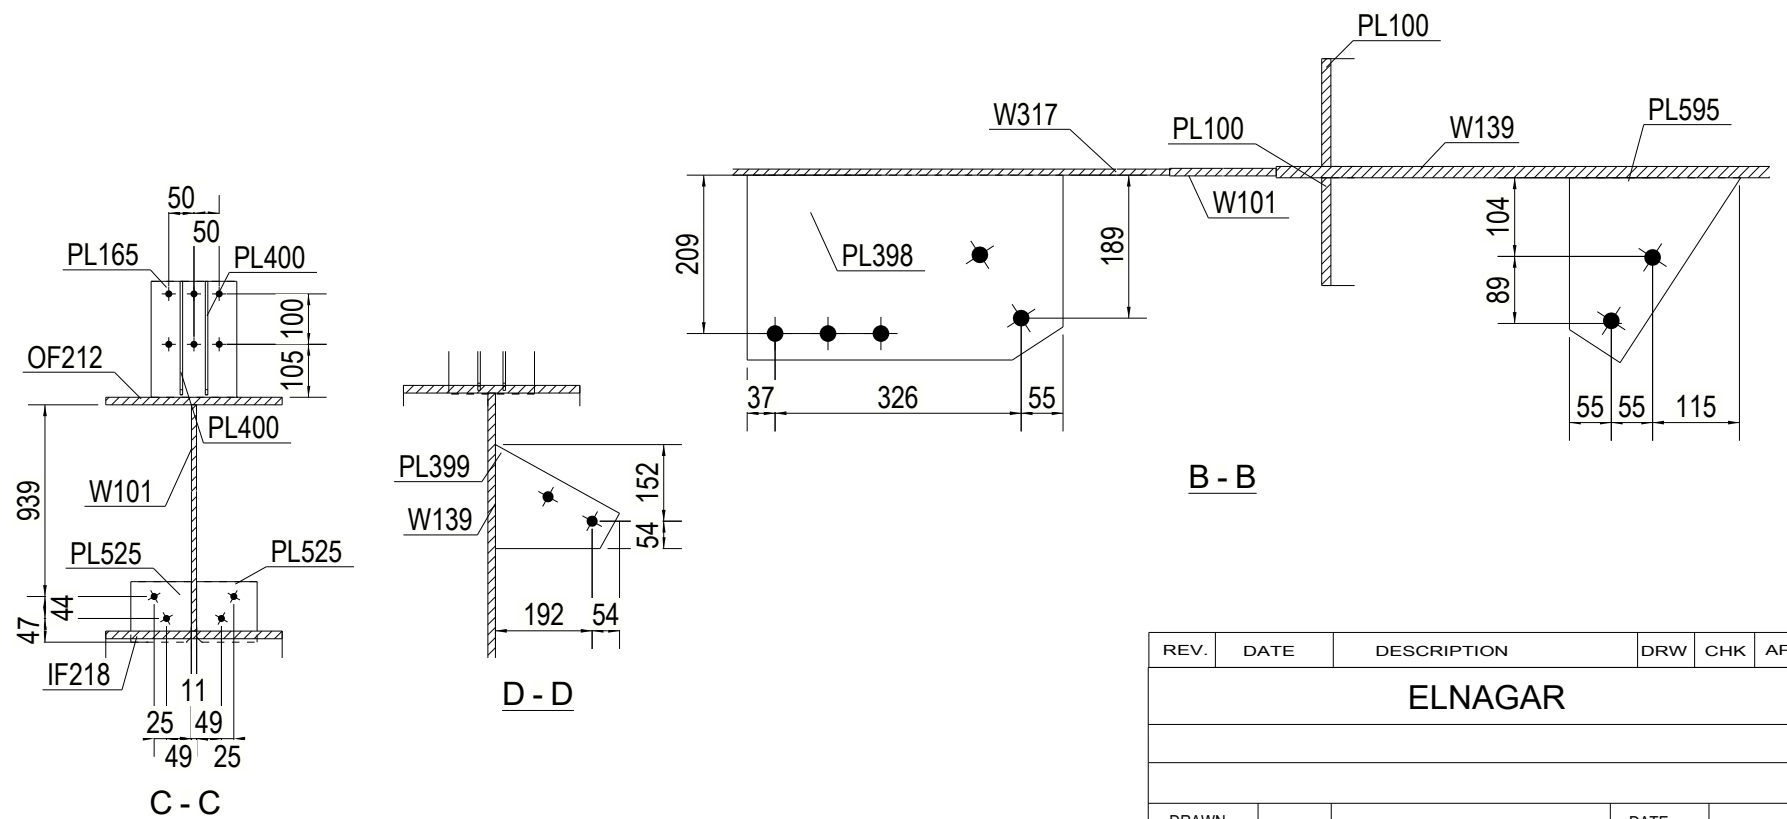

QTY= 1 Nos. RAFTER MKD : RF22

Tekla structures