



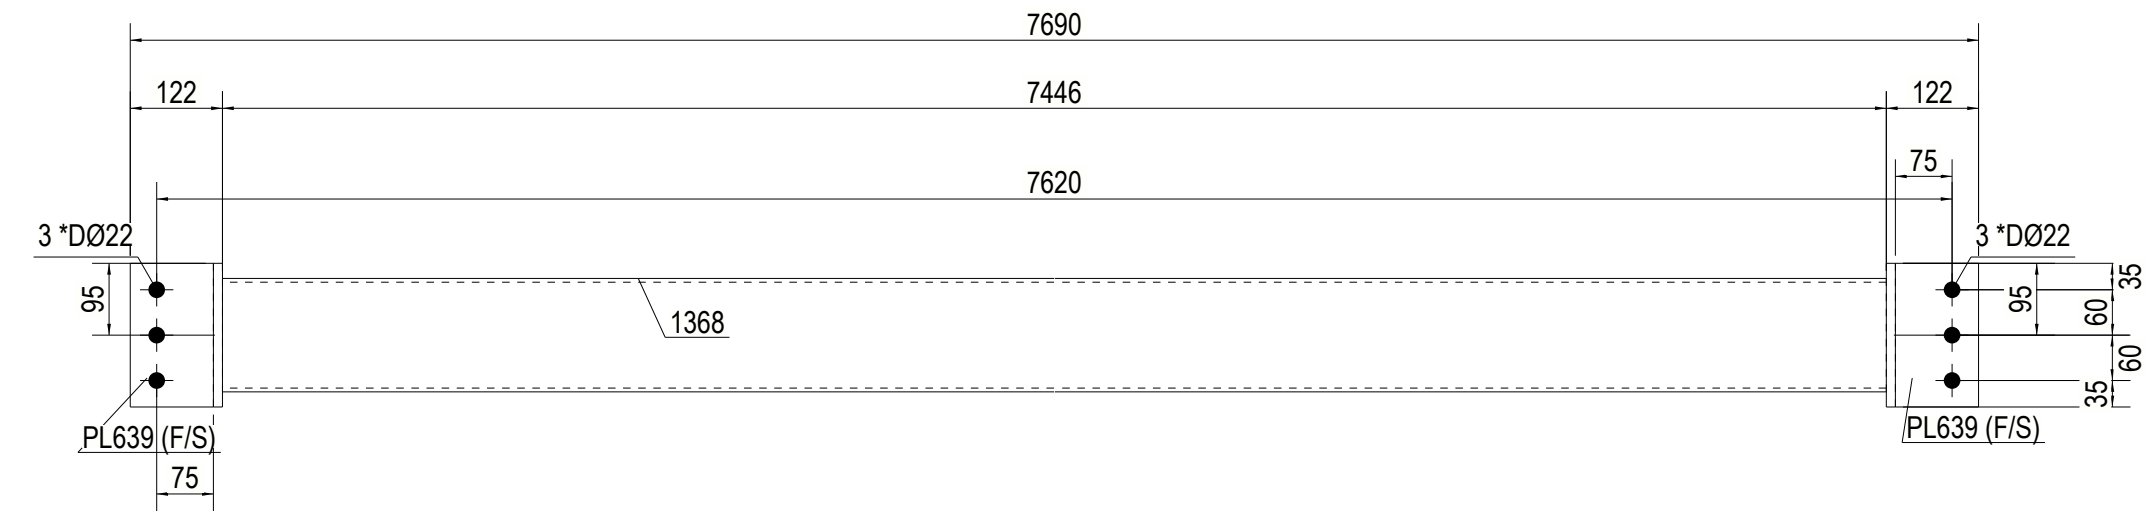

FRONT VIEW

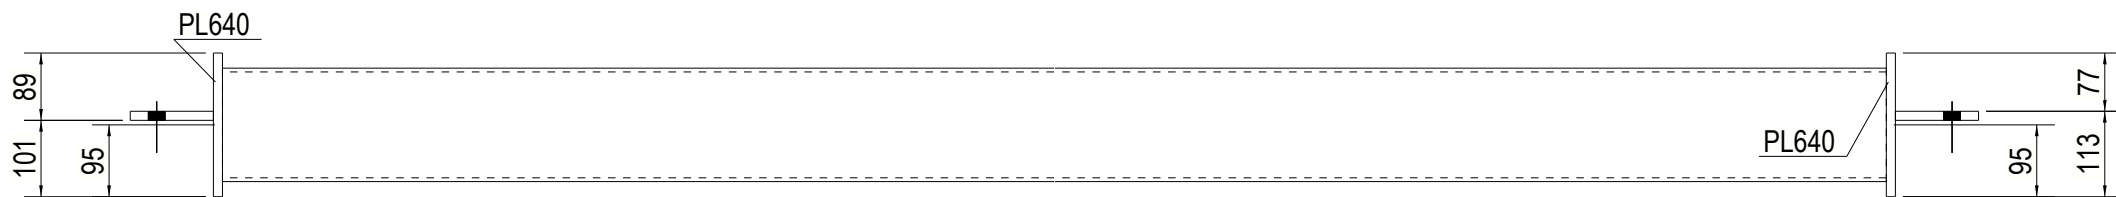

TOP VIEW

ASSEMBLY MARK	ITEM NO.	DESCRIPTION	LENGTH	MATERIAL	QTY.	UNIT WT. IN Kgs	WT./ITEM IN Kgs	TOTAL WT. IN Kgs	GRAND TOTAL WT.	ITEM TYPE
rebar structures	1368	SHS150*150*5.0	7446	S355JR	1	22.60	169.51	169.51		
	PL639	PL12*110	190	S275	2	7.85	1.97	3.94		
	PL640	PL12*190	190	S275	2	7.85	3.40	6.80		
	ST18 x 2							TOTAL IN Kgs.	180.25	360.50

QTY= 2 Nos. BRACING MKD : ST18

REV.	DATE	DESCRIPTION	DRW	CHK	APP
ELNAGAR					
DRAWN			DATE		
CHECKED			SCALE	1:10	
REVIEWED			REL. NO.		
ASSEMBLY MARK				SHT. NO.	REV. NO.
ST18					