


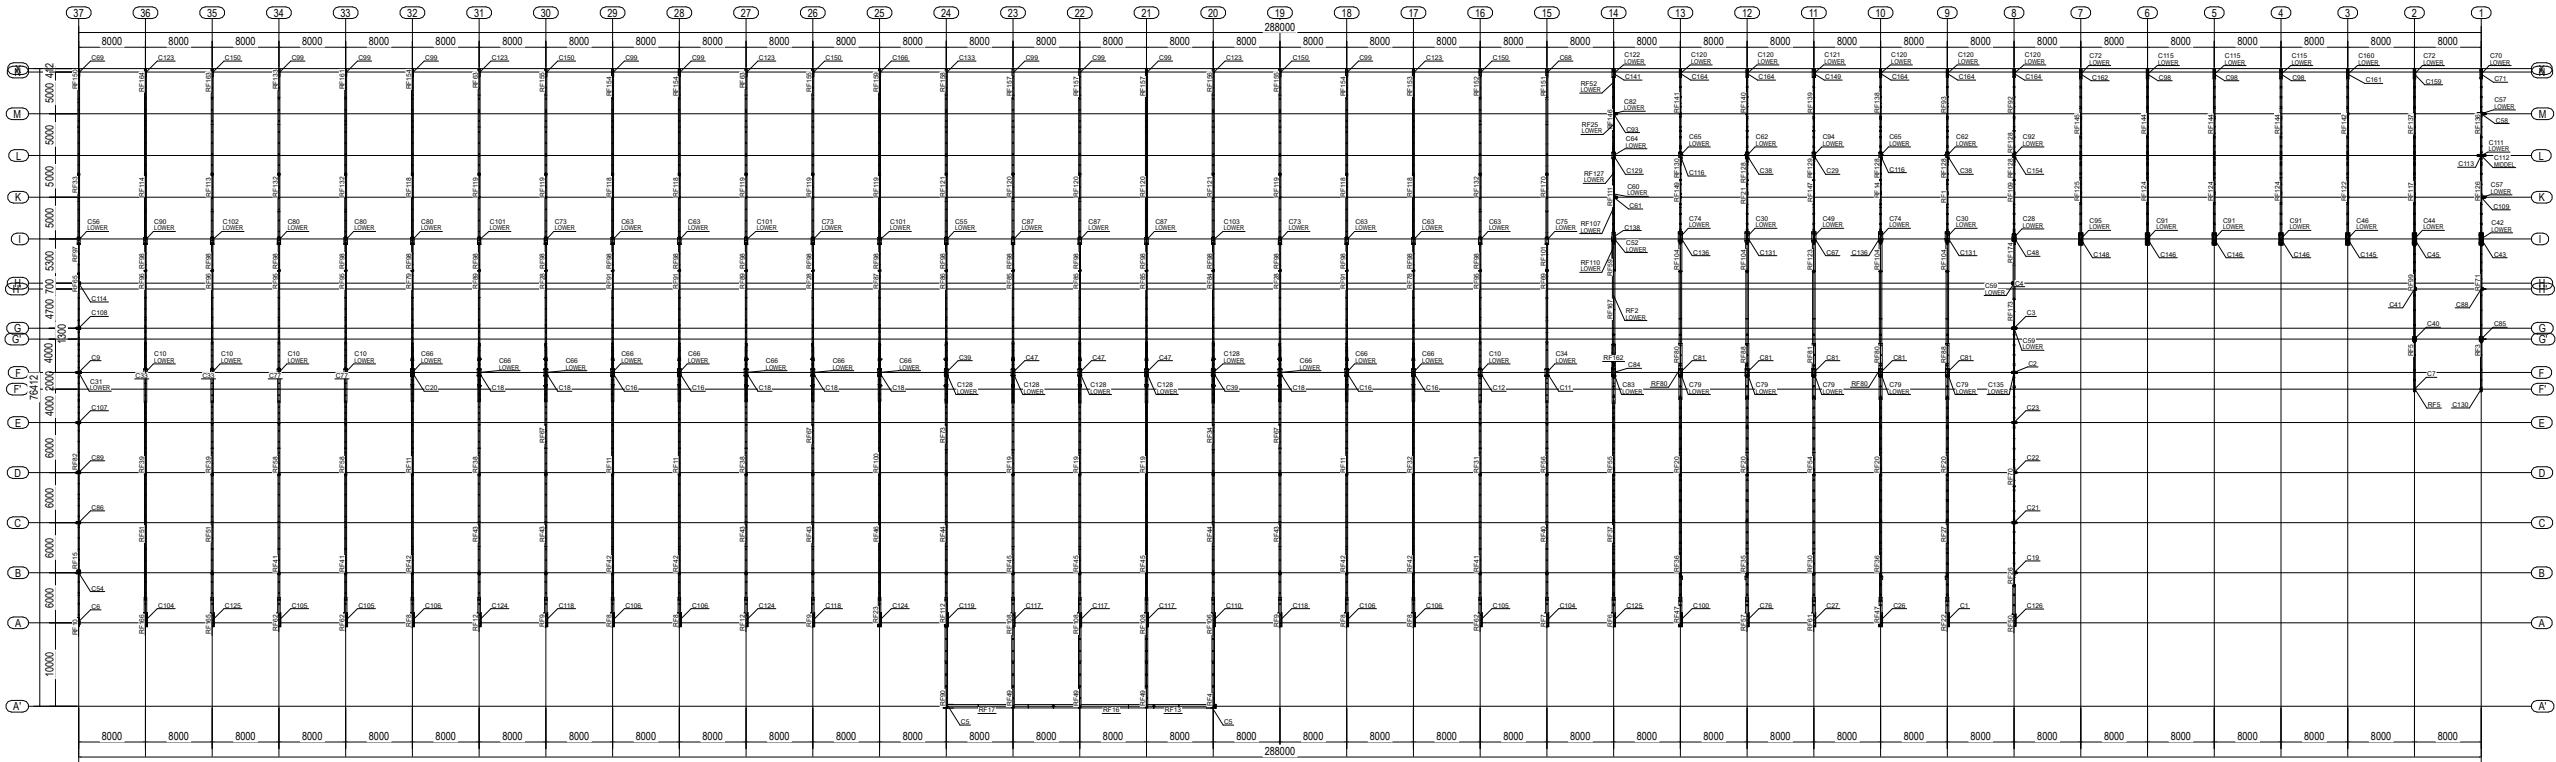

PART MARK KEY PLAN

00	28.04.2028	ISSUED FOR CONSTRUCTION	ZAC	-	ZAC	-	
REV	DATE	DESCRIPTION	DRN	DSN	CHK	APR	
PROJECT :							
LOCATION :		JORDAN					
CLIENT :							
CONSULTANT :		M/s.: -----					
STEEL CONTRACTOR :							
		الدعائم هياكل معدنية SSS SUPPORTS STEEL STRUCTURES					
DRAWING TITLE:		PART MARK KEY PLAN					
SSS JOB NO. :		R02				DRG NO.: E01	