



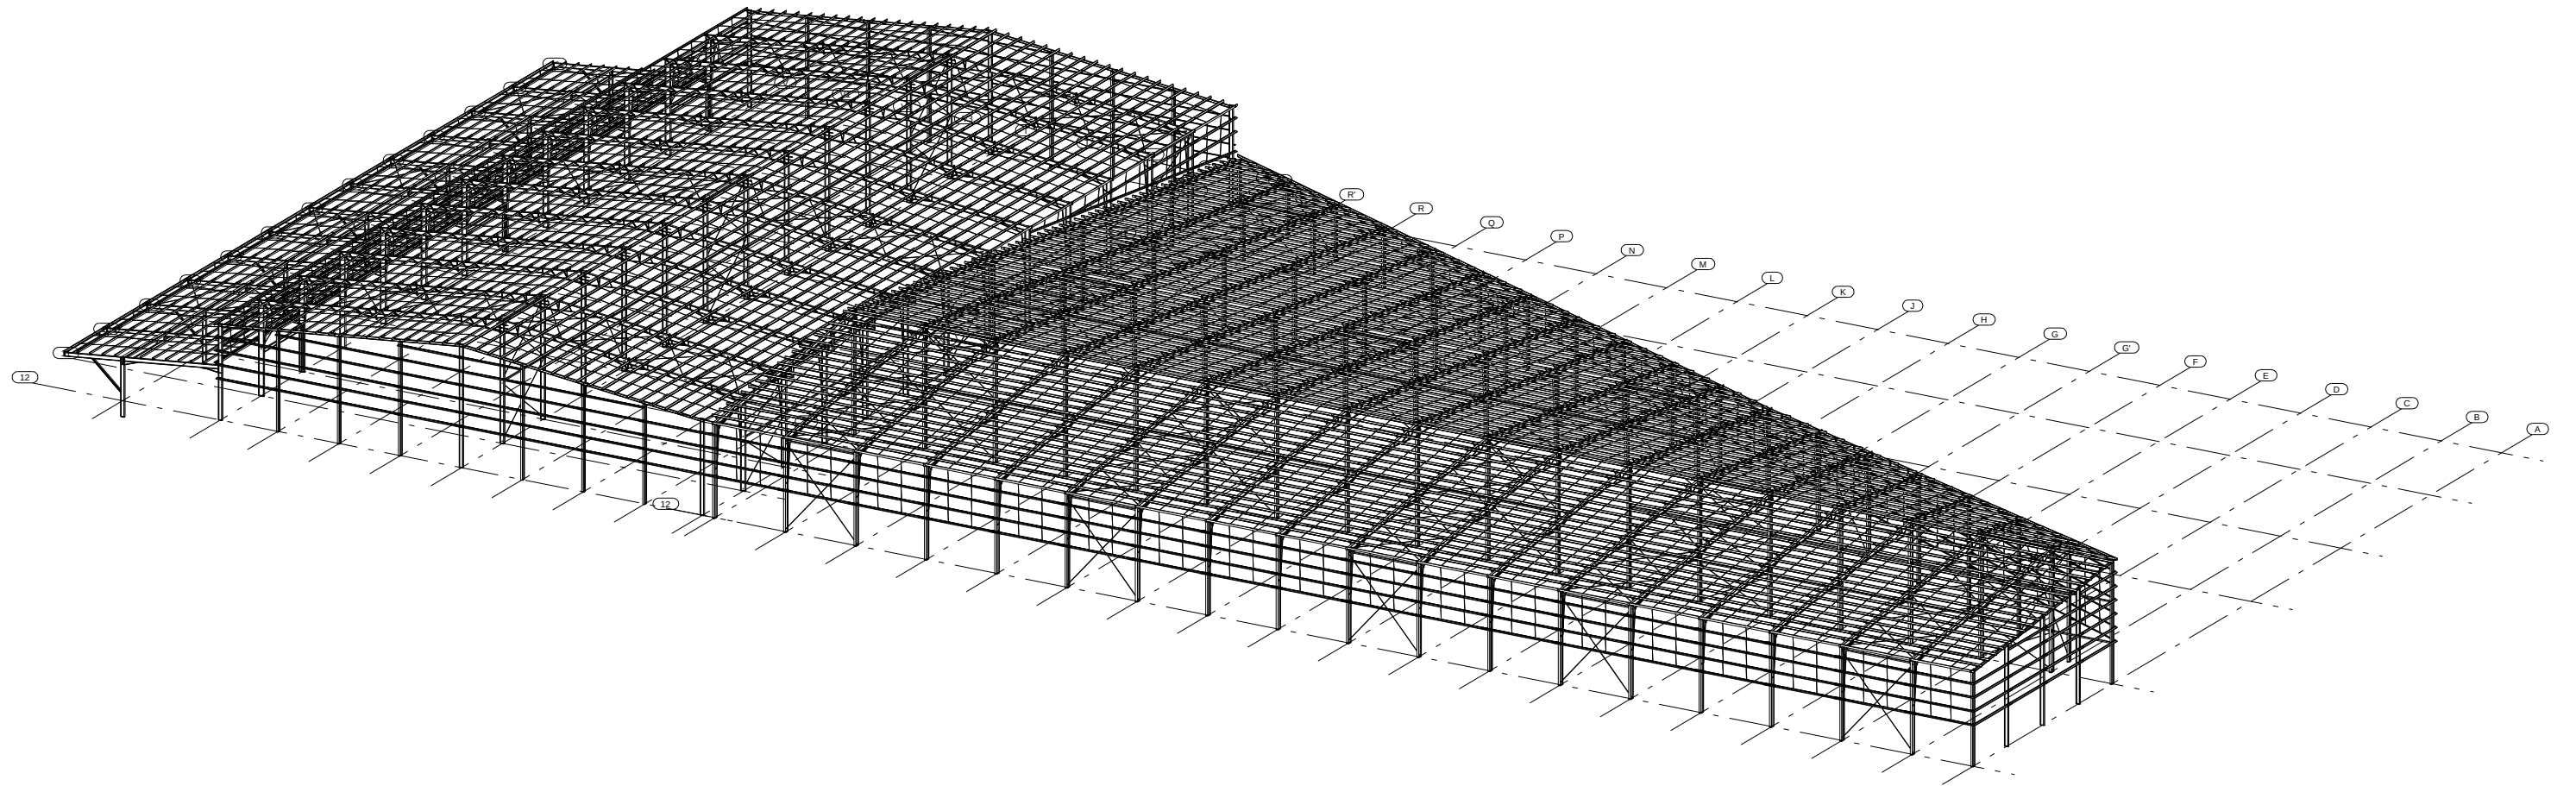


3D MODEL

12-08-2020		ISSUED FOR FABRICATION		A.A.	H.H.		
REV.	DATE	DESCRIPTION		DRN	CHK		
.....							
PROJECT NAME:							
SCHOOL PROJECT							
CONTRACTOR:							
--							
DRAWING TITLE:							
STEEL STRUCTURE							
3D_MODEL							
CHECKED BY		A.A.	SCALE				
DATE		A.A.	SHEET NO.		E01		

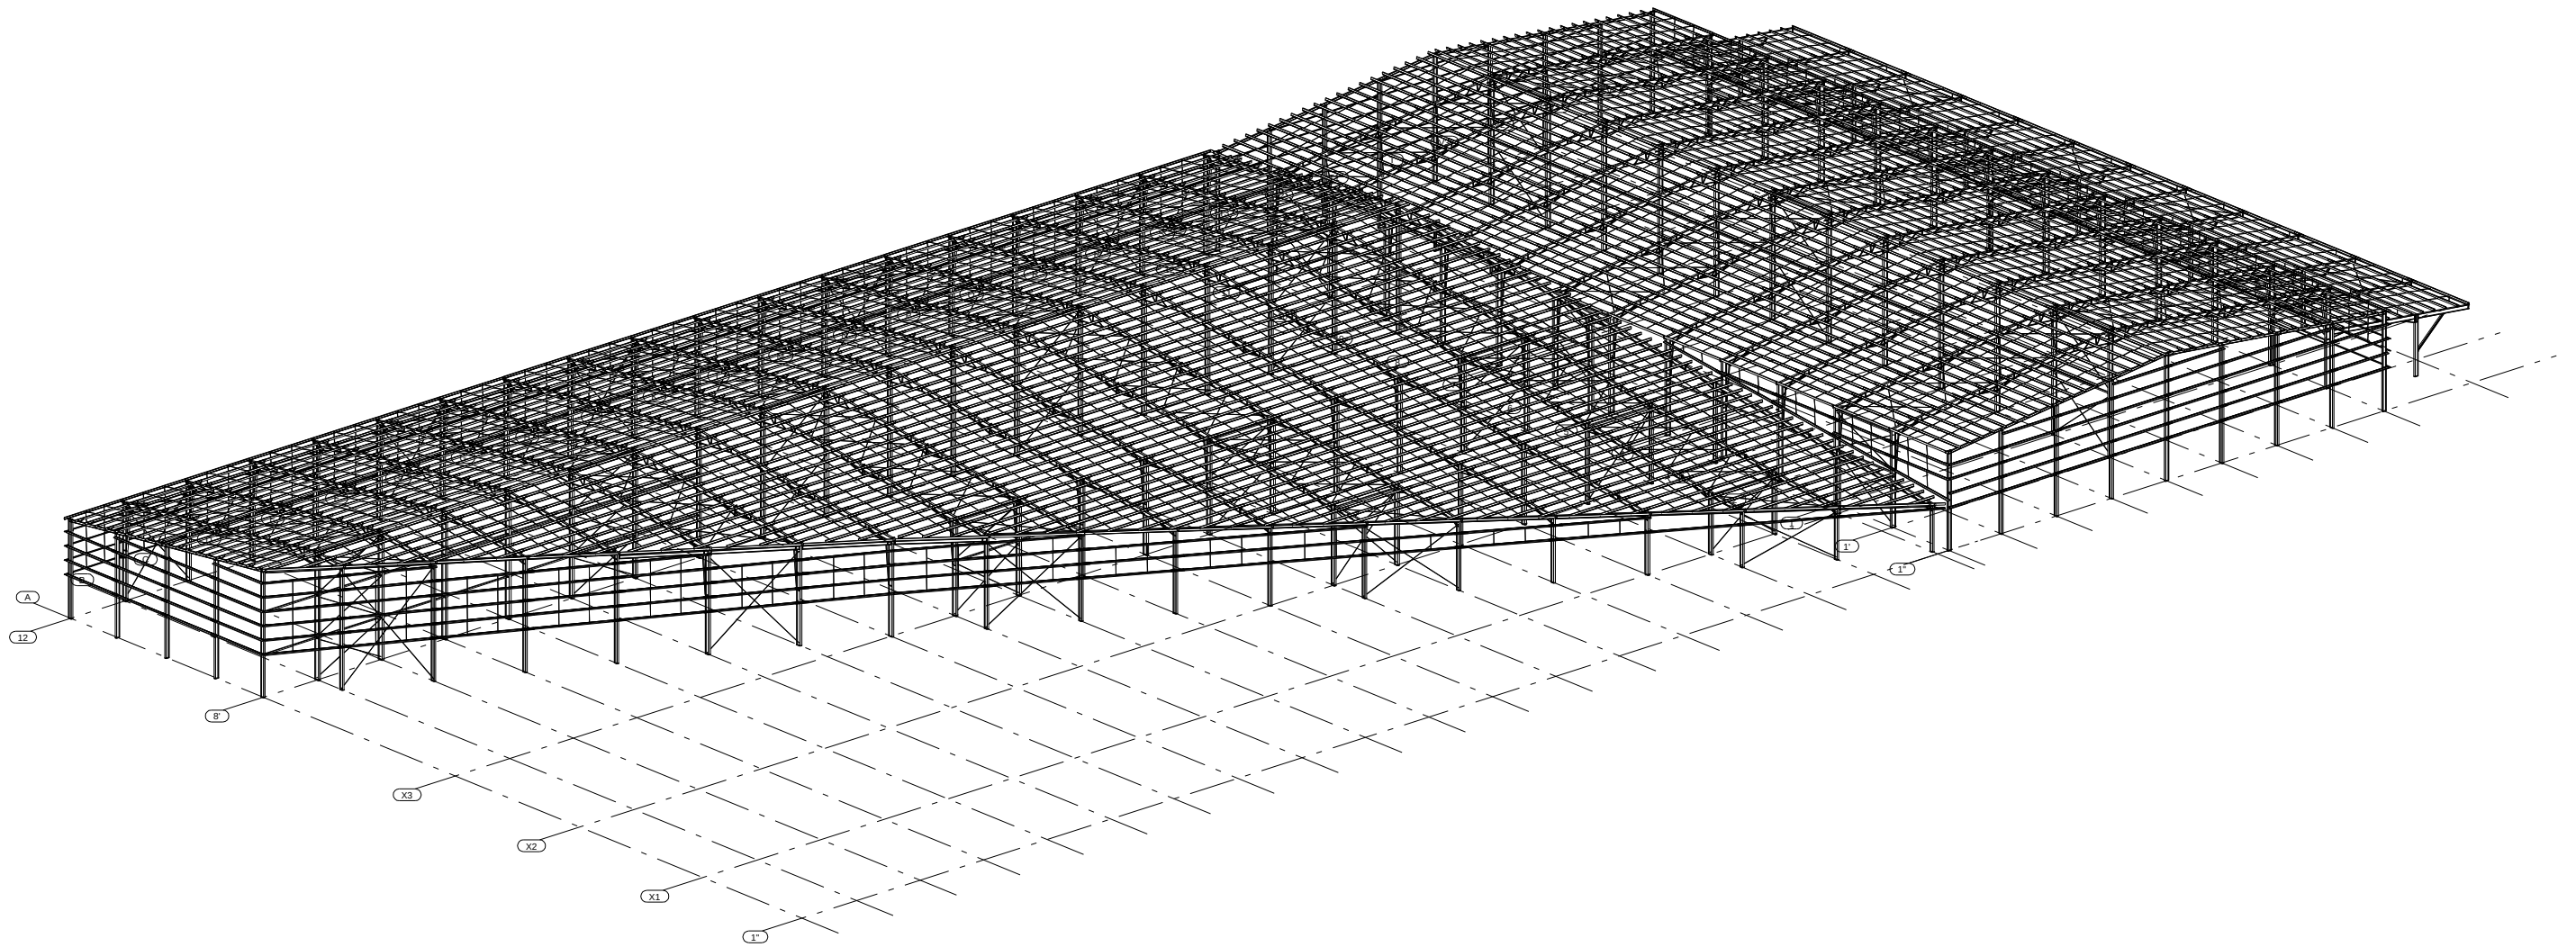


3D

12-08-2024		ISSUED FOR FABRICATION		A.A.	H.H.		
REV.	DATE	DESCRIPTION		DRN	CHK		
.....							
PROJECT NAME:							
SCHOOL PROJECT							
CONTRACTOR:							
--							
DRAWING TITLE:							
STEEL STRUCTURE							
3D_MODEL							
CHECKED BY		A.A.	SCALE				
DATE	A.A.		SHEET NO.		E02		

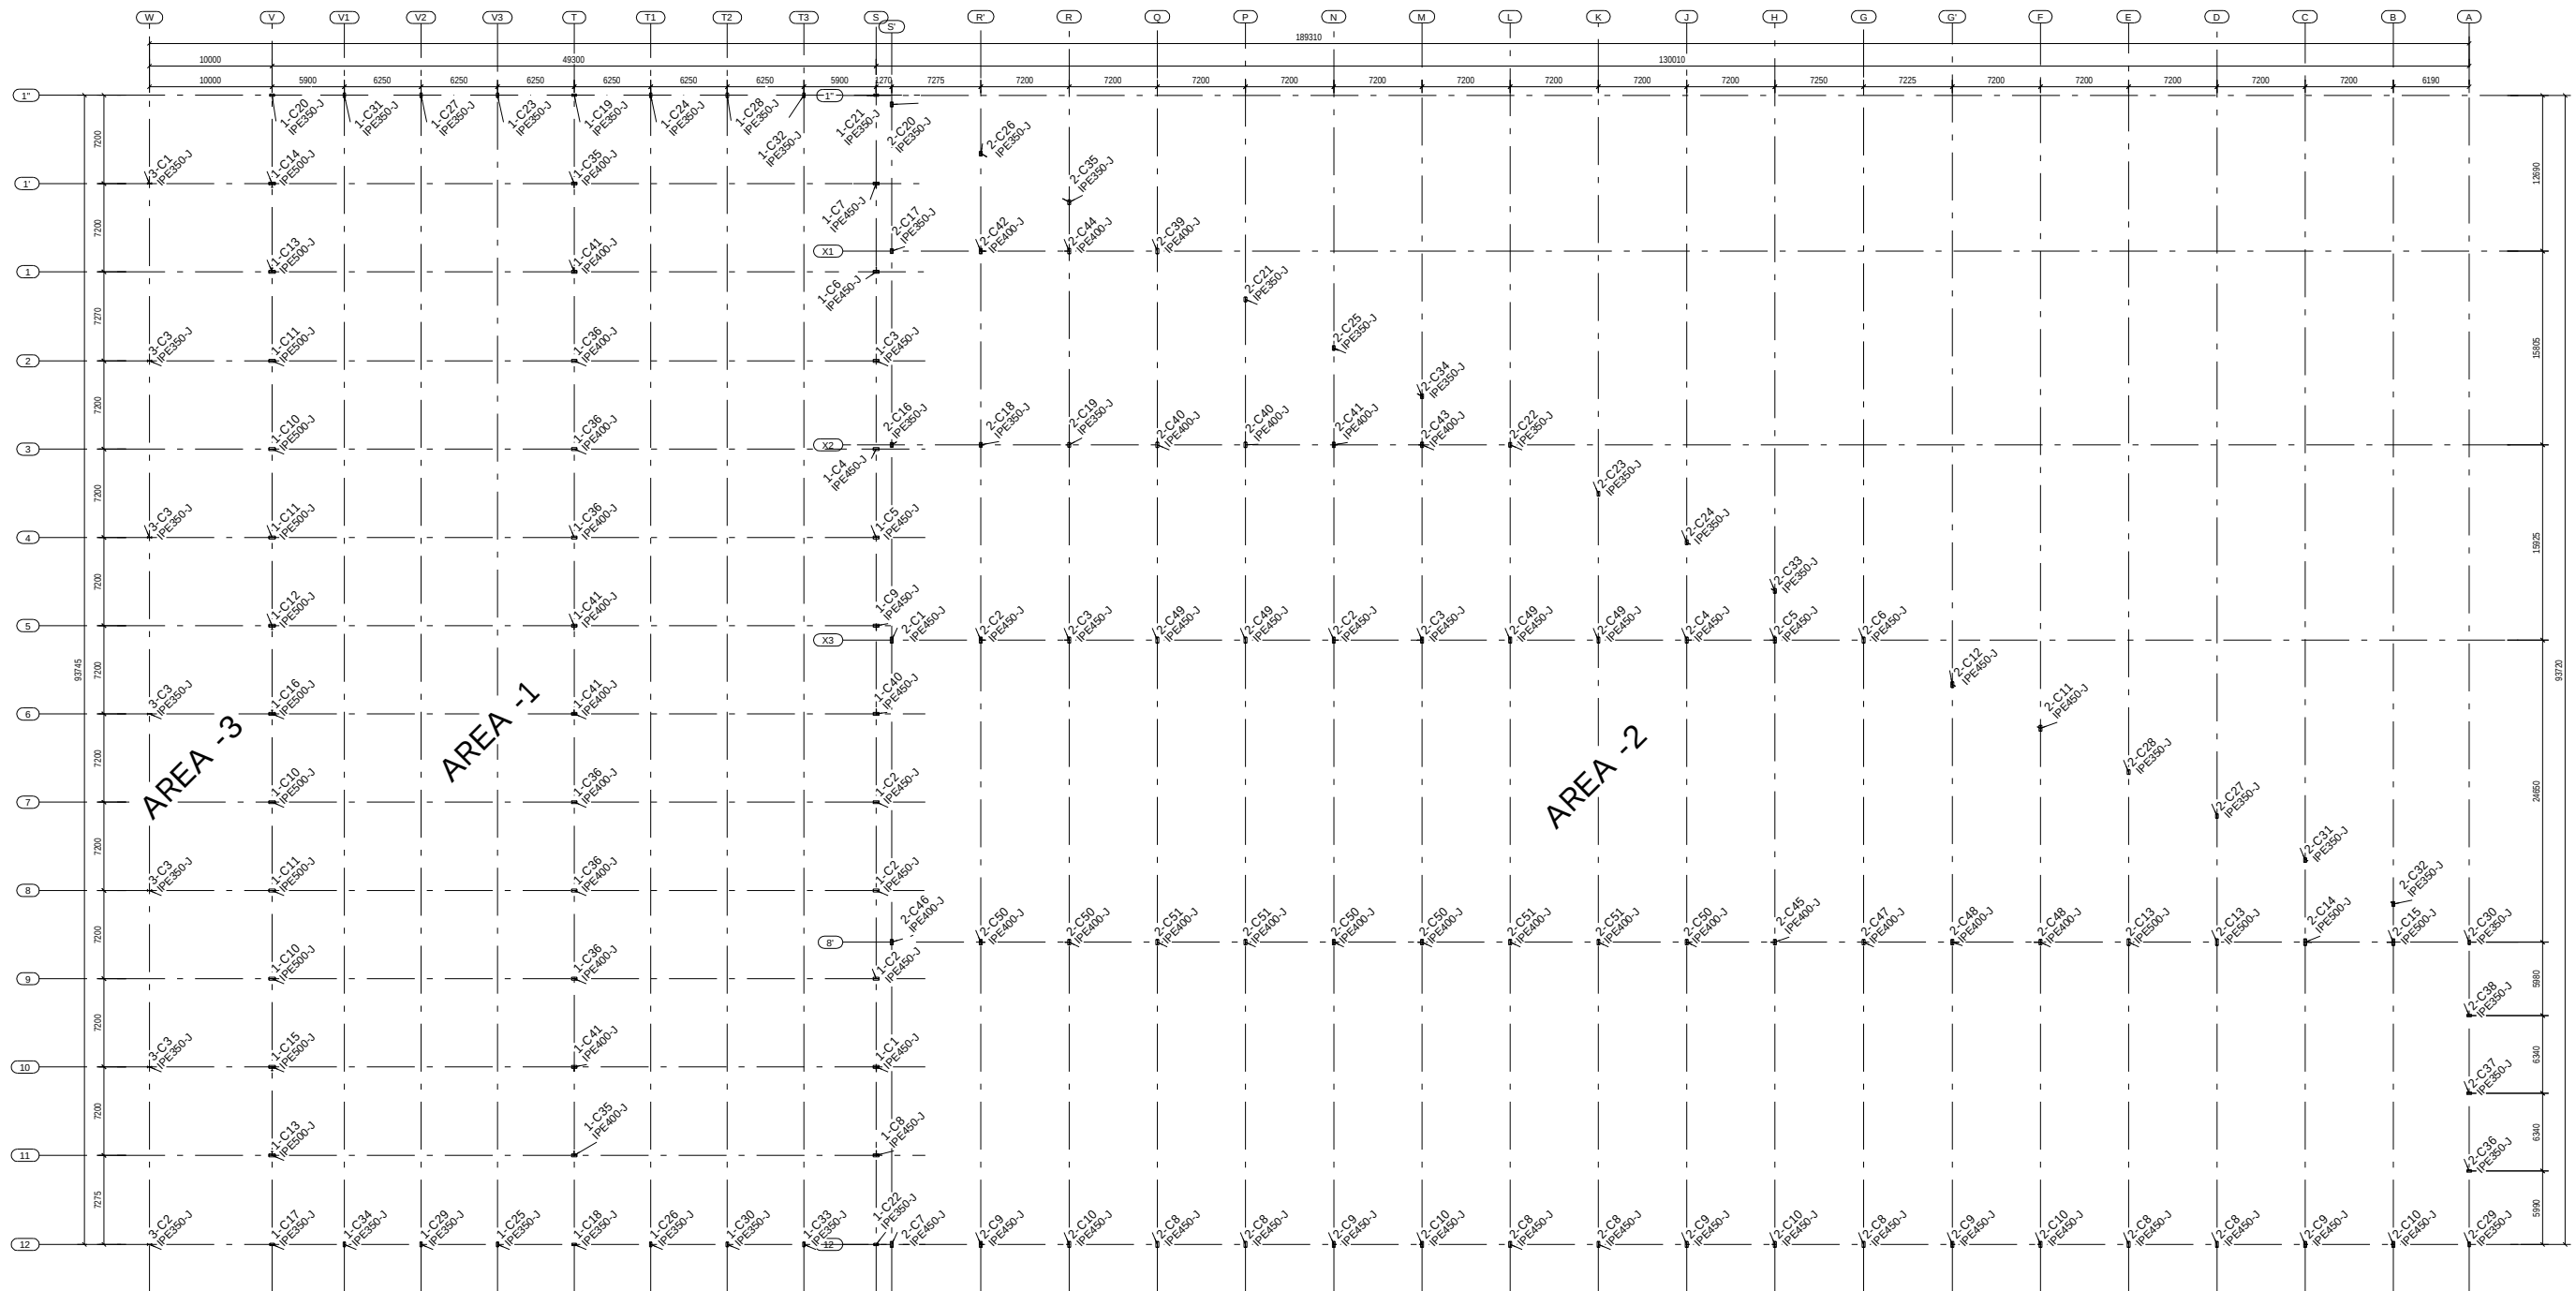


PLAN @EL+0.00

		12-08-2024	ISSUED FOR FABRICATION		A.A.	H.H.	
REV.	DATE	DESCRIPTION		DRN	CHK	DSN	
.....							
PROJECT NAME:							
SCHOOL PROJECT							
CONTRACTOR:							
--							
DRAWING TITLE:							
STEEL STRUCTURE							
Anchor Bolts Plan & Details							
CHECKED BY		A.A.	SCALE				
DATE		A.A.	SHEET NO.	E03			

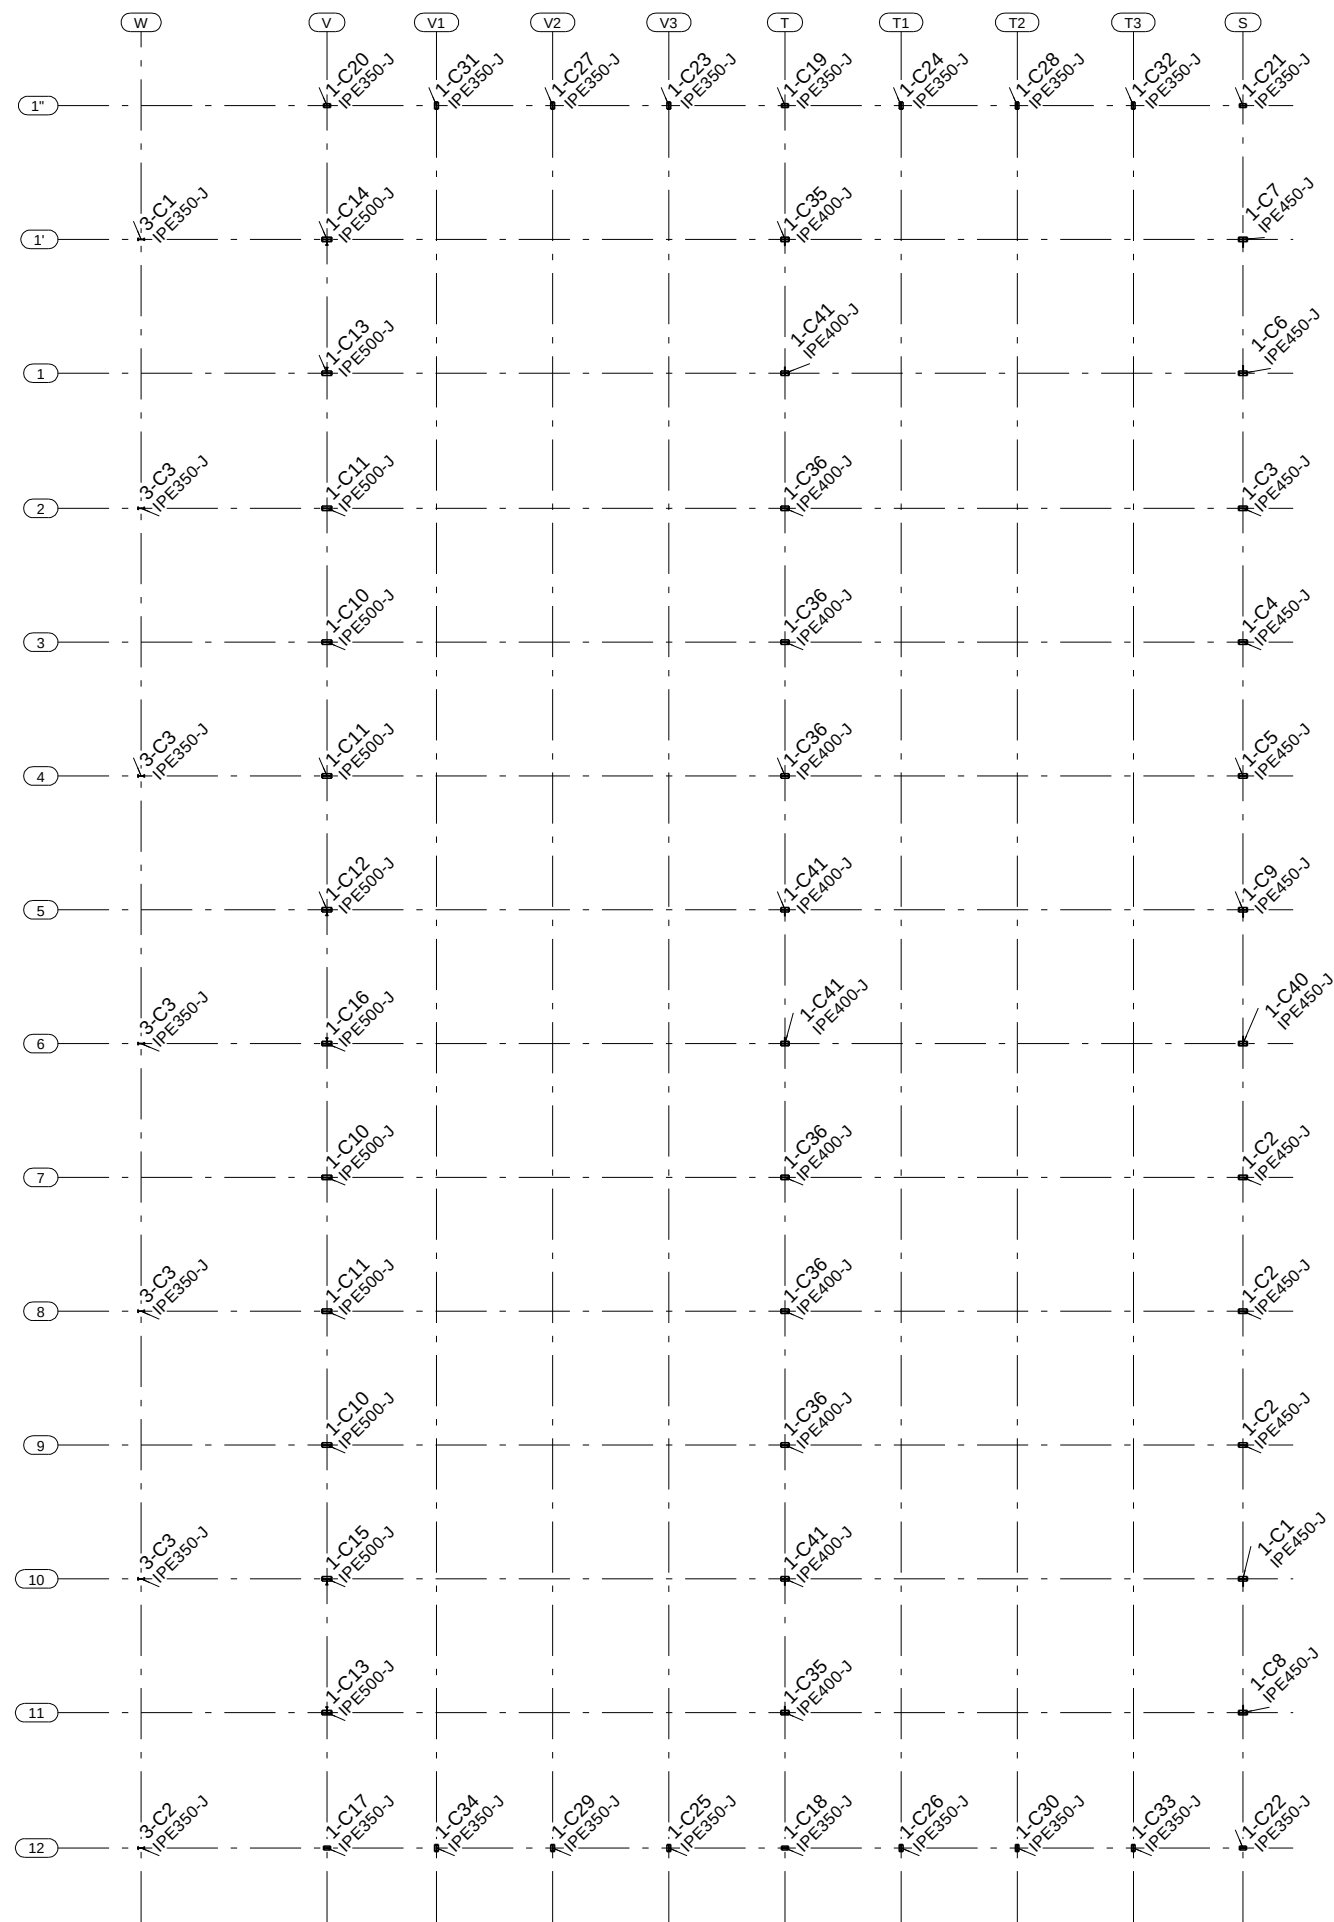

PLAN @EL+0.00
AREA -1 + AREA - 3

FD	12-06-2026	ISSUED FOR FABRICATION	A.A	H.H	
REV	DATE	DESCRIPTION	DRN	CHK	DSN
.....					
PROJECT NAME: SCHOOL PROJECT					
CONTRACTOR: --					
DRAWING TITLE: STEEL STRUCTURE Anchor Bolts Plan - Area - 1					
CHECKED BY	A.A	SCALE			
DATE	A.A	SHEET NO.	E04		

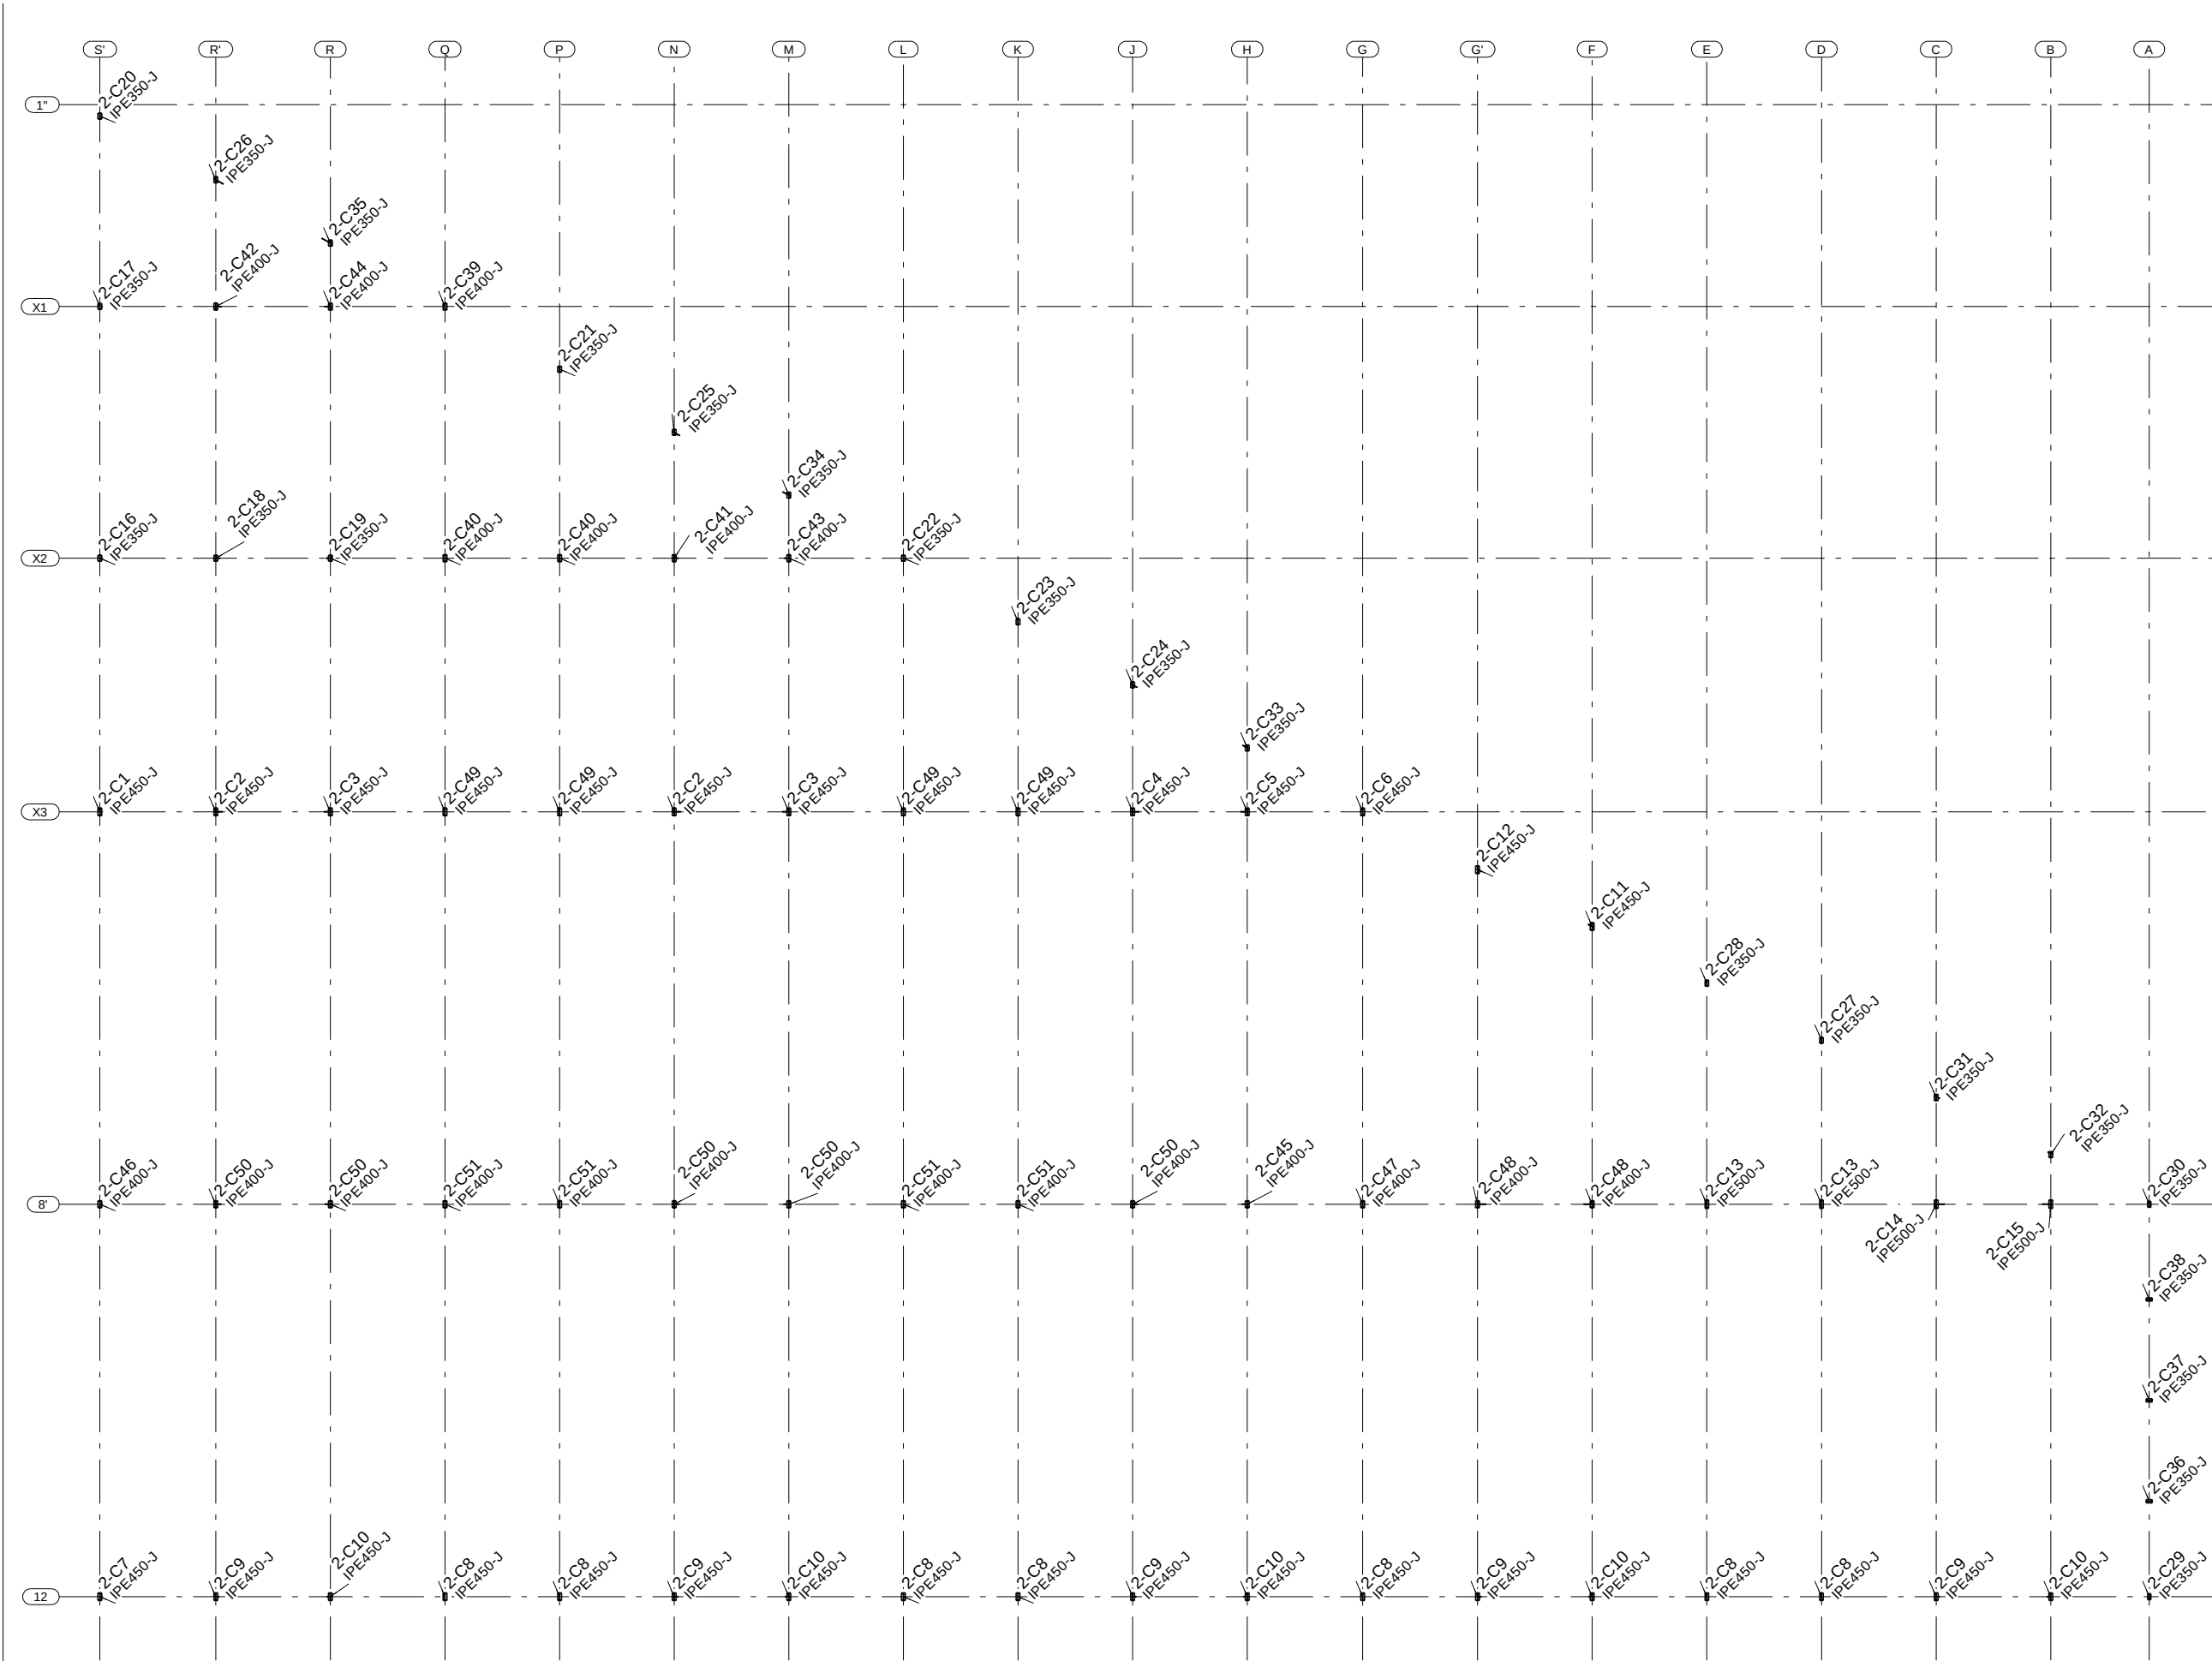


PLAN @EL+0.00


AREA -2

FD	12-06-2026	ISSUED FOR FABRICATION			A.A	H.H	
REV.	DATE	DESCRIPTION			DRN	CHK	DSN

PROJECT NAME:							
SCHOOL PROJECT							
CONTRACTOR:							
--							
DRAWING TITLE:							
STEEL STRUCTURE							
Anchor Bolts Plan - Area - 2							
CHECKED BY		A.A		SCALE			
DATE		A.A		SHEET NO.		E05	

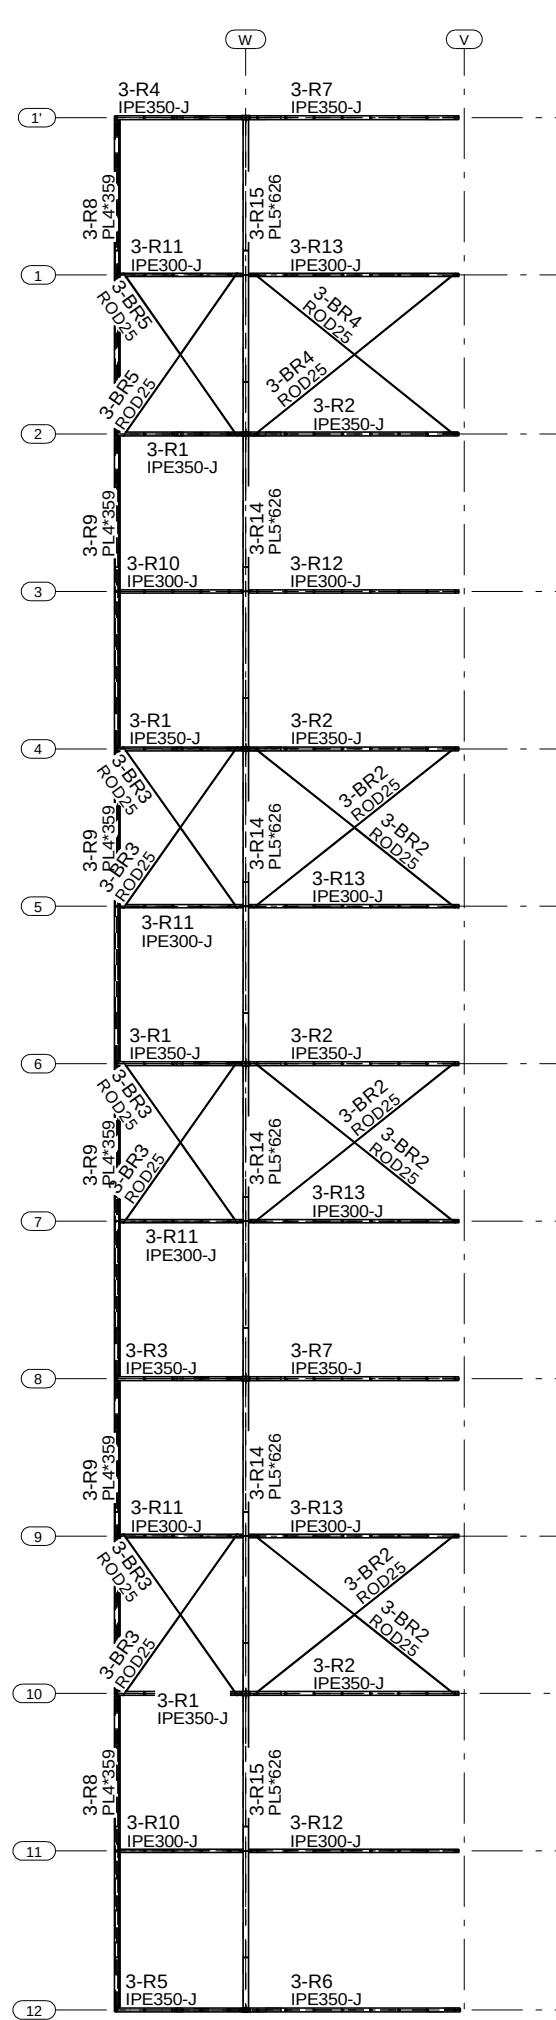

ROOF PLAN WITHOUT PURLIN

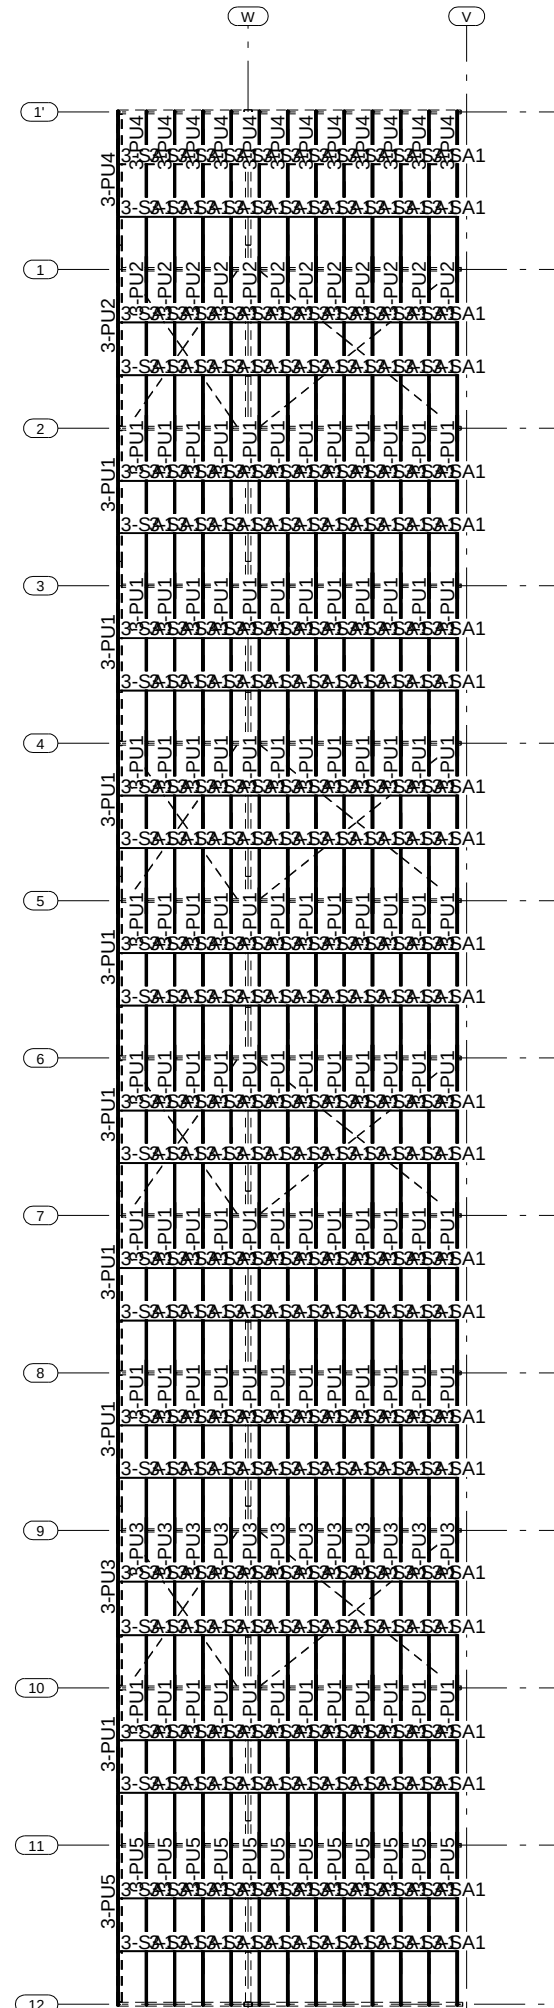


ROOF PLAN WITH PURLIN

AREA - 3


FD	12-06-2026	ISSUED FOR FABRICATION	A.A	H.H	
REV	DATE	DESCRIPTION	DRN	CHK	DSN
PROJECT NAME:					
SCHOOL PROJECT					
CONTRACTOR:					

DRAWING TITLE:					
STEEL STRUCTURE					
ROOF PLAN - Area - 1					
CHECKED BY	A.A	SCALE			
DATE	A.A	SHEET NO.	E06		

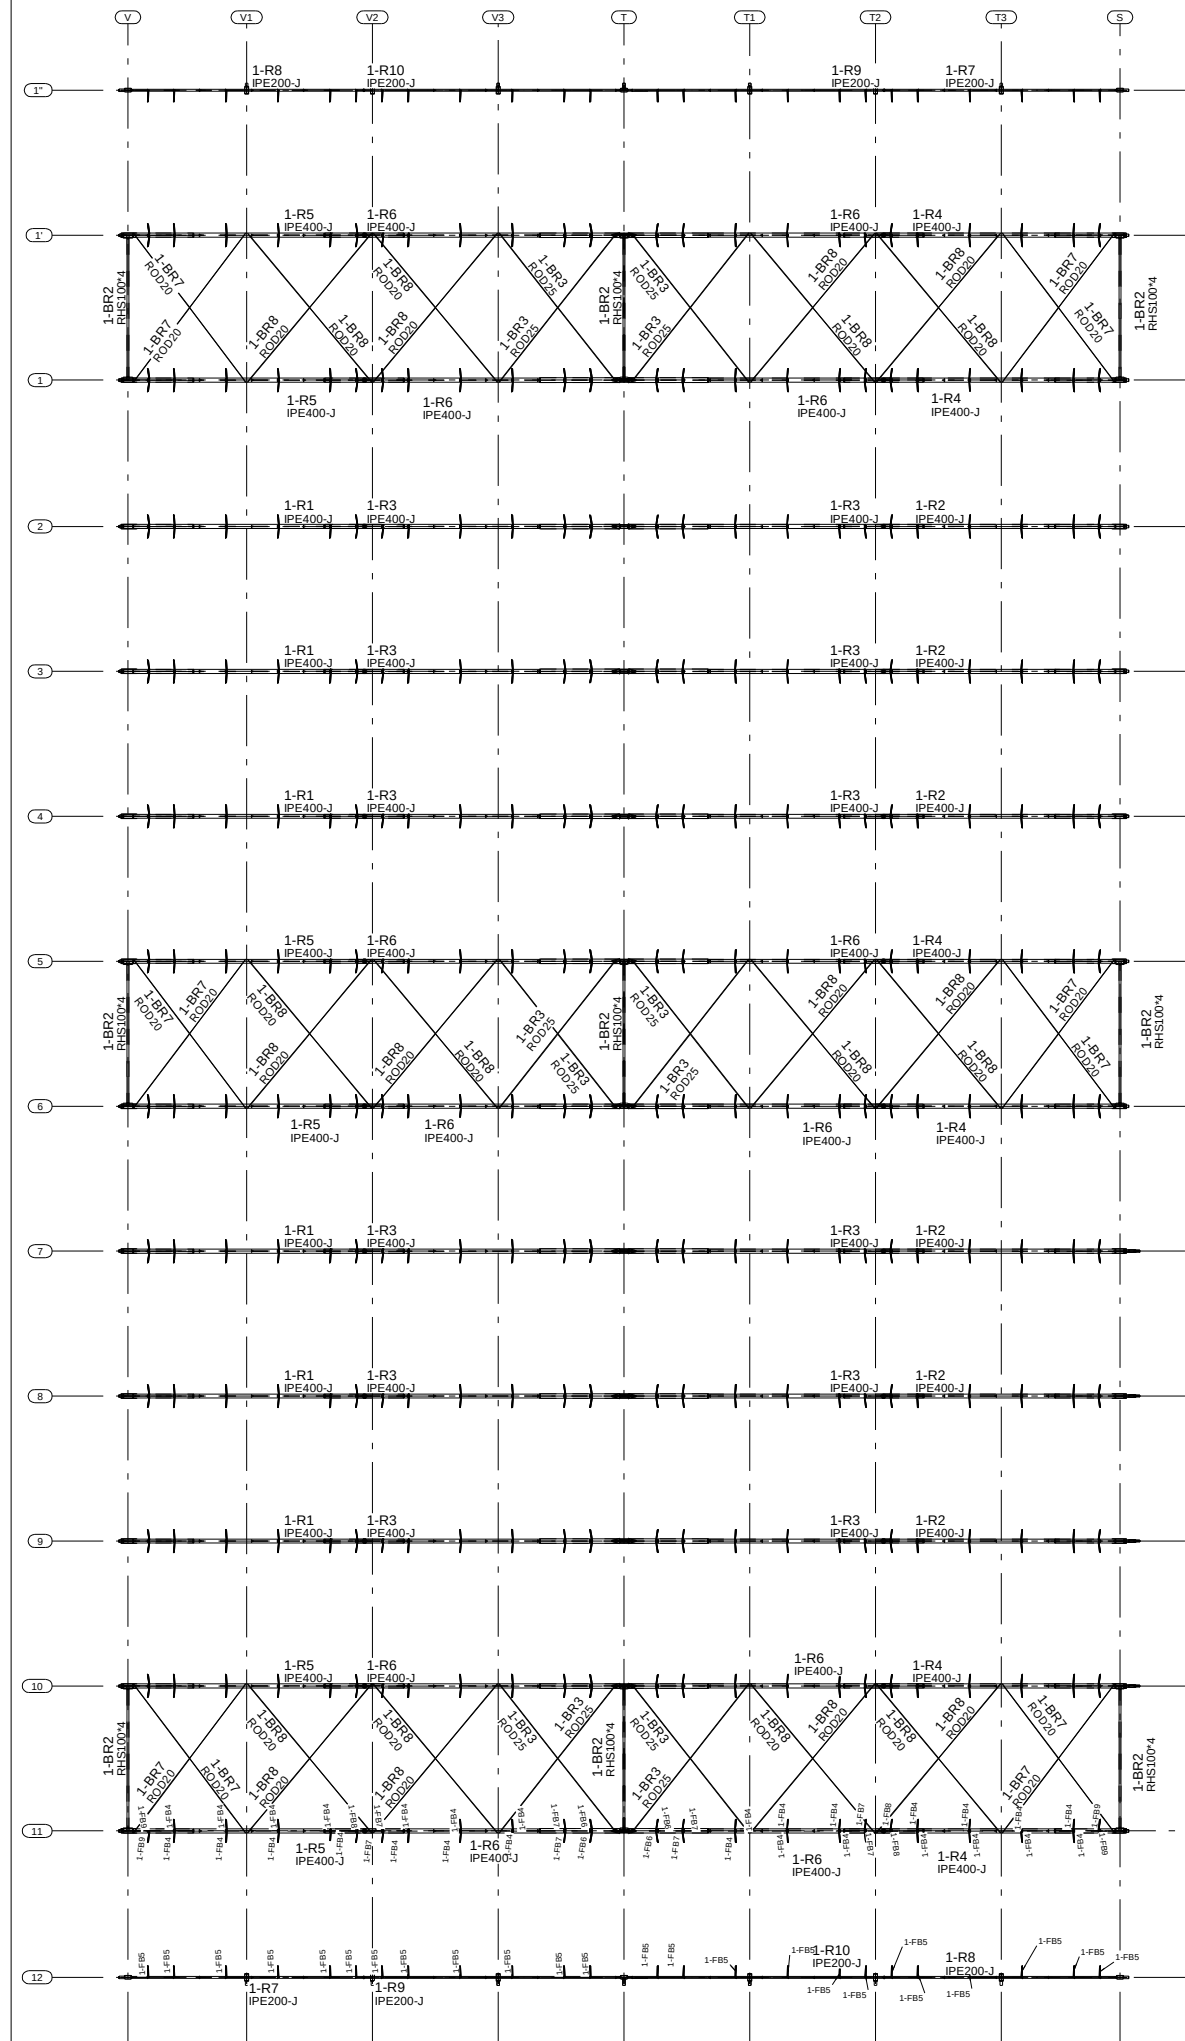

ROOF PLAN WITHOUT PURLIN - Area - 2


AREA - 1

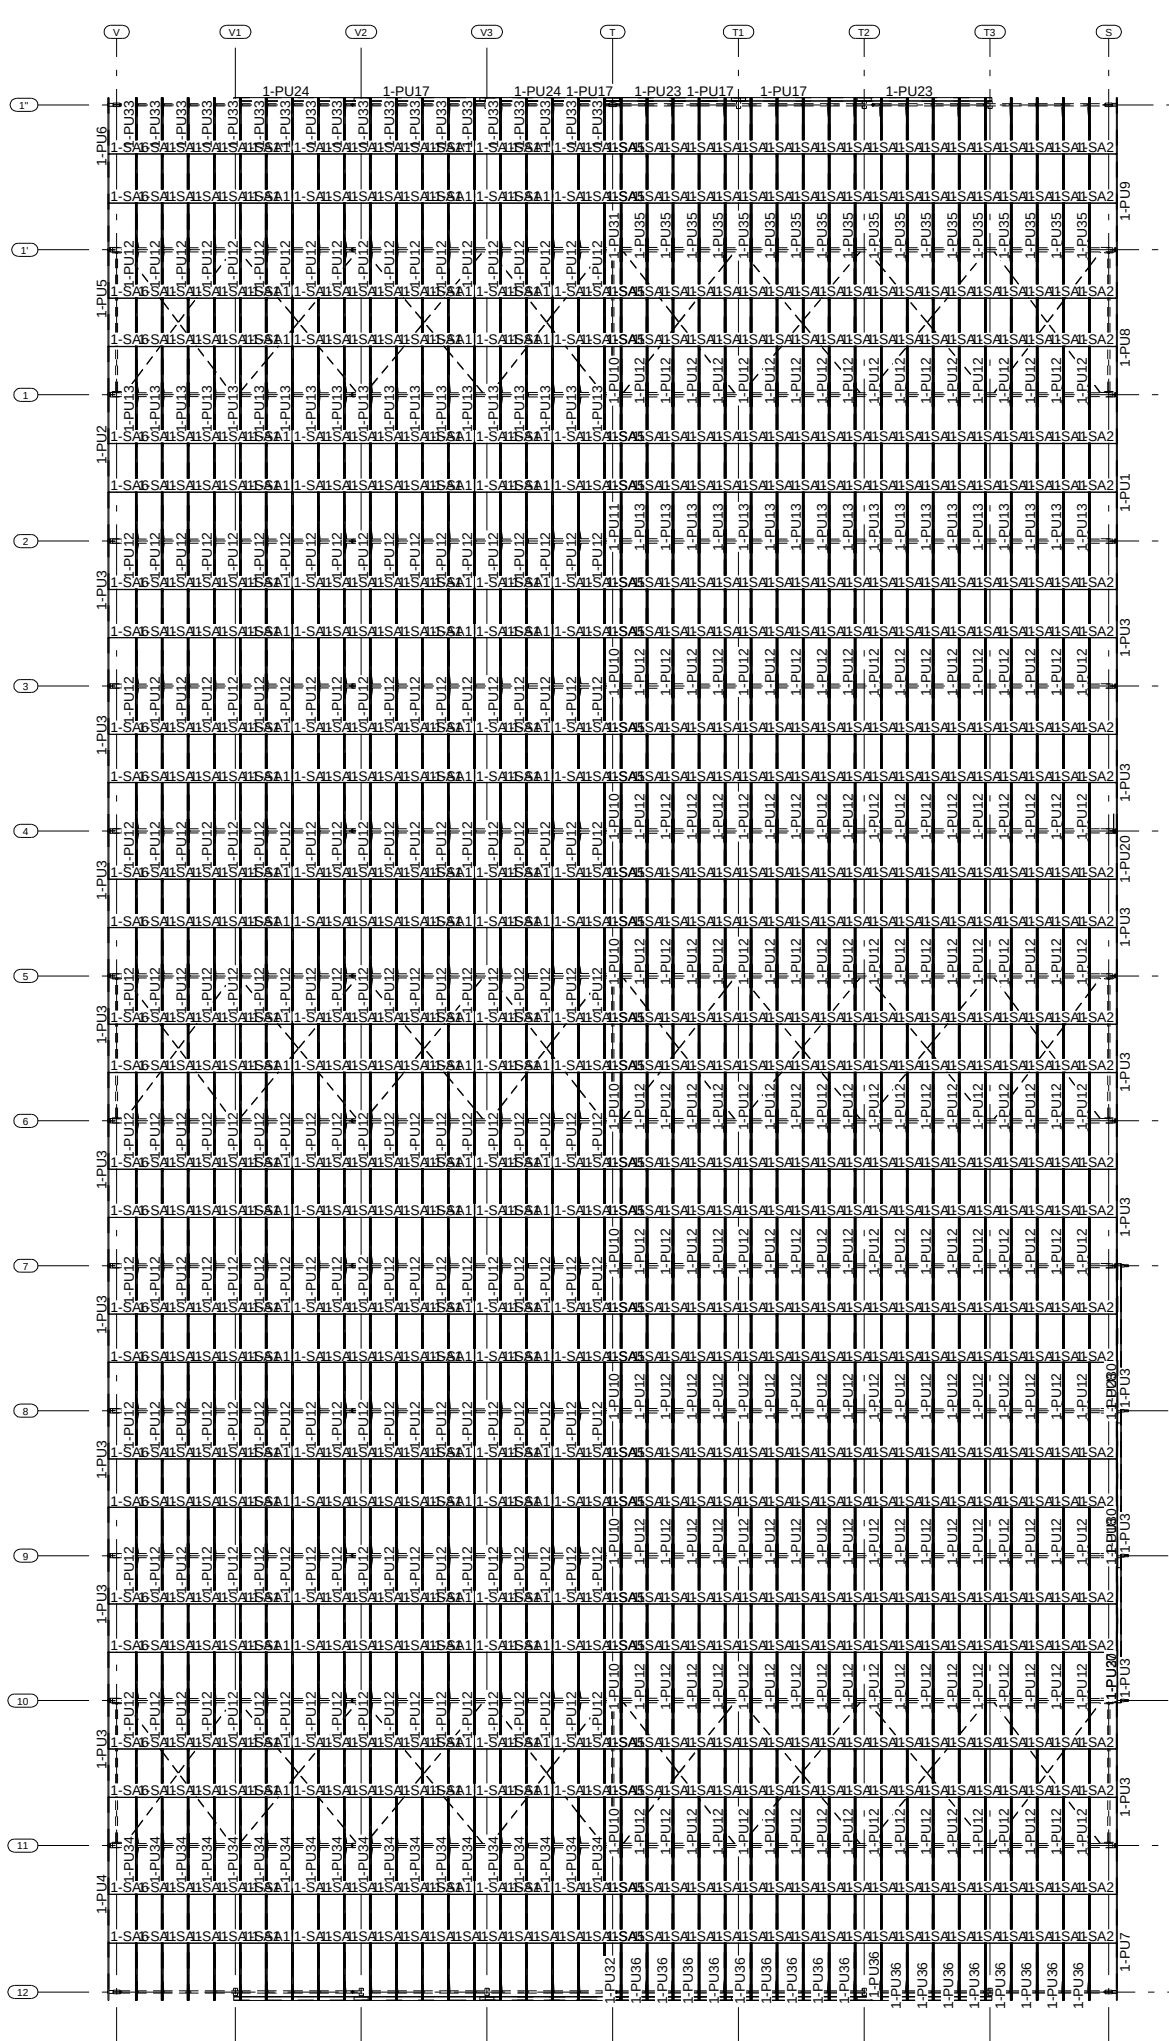

ROOF PLAN WITH PURLIN - Area - 2

		12-08-2028	ISSUED FOR FABRICATION		A.A	H.H
REV.	DATE	DESCRIPTION		DRN	CHK	EDR


PROJECT NAME:						
SCHOOL PROJECT						
CONTRACTOR:						
--						
DRAWING TITLE:						
STEEL STRUCTURE						
ROOF PLAN- Area - 2						
CHECKED BY		A.A		SCALE		
DATE		A.A		SHEET NO.		E07

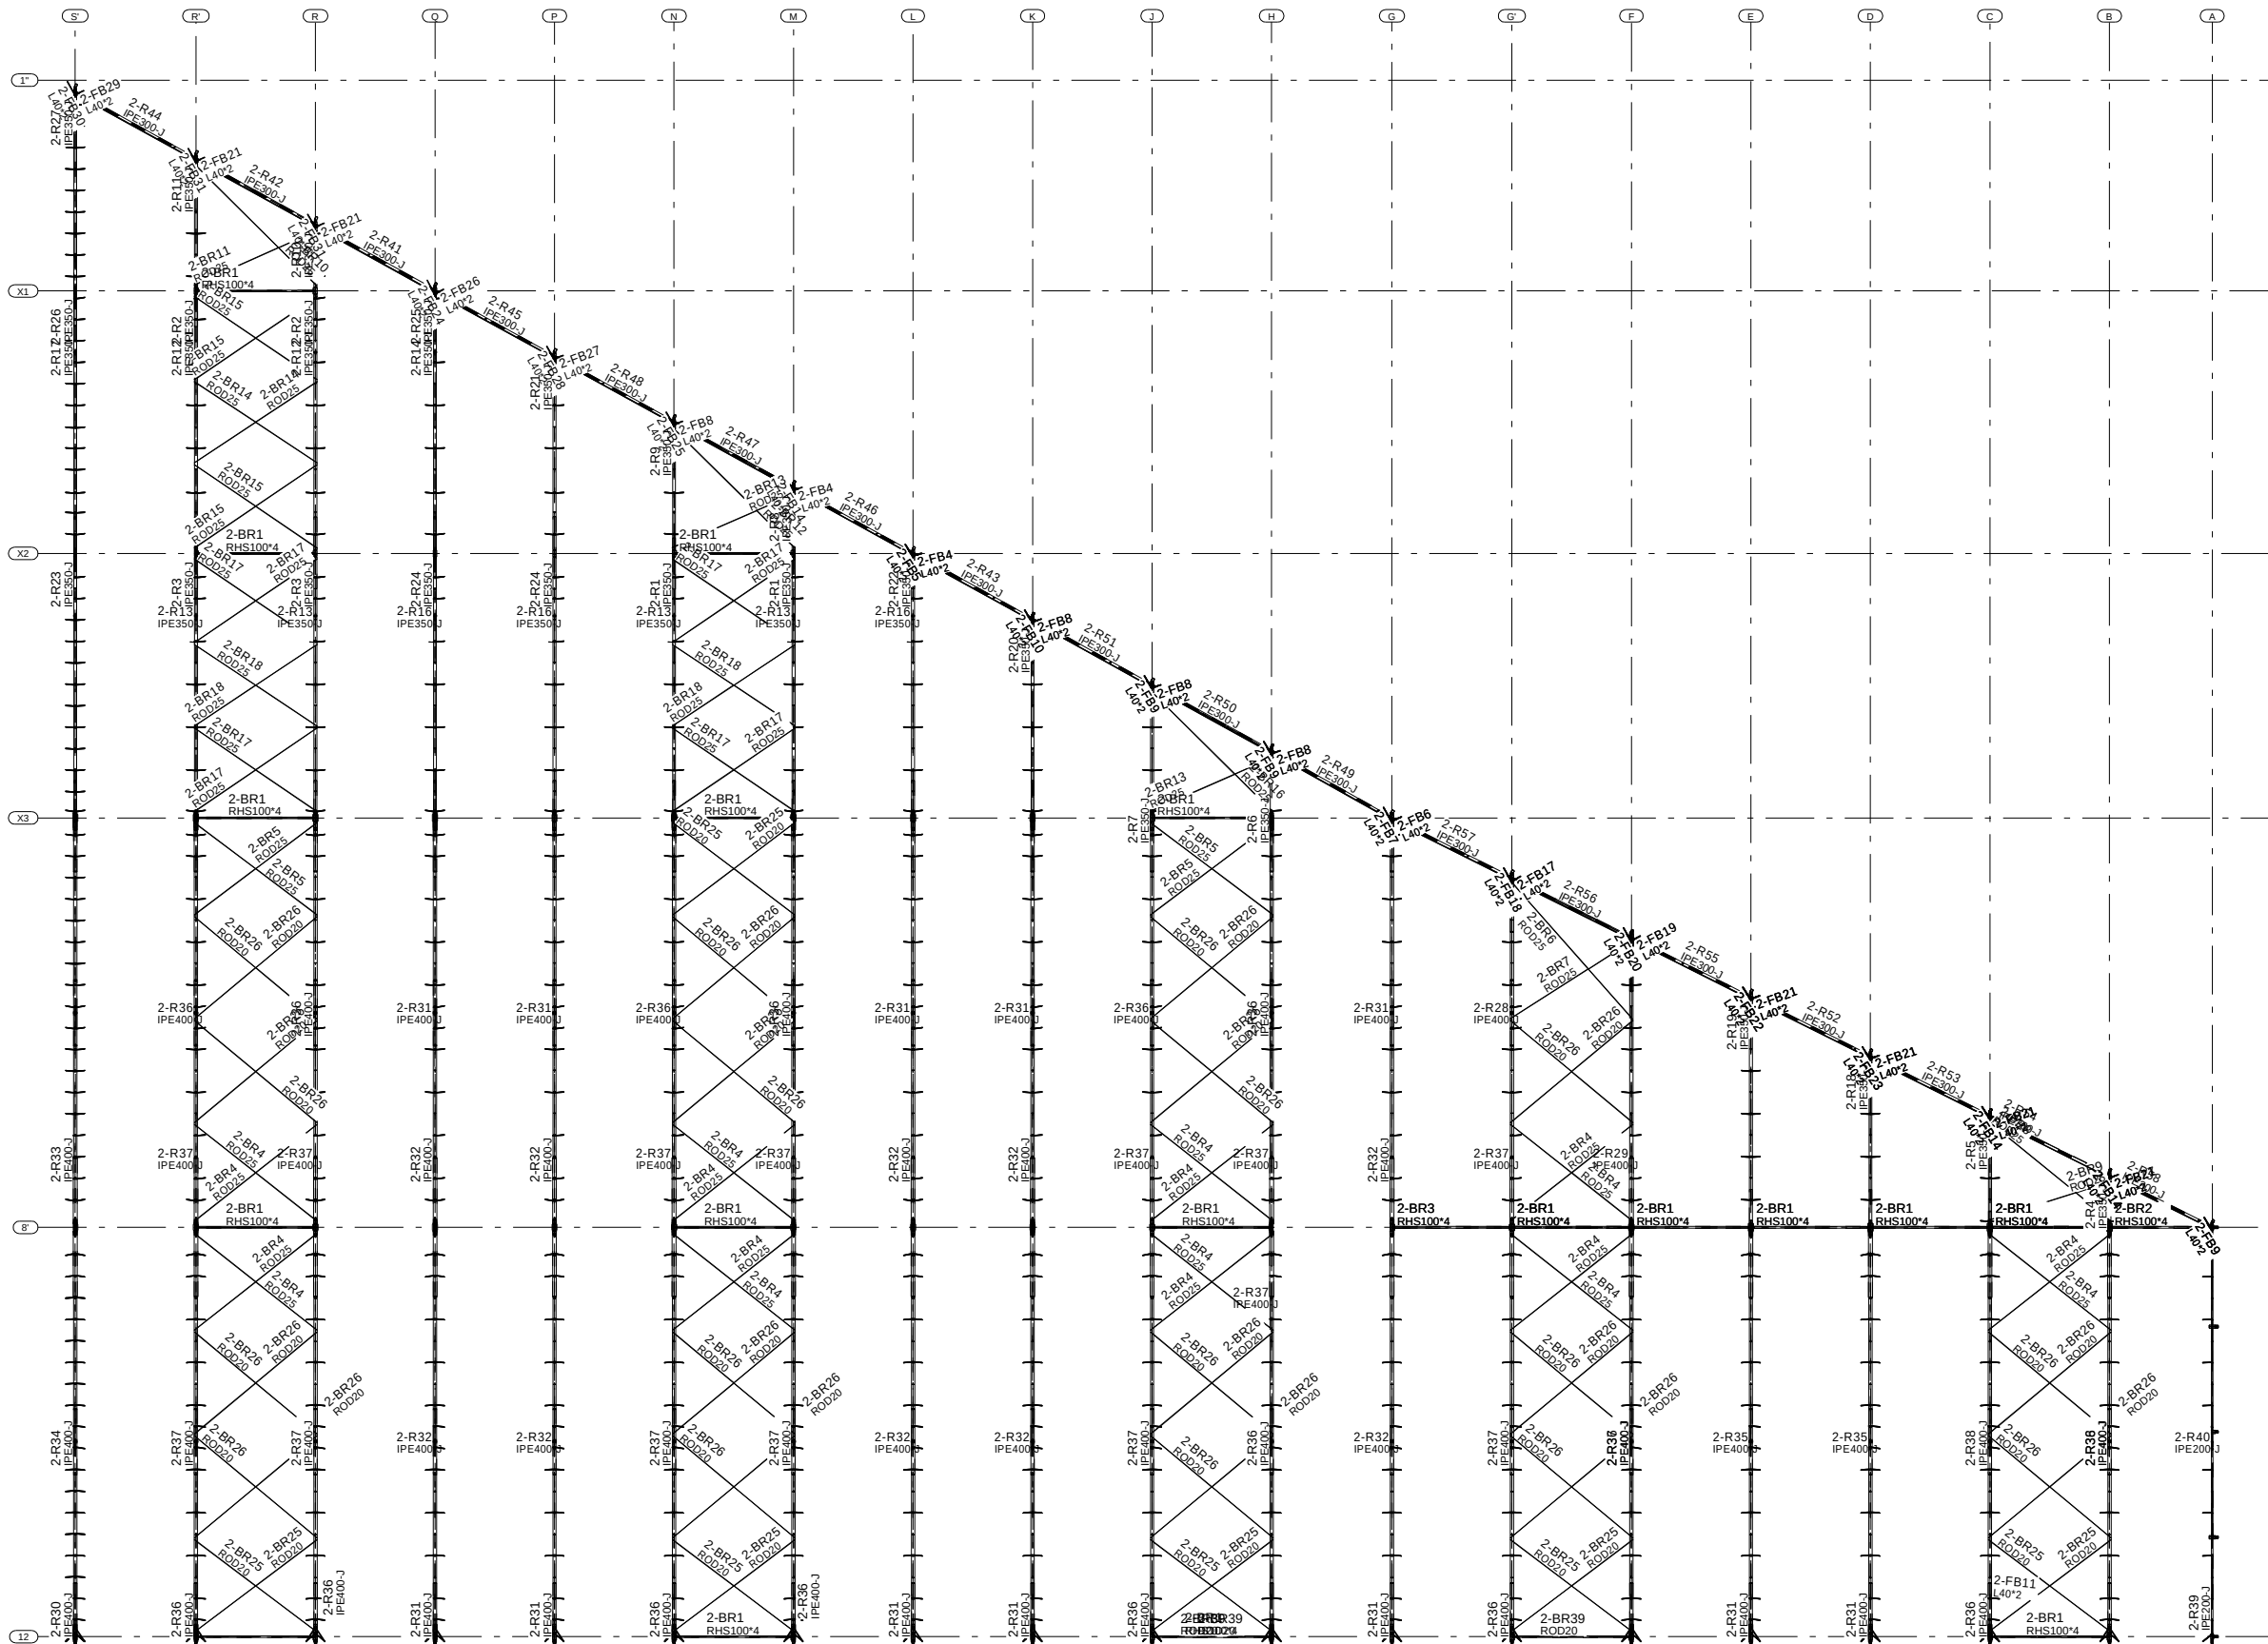

PLAN @EL+9.25

12-08-2024		ISSUED FOR FABRICATION		A.A	H.H
REV.	DATE	DESCRIPTION		DRN	CHK


PROJECT NAME:					
SCHOOL PROJECT					
CONTRACTOR:					
--					
DRAWING TITLE:					
STEEL STRUCTURE					
ROOF PLAN WITHOUT PURLIN- Area - 3					
CHECKED BY		A.A	SCALE		
DATE		A.A	SHEET NO.		E08

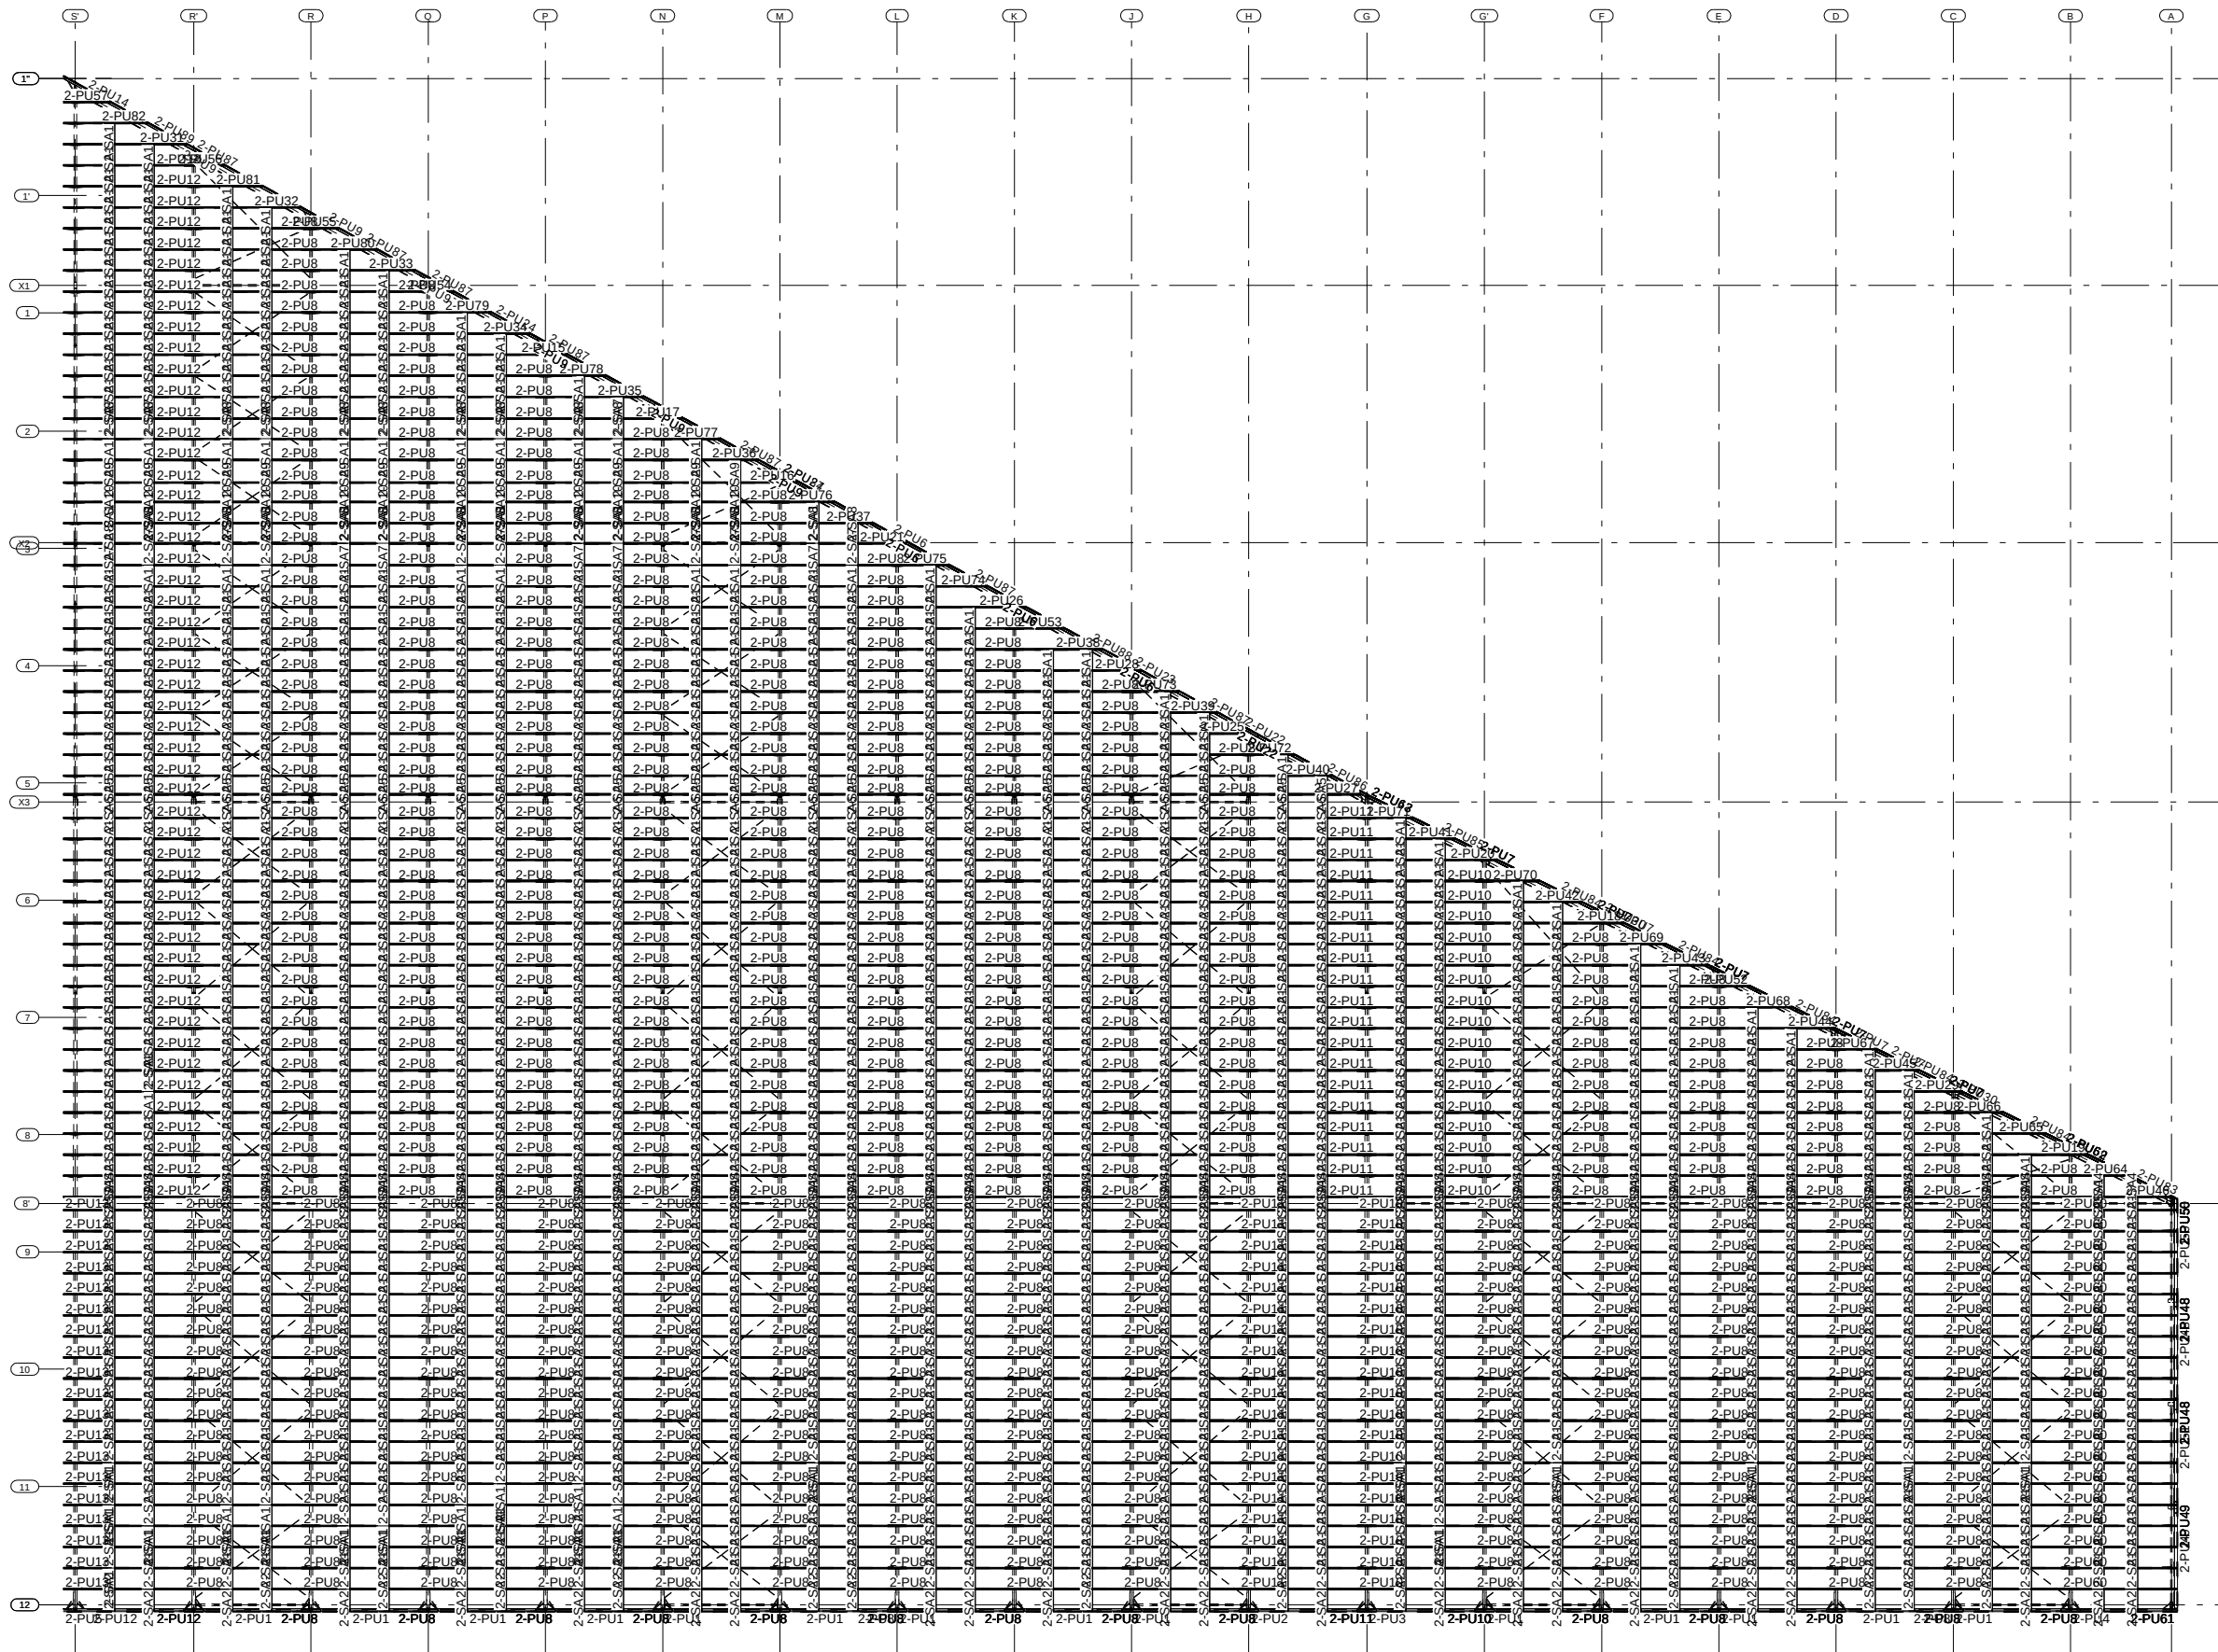


PLAN @EL+9.25

		ISSUED FOR FABRICATION		A.A		H.H	
REV.	DATE	DESCRIPTION		DRN	CHK	CIN	


PROJECT NAME:							
SCHOOL PROJECT							
CONTRACTOR:							
--							
DRAWING TITLE:							
STEEL STRUCTURE							
ROOF PLAN WITHOUT PURLIN- Area - 3							
CHECKED BY		A.A		SCALE			
DATE		A.A		SHEET NO.		E09	

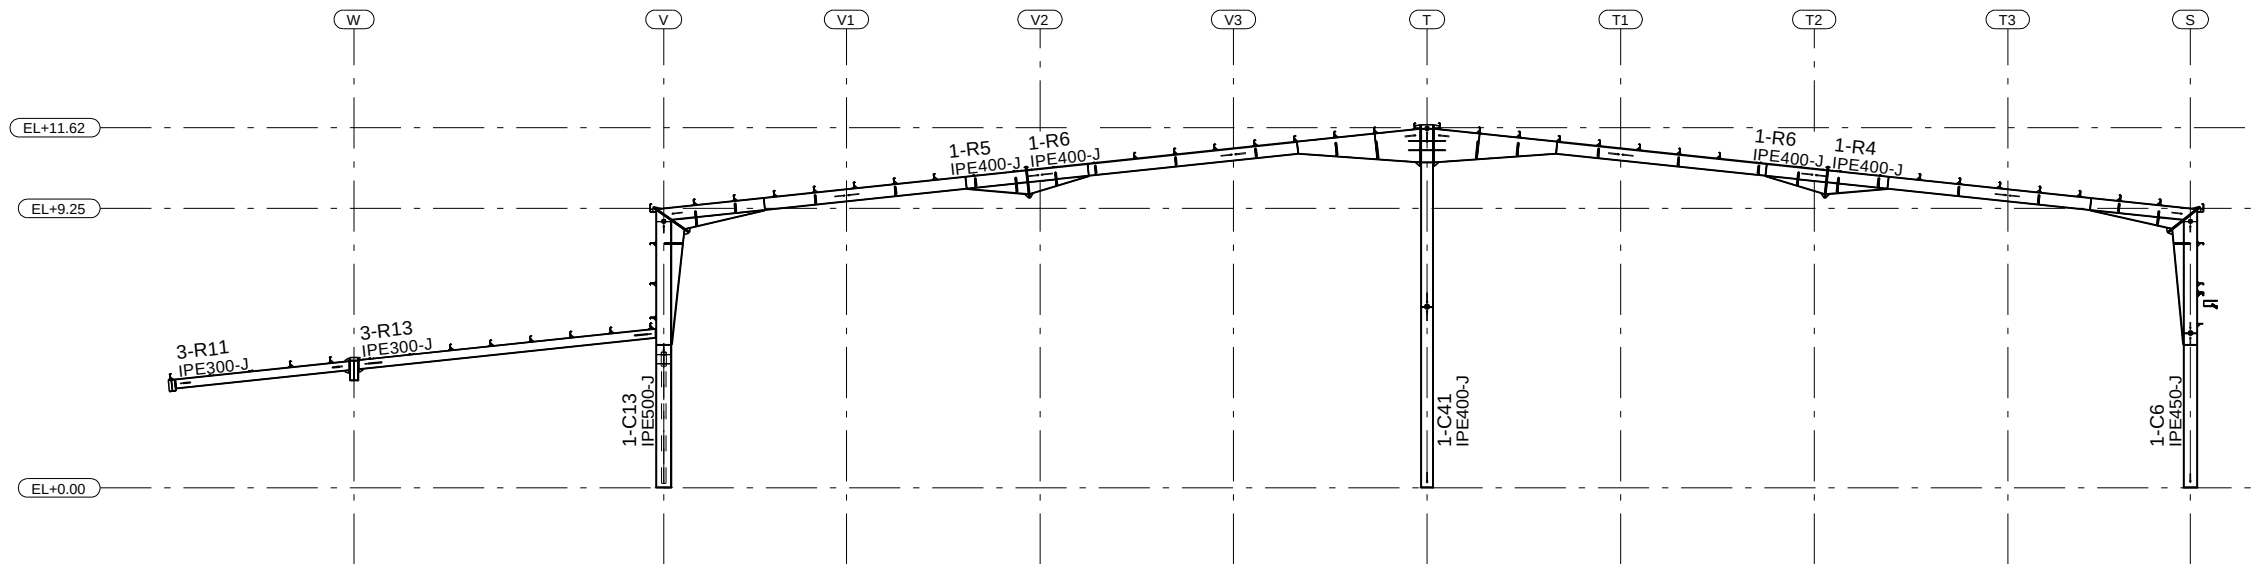

SECTION GRID 1

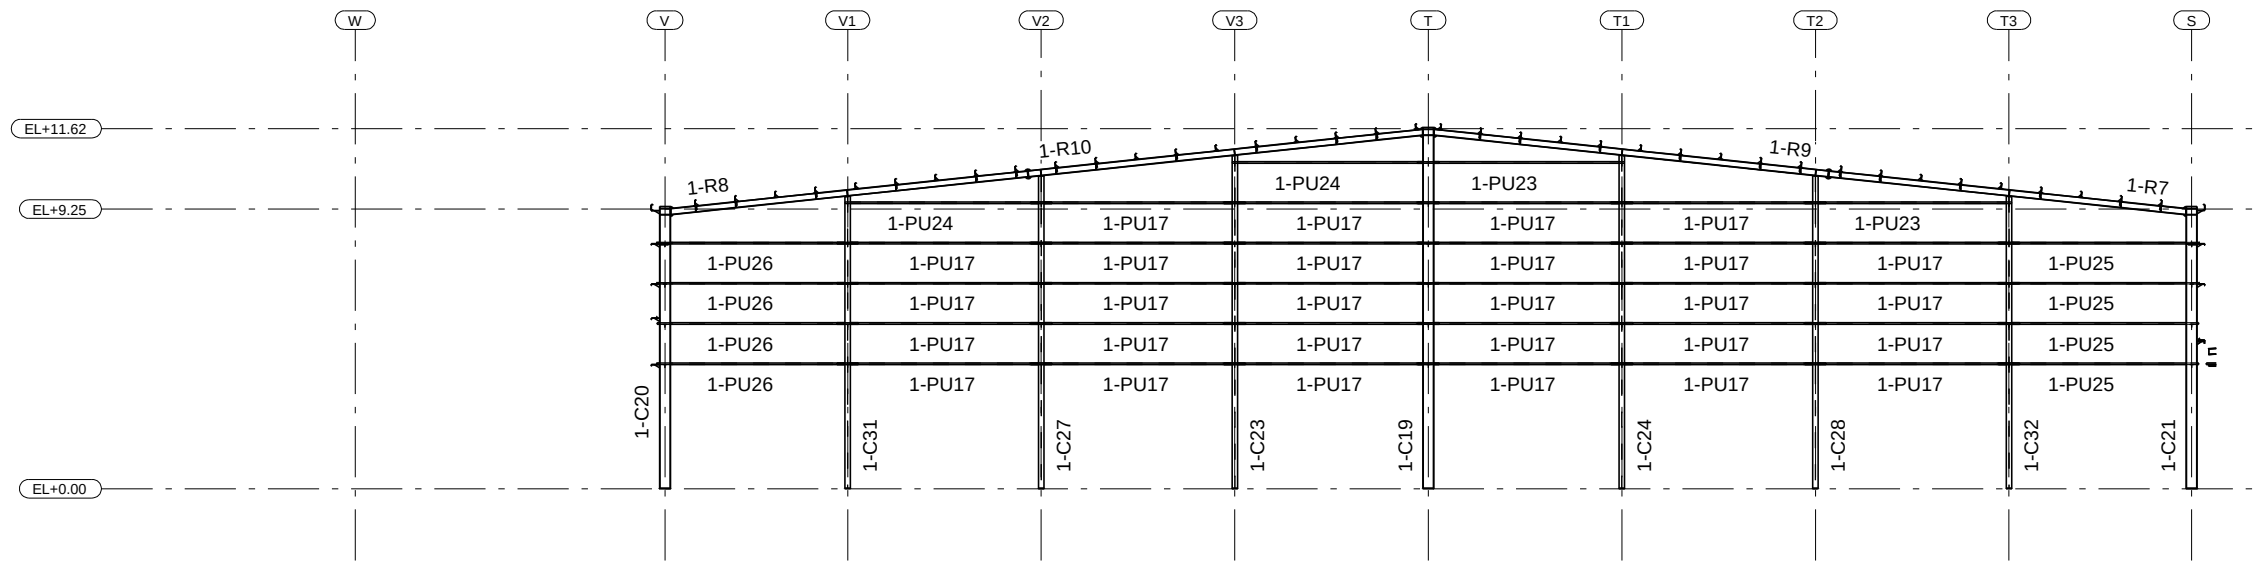


SECTION GRID 1"

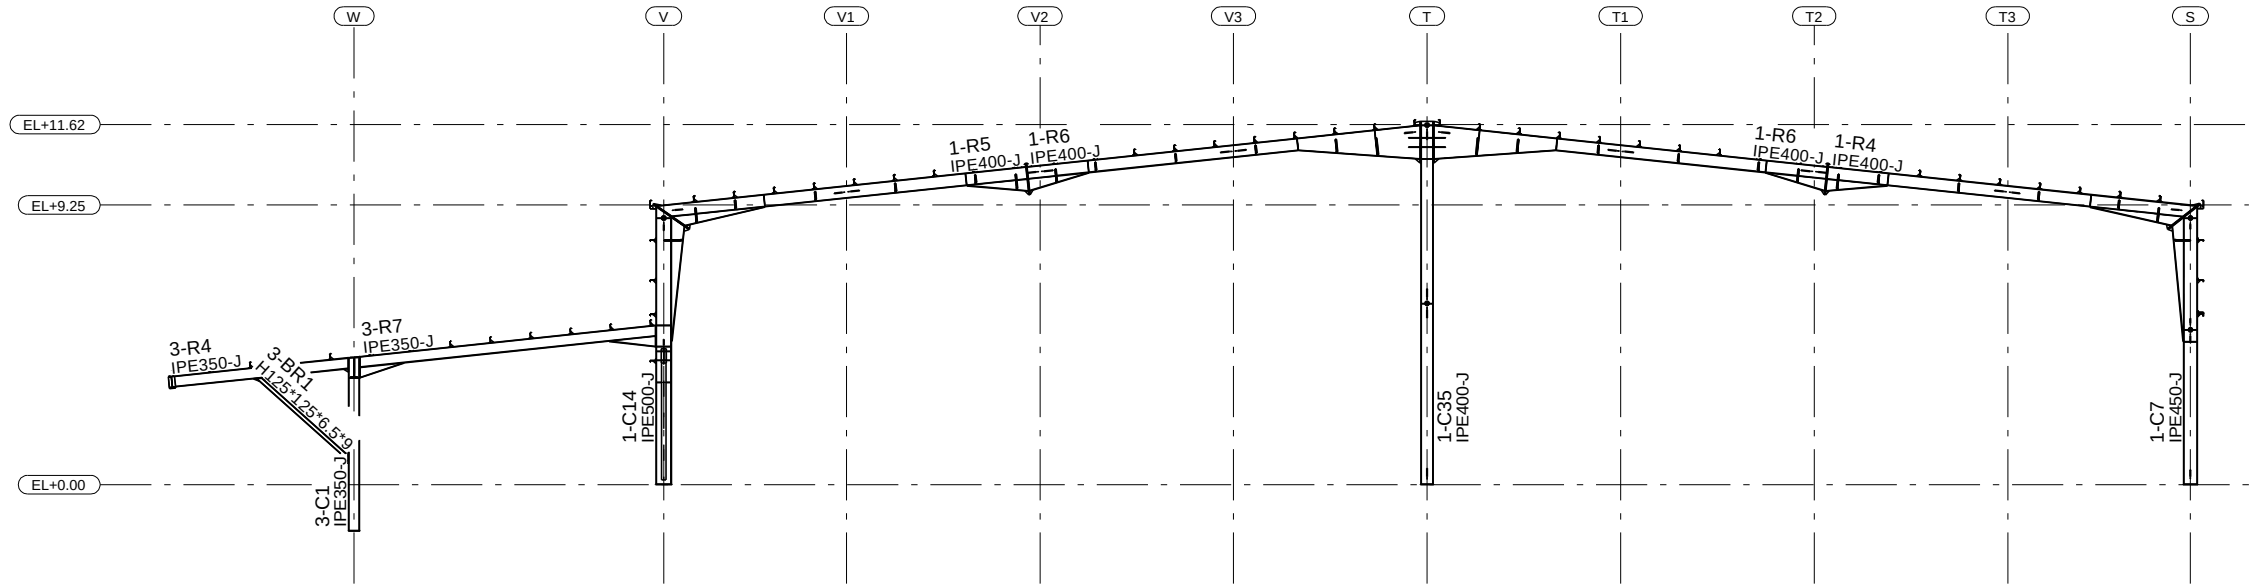


SECTION GRID 1'


FD	12-06-2026	ISSUED FOR FABRICATION	A.A	H.H	
REV	DATE	DESCRIPTION	DRN	CHK	DSN
.....					
PROJECT NAME:					
SCHOOL PROJECT					
CONTRACTOR:					
..					
DRAWING TITLE:					
STEEL STRUCTURE					
SECTION GRID (1 + 1' + 1")					
CHECKED BY	A.A	SCALE			
DATE	A.A	SHEET NO.	E10		

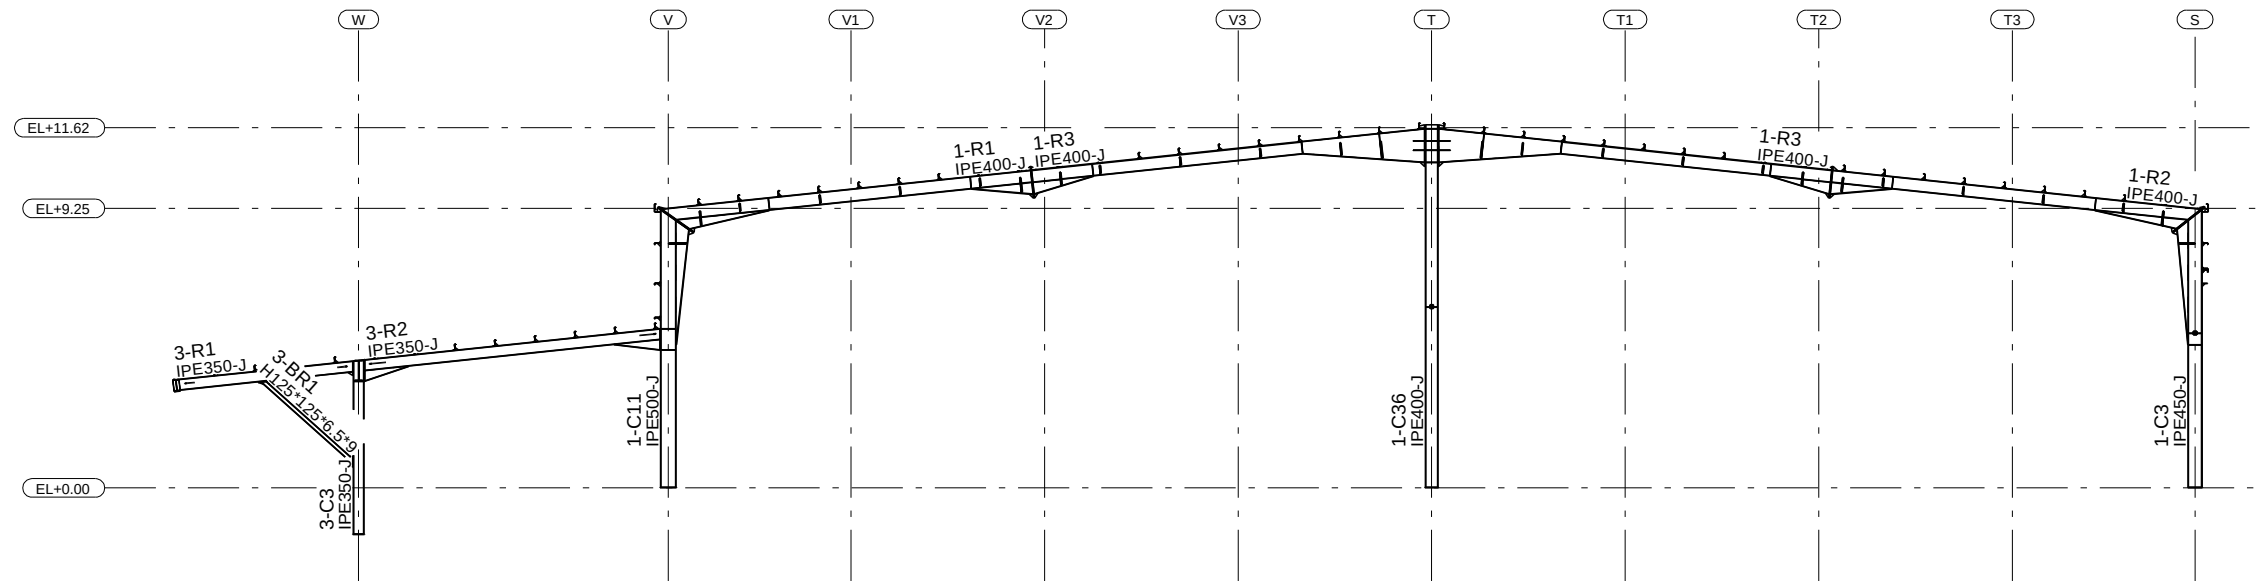

SECTION GRID 2

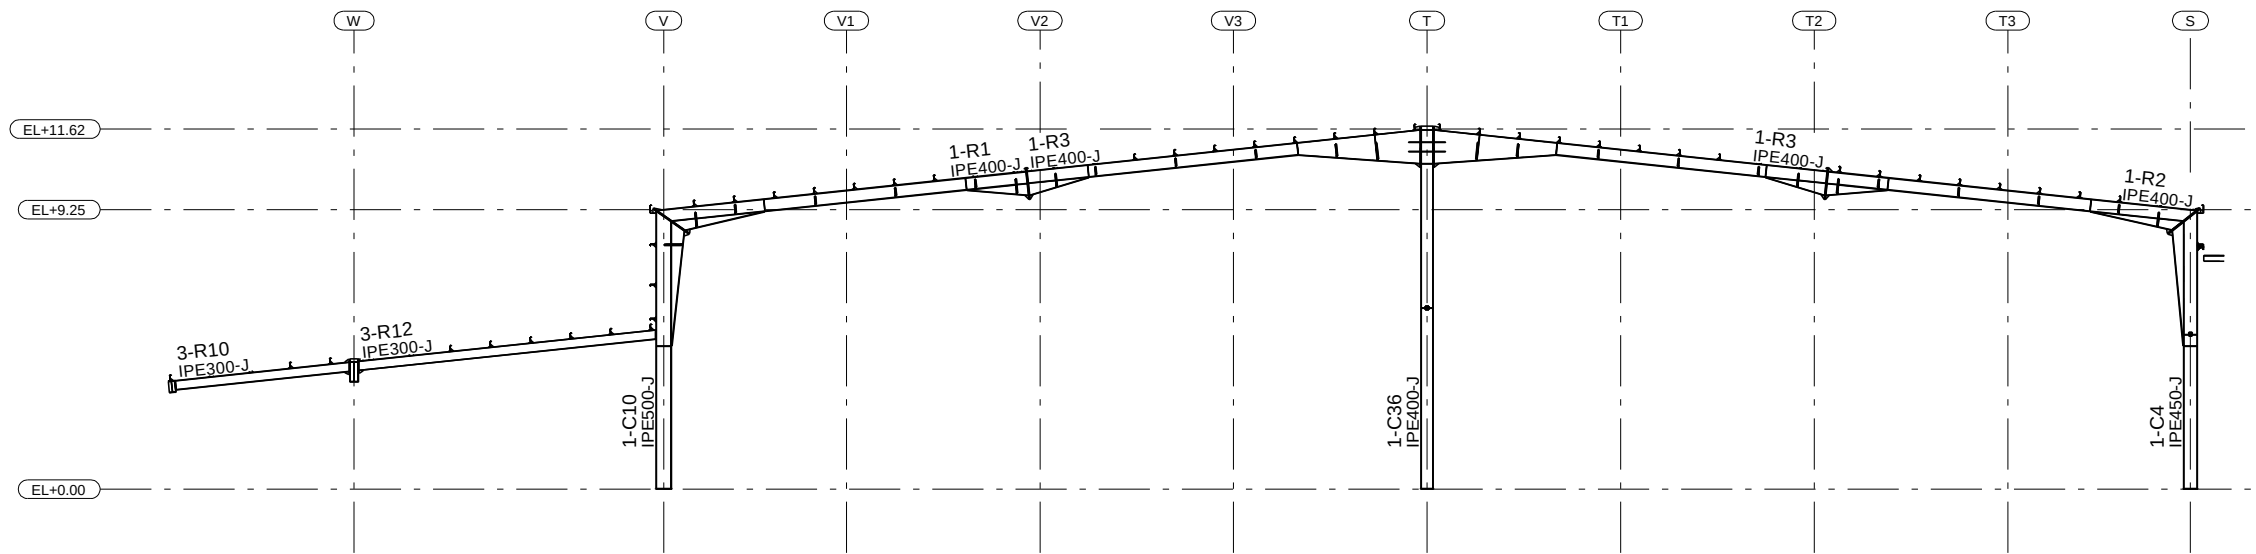


SECTION GRID 3

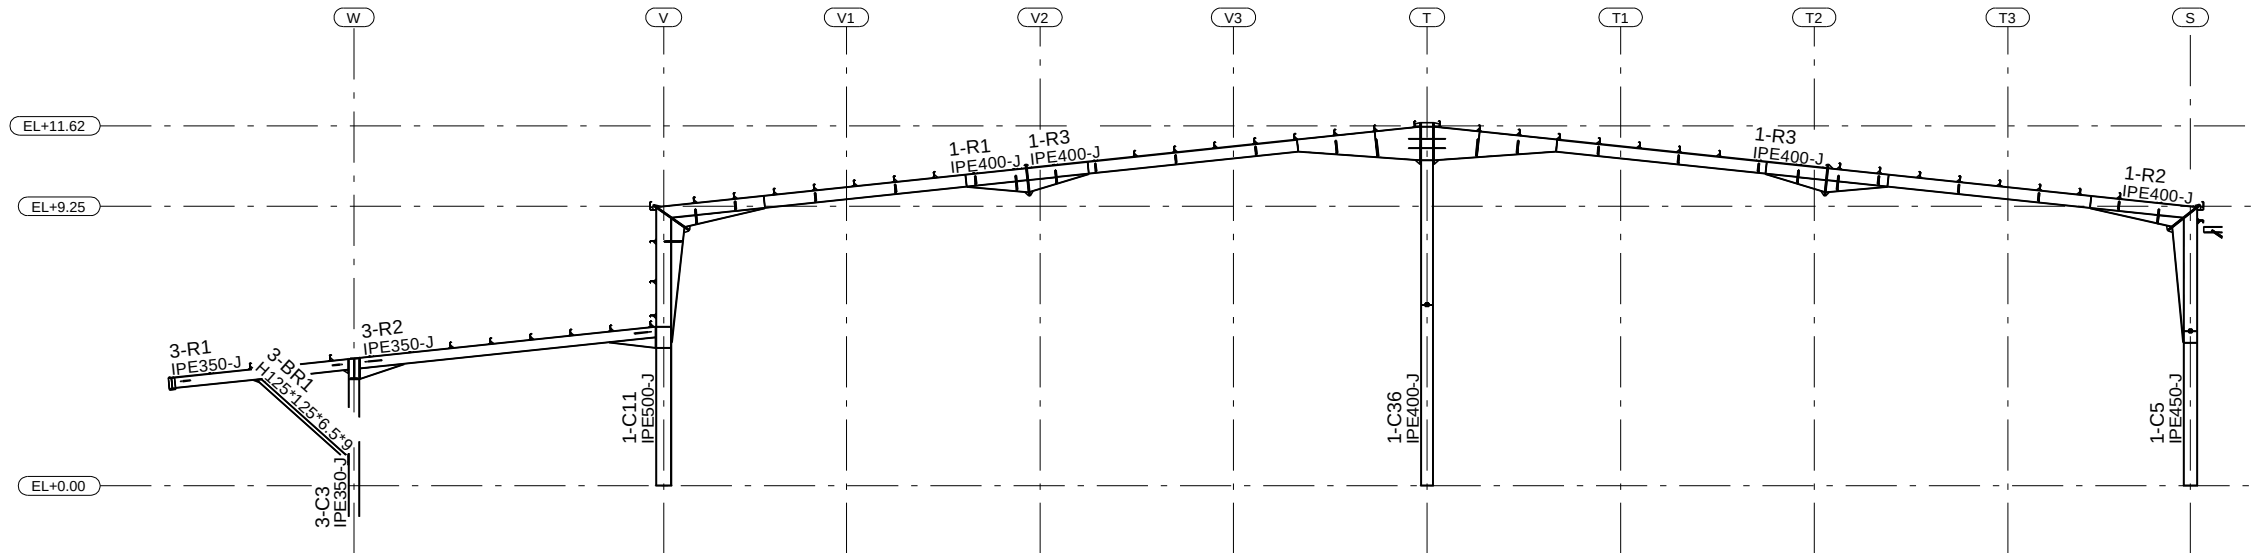


SECTION GRID 4


FD	12-06-2026	ISSUED FOR FABRICATION		A.A	H.H	
	REV	DATE	DESCRIPTION	DRN	CHK	DSN
.....						
PROJECT NAME:						
SCHOOL PROJECT						
CONTRACTOR:						
--						
DRAWING TITLE:						
STEEL STRUCTURE						
SECTION GRID (2 + 3 + 4)						
CHECKED BY		A.A		SCALE		
DATE		A.A		SHEET NO.		E11

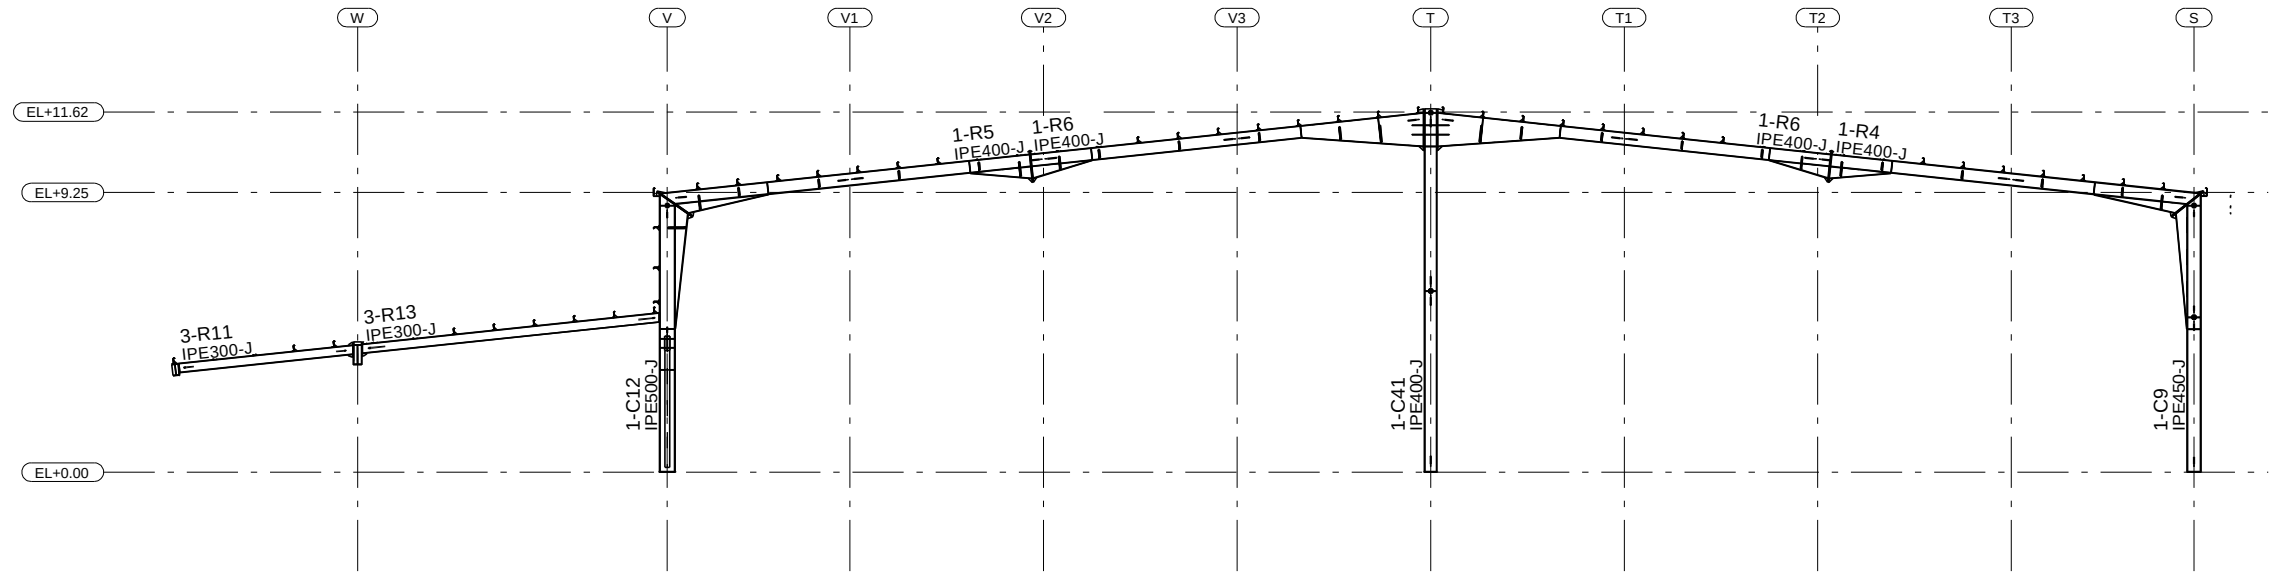

SECTION GRID 5

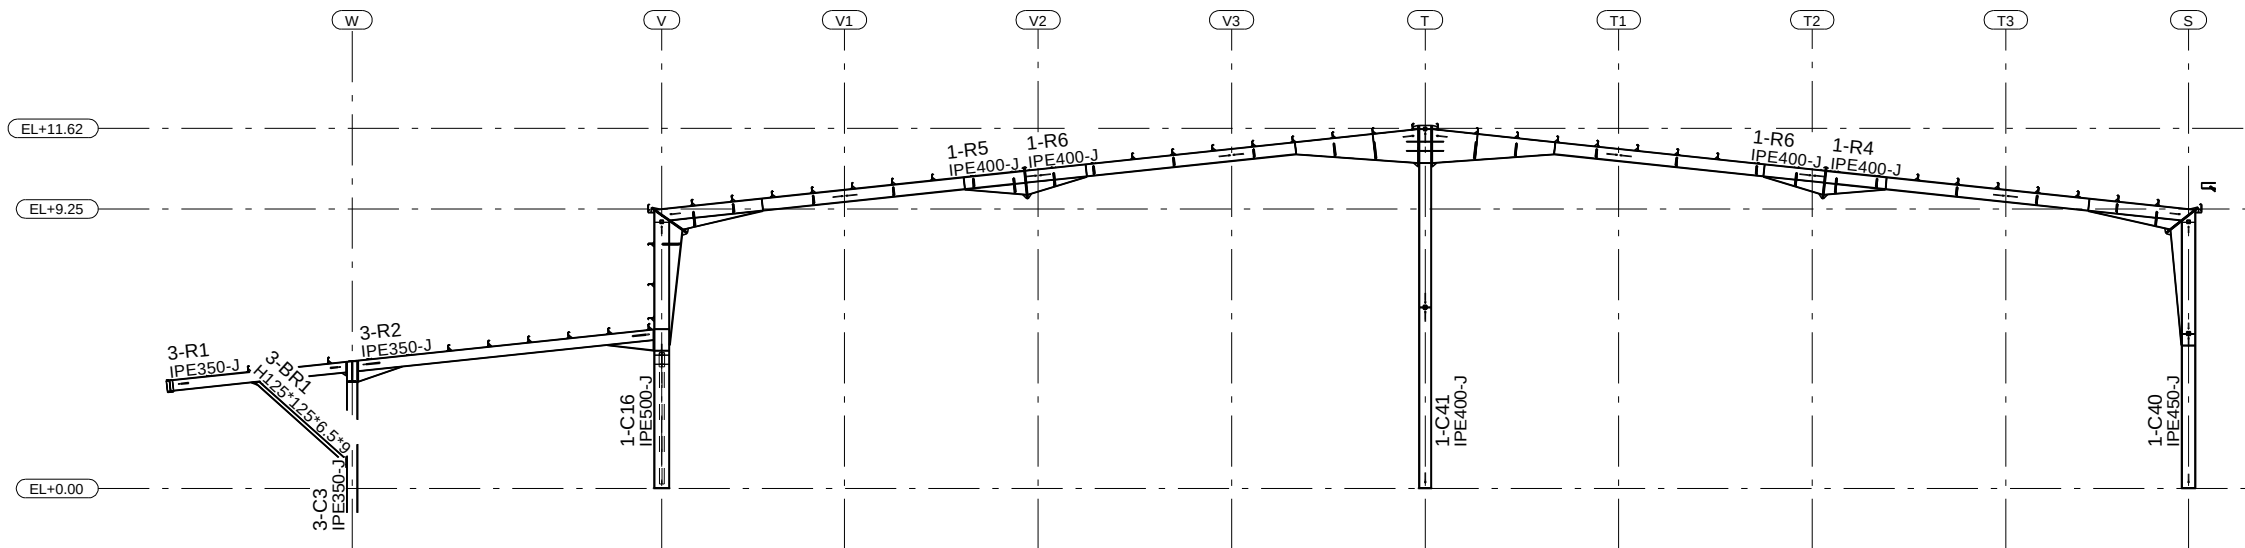


SECTION GRID 6

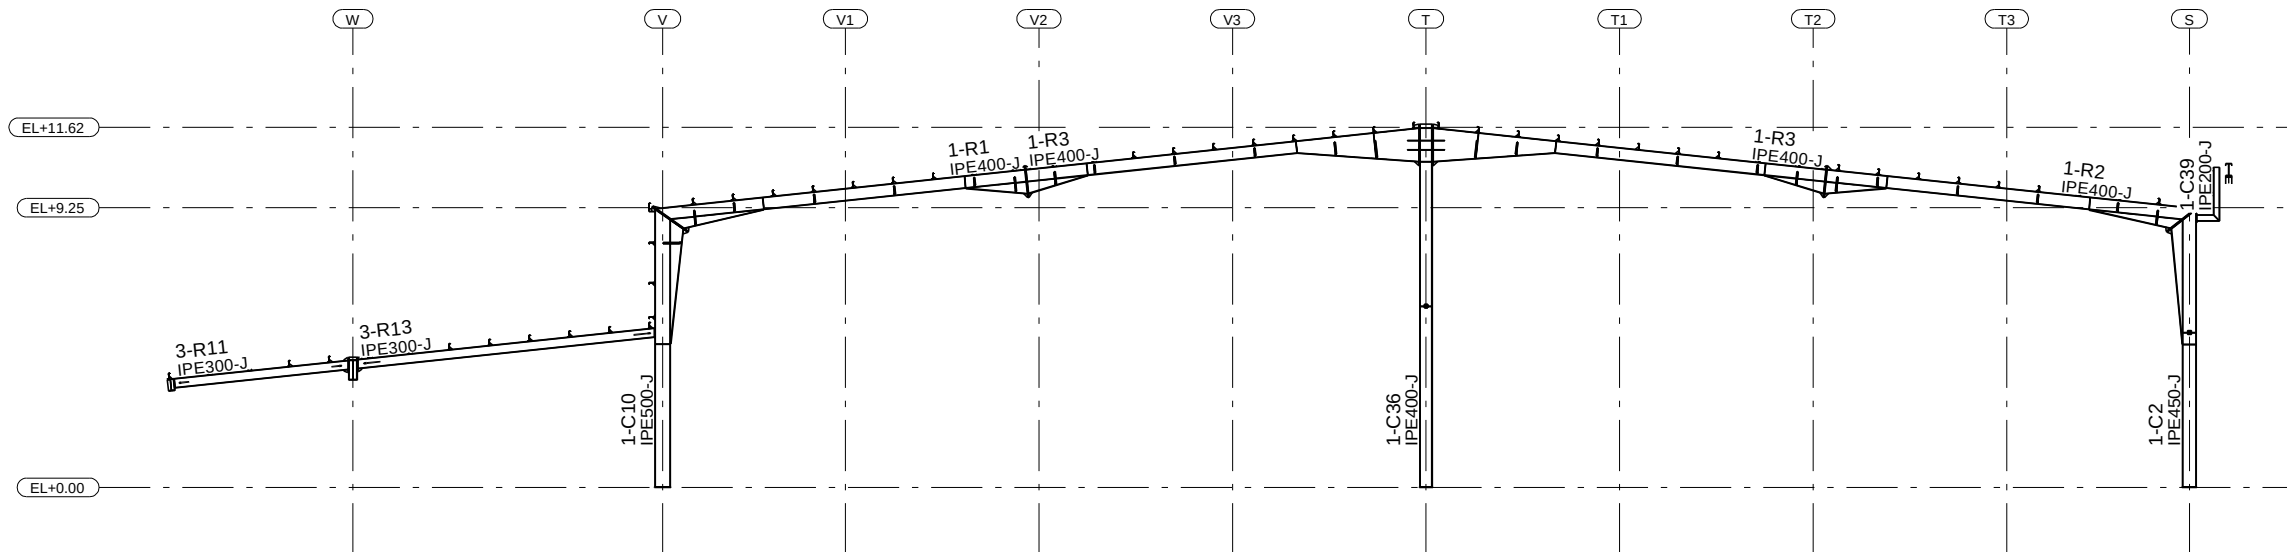


SECTION GRID 7


FD	12-06-2026	ISSUED FOR FABRICATION	A.A	H.H	
REV	DATE	DESCRIPTION	DRN	CHK	DSN
PROJECT NAME:					
SCHOOL PROJECT					
CONTRACTOR:					
DRAWING TITLE:					
STEEL STRUCTURE					
SECTION GRID (5 + 6 + 7)					
CHECKED BY	A.A	SCALE			
DATE	A.A	SHEET NO.	E12		

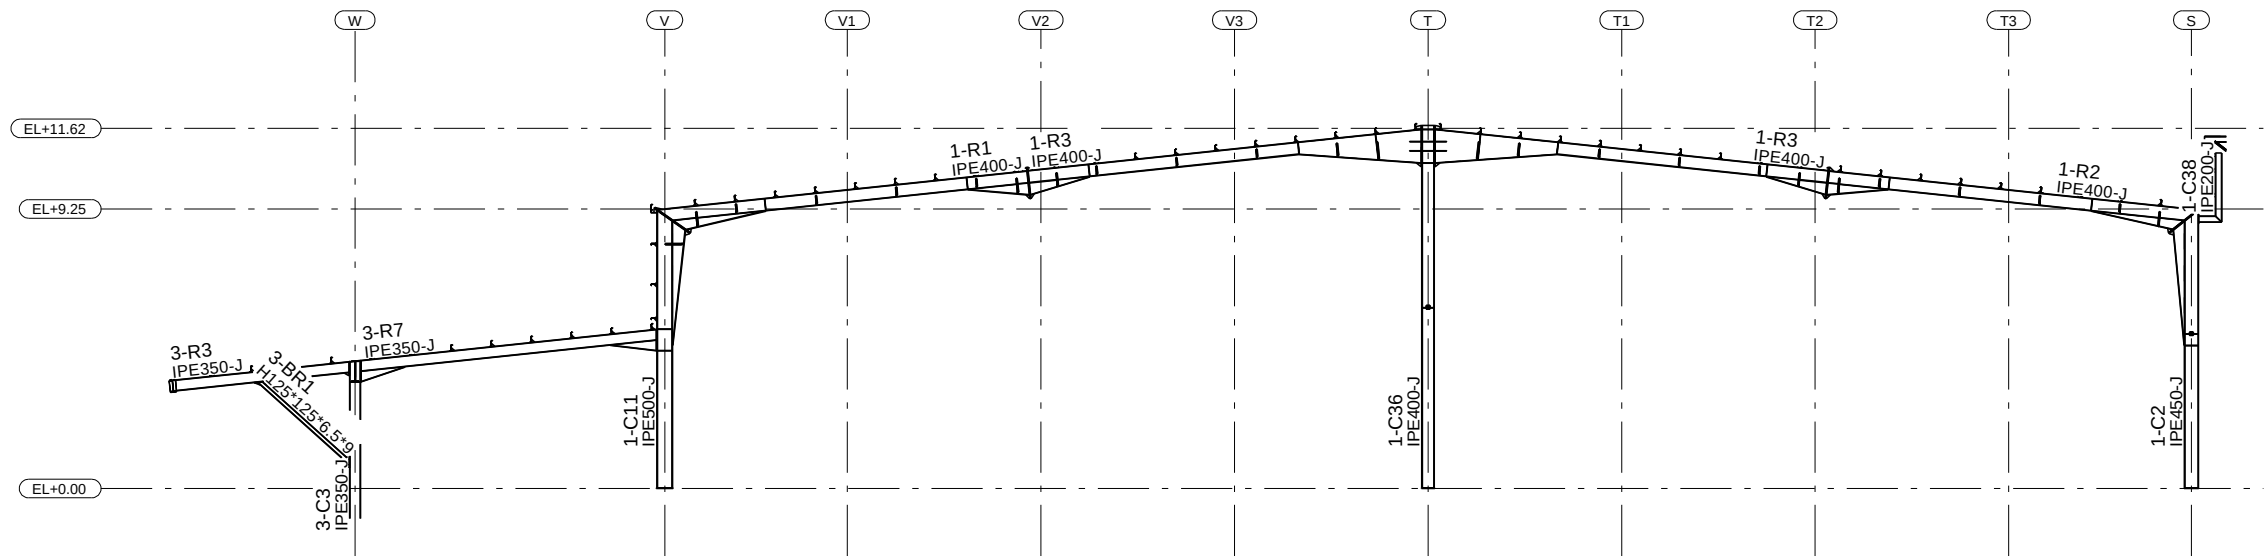

SECTION GRID 8

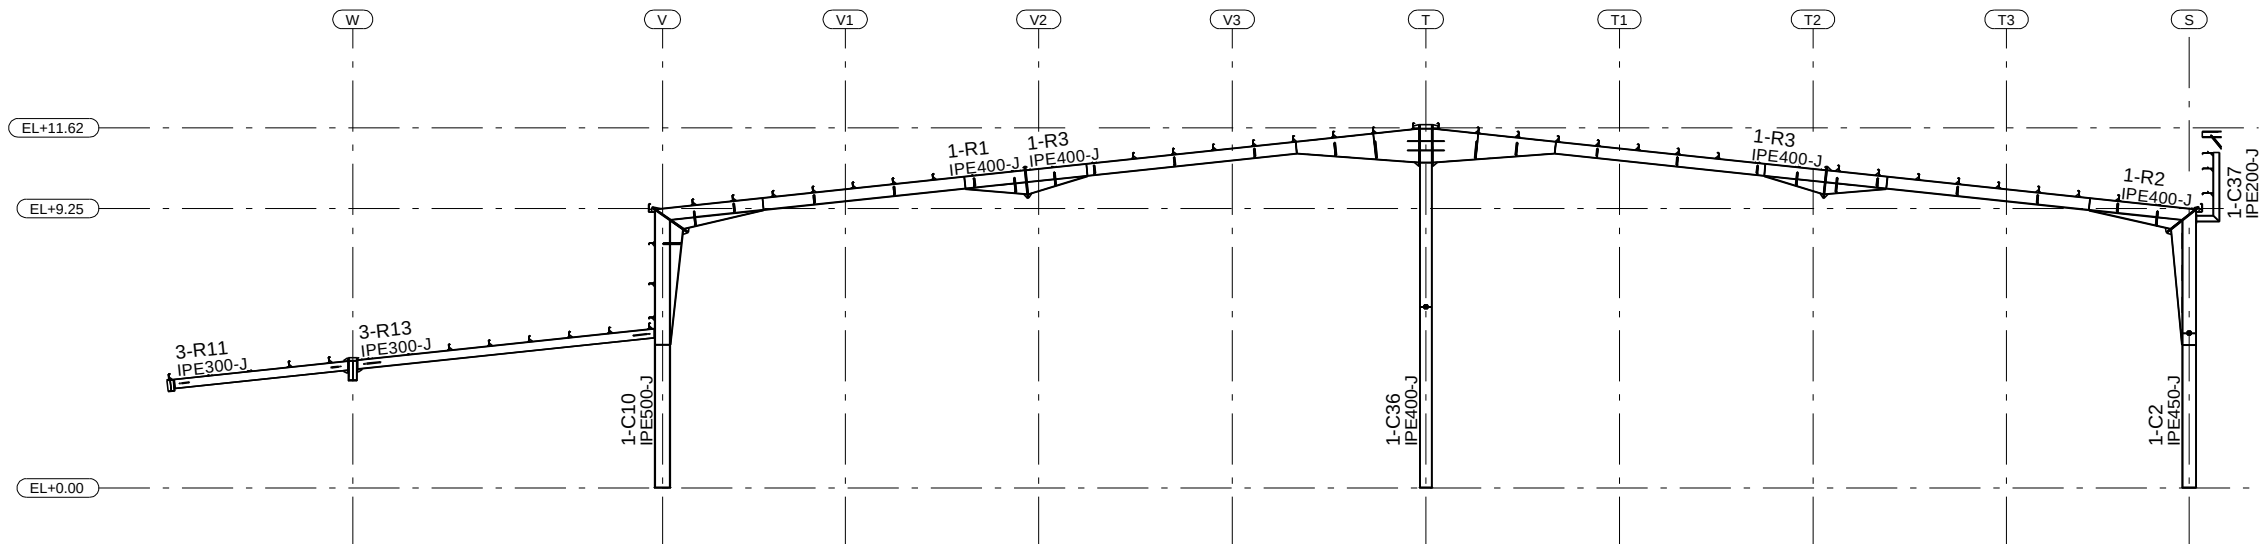


SECTION GRID 9

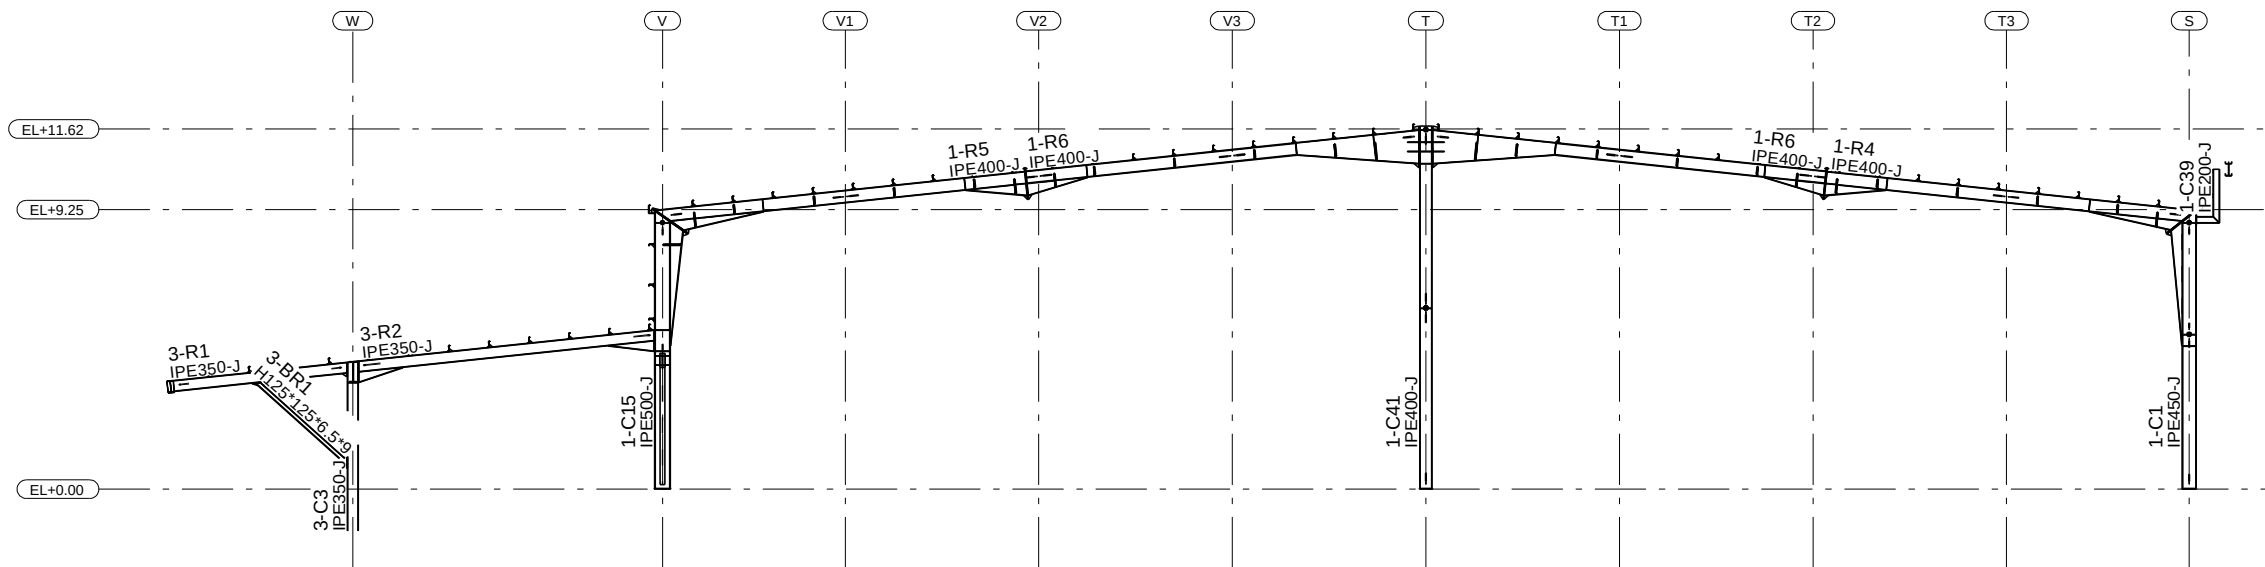


SECTION GRID 10

FD	12-06-2026	ISSUED FOR FABRICATION	A.A	H.H	
REV	DATE	DESCRIPTION	DRN	CHK	DSN
PROJECT NAME:					
SCHOOL PROJECT					
CONTRACTOR:					

DRAWING TITLE:					
STEEL STRUCTURE					
SECTION GRID (8 + 9 + 10)					
CHECKED BY	A.A	SCALE			
DATE	A.A	SHEET NO.	E13		

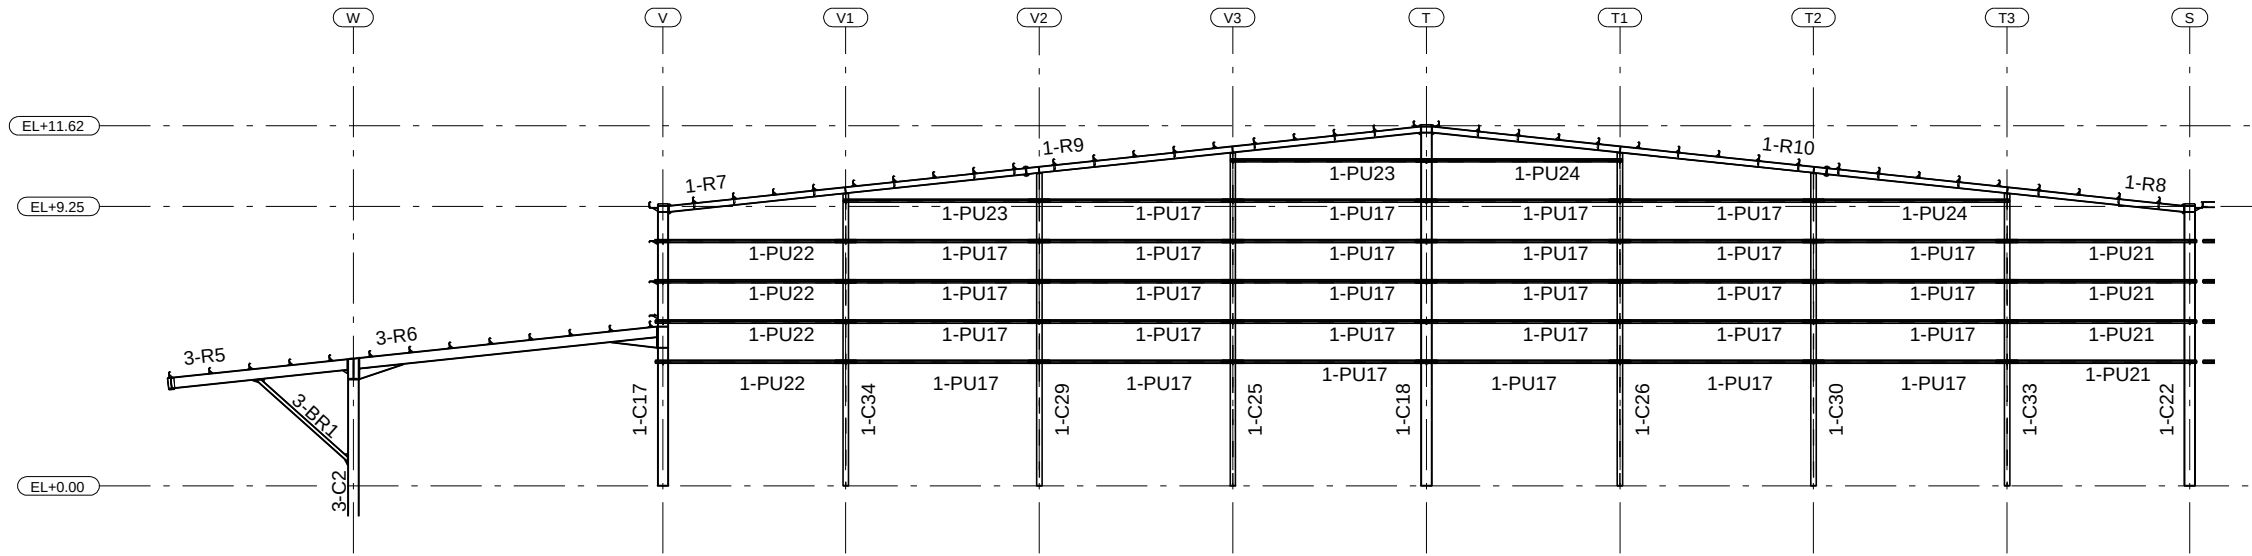


SECTION GRID 12

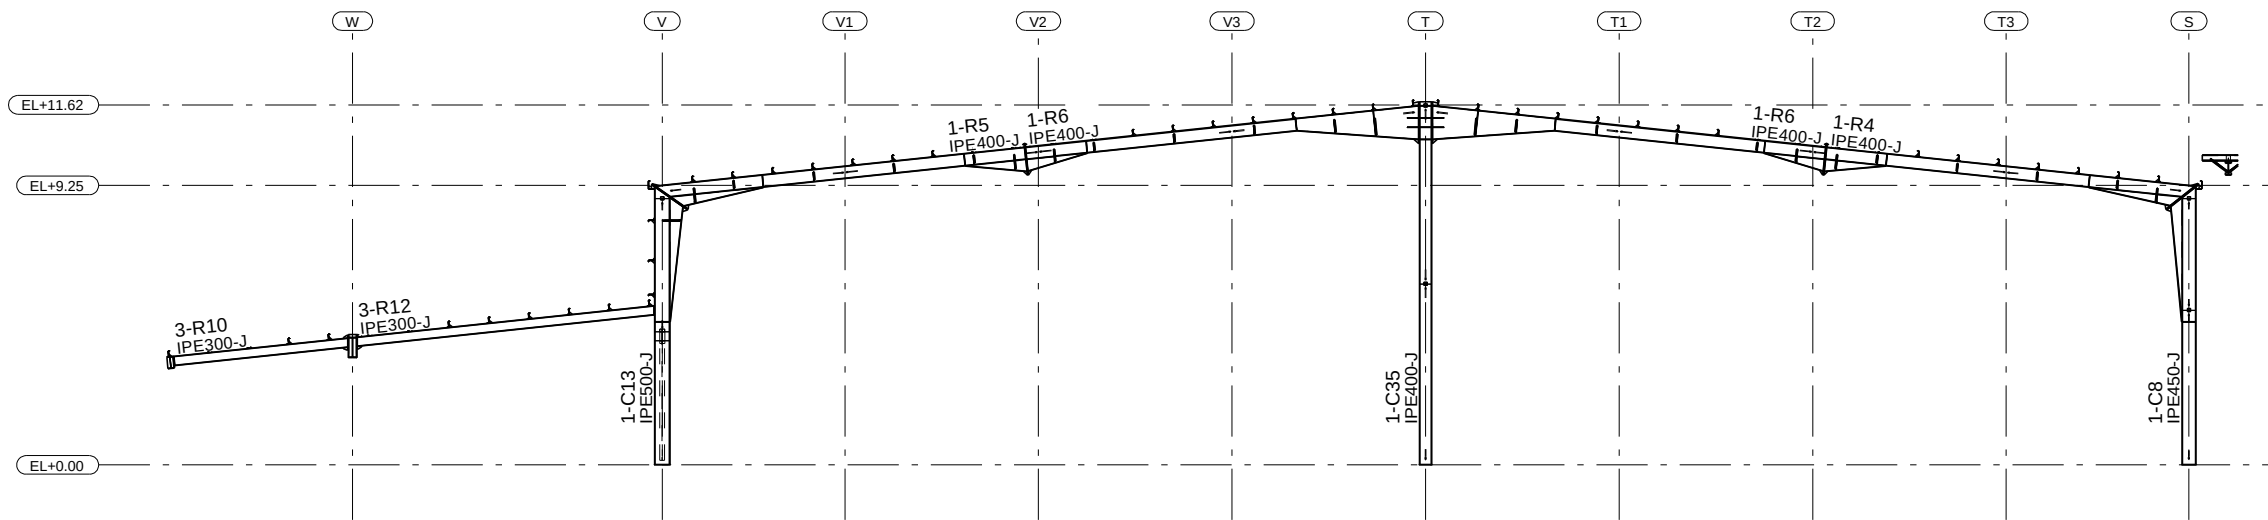


SECTION GRID 11


FD	12-06-2026	ISSUED FOR FABRICATION	A.A	H.H	
REV	DATE	DESCRIPTION	DRN	CHK	DSN
.....					
PROJECT NAME:					
SCHOOL PROJECT					
CONTRACTOR:					
--					
DRAWING TITLE:					
STEEL STRUCTURE					
SECTION GRID (11 + 12)					
CHECKED BY	A.A	SCALE			
DATE	A.A	SHEET NO.	E14		

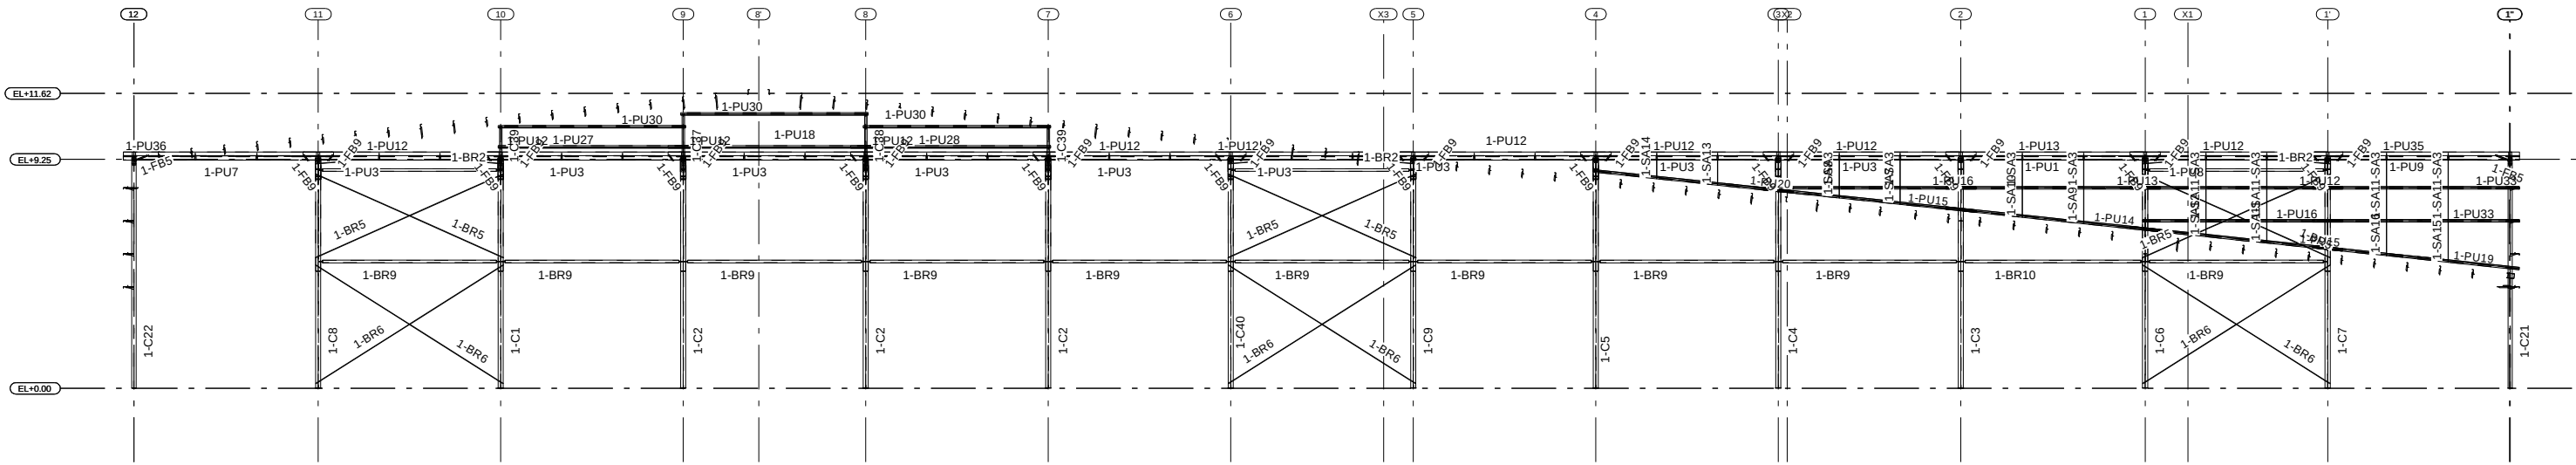

SECTION GRID S

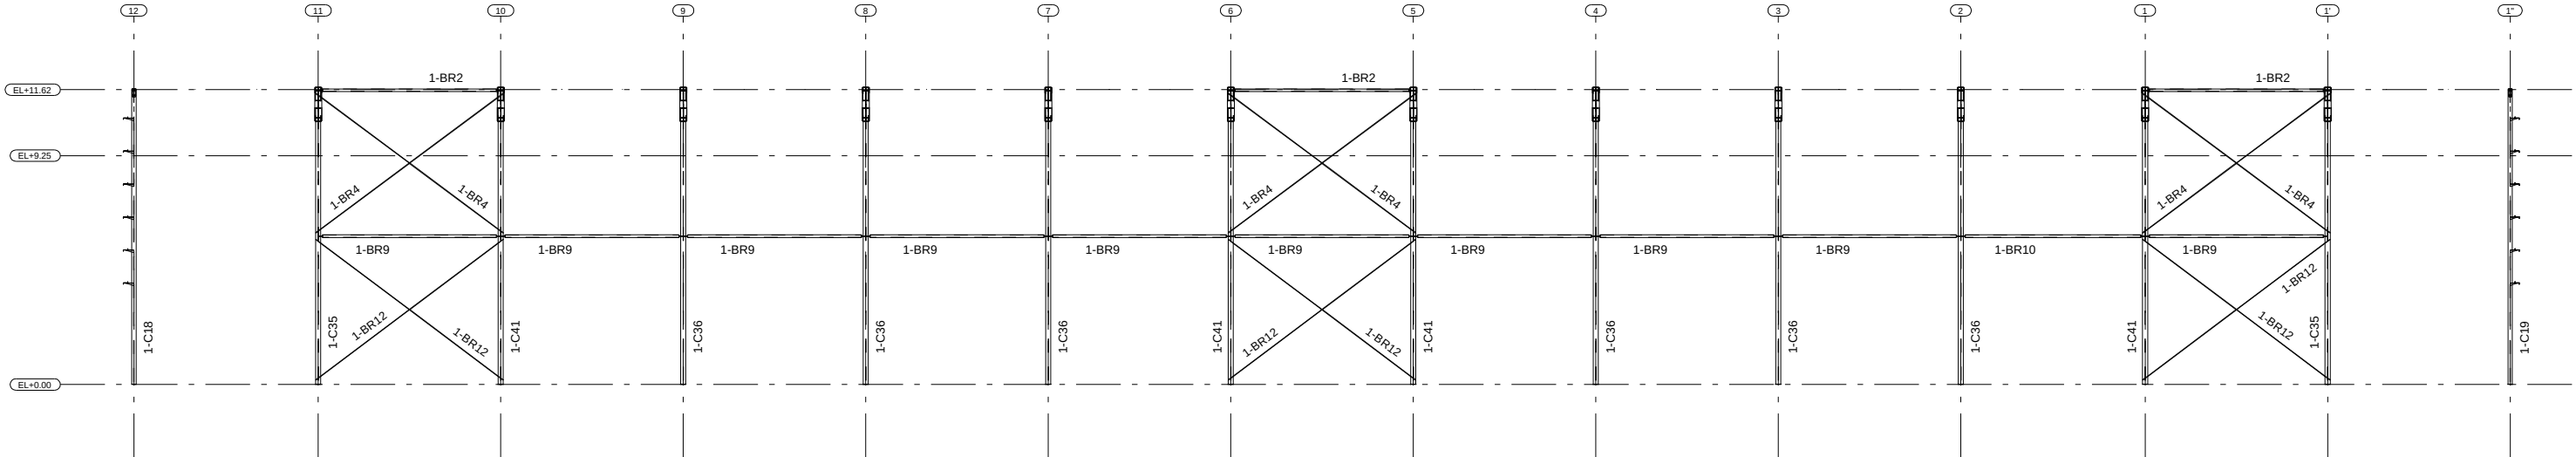


SECTION GRID T

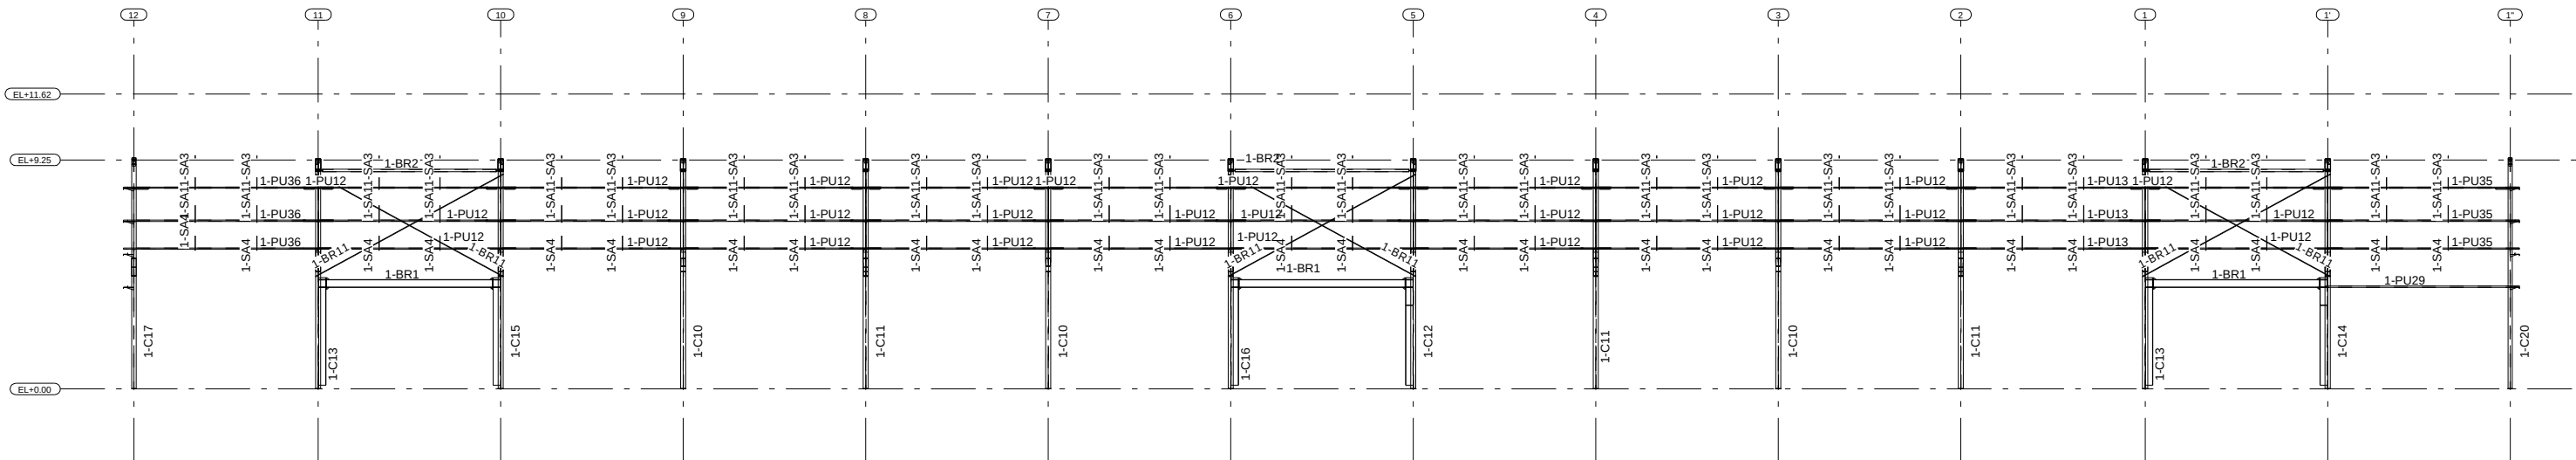


SECTION GRID V


12-08-2024		ISSUED FOR FABRICATION		A.A		H.H			
REV.	DATE	DESCRIPTION				DRN	CHK		
.....									
PROJECT NAME:									
SCHOOL PROJECT									
CONTRACTOR:									
--									
DRAWING TITLE:									
STEEL STRUCTURE									
SECTION GRID (V + T + S)									
CHECKED BY		A.A		SCALE					
DATE		A.A		SHEET NO.		E15			

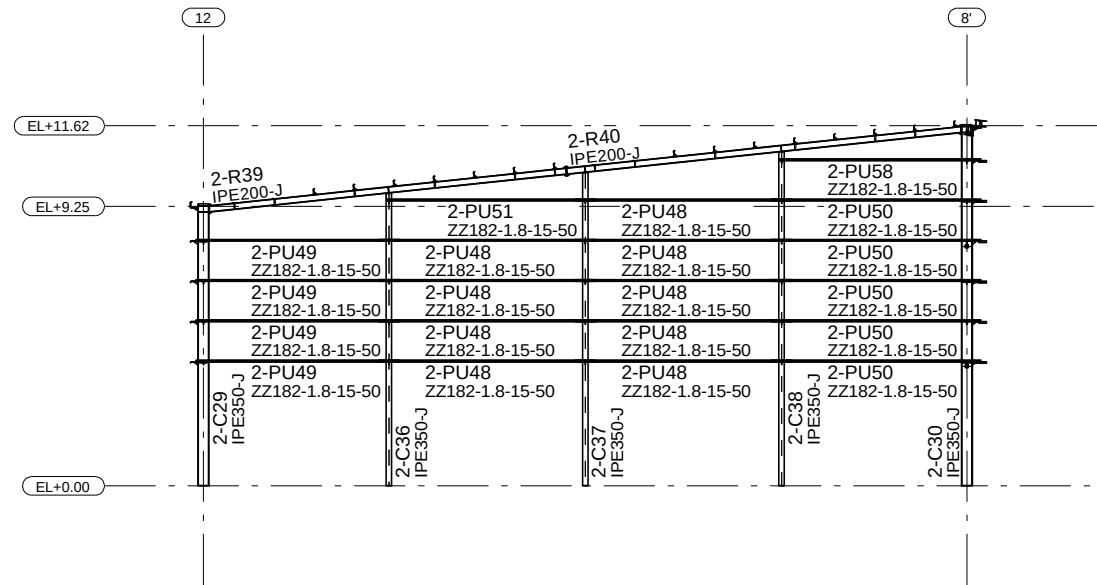

SECTION GRID A

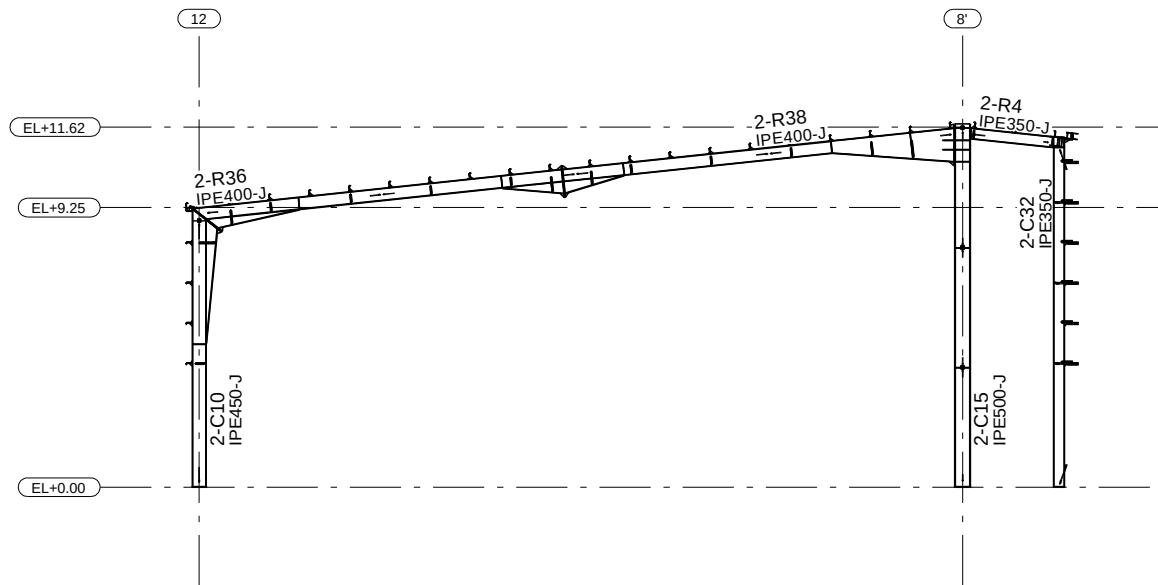


SECTION GRID B

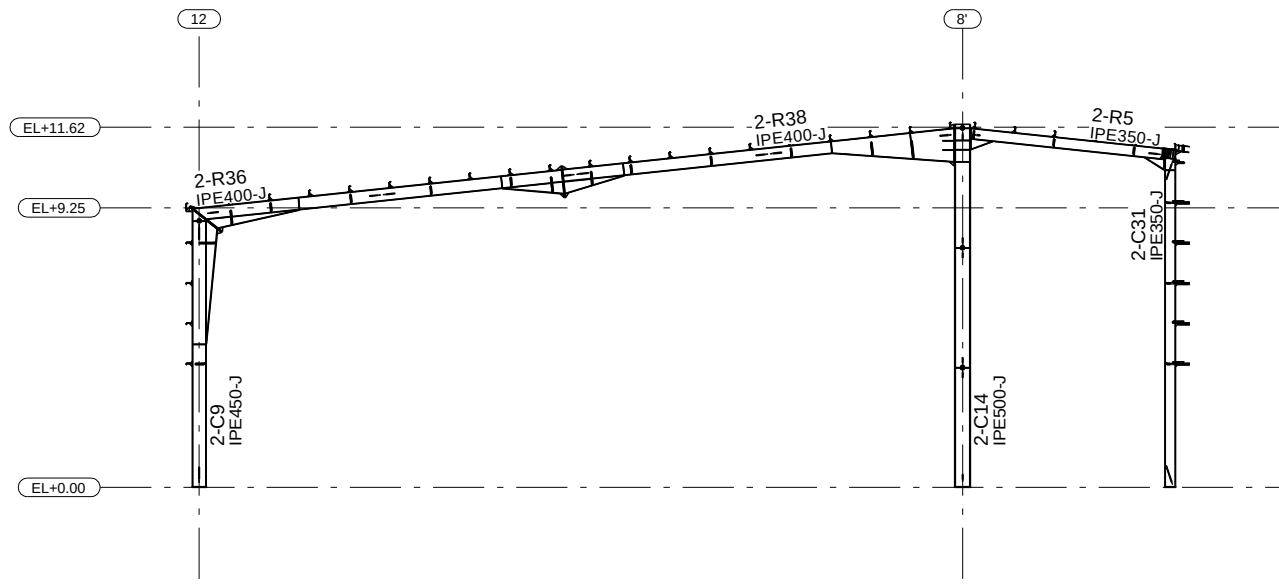


SECTION GRID C


FD	12-06-2026	ISSUED FOR FABRICATION	A.A	H.H	
REV	DATE	DESCRIPTION	DRN	CHK	DSN
.....					
PROJECT NAME:					
SCHOOL PROJECT					
CONTRACTOR:					
..					
DRAWING TITLE:					
STEEL STRUCTURE					
SECTION GRID (A + B + C)					
CHECKED BY	A.A	SCALE			
DATE	A.A	SHEET NO.	E16		

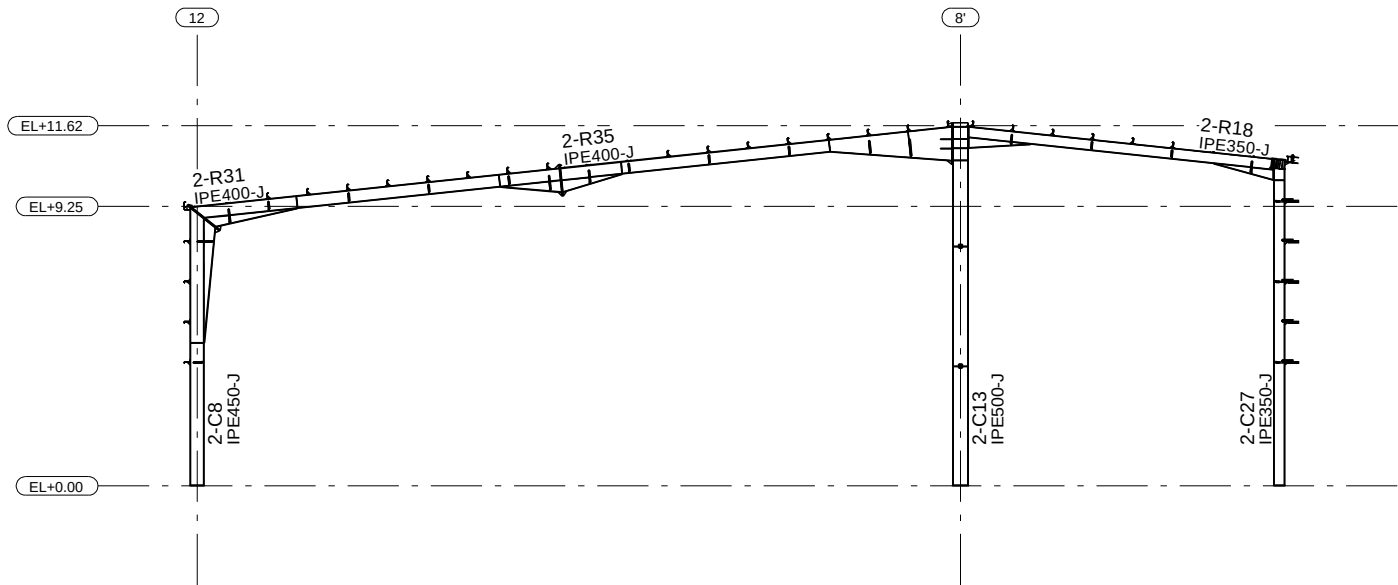

SECTION GRID D

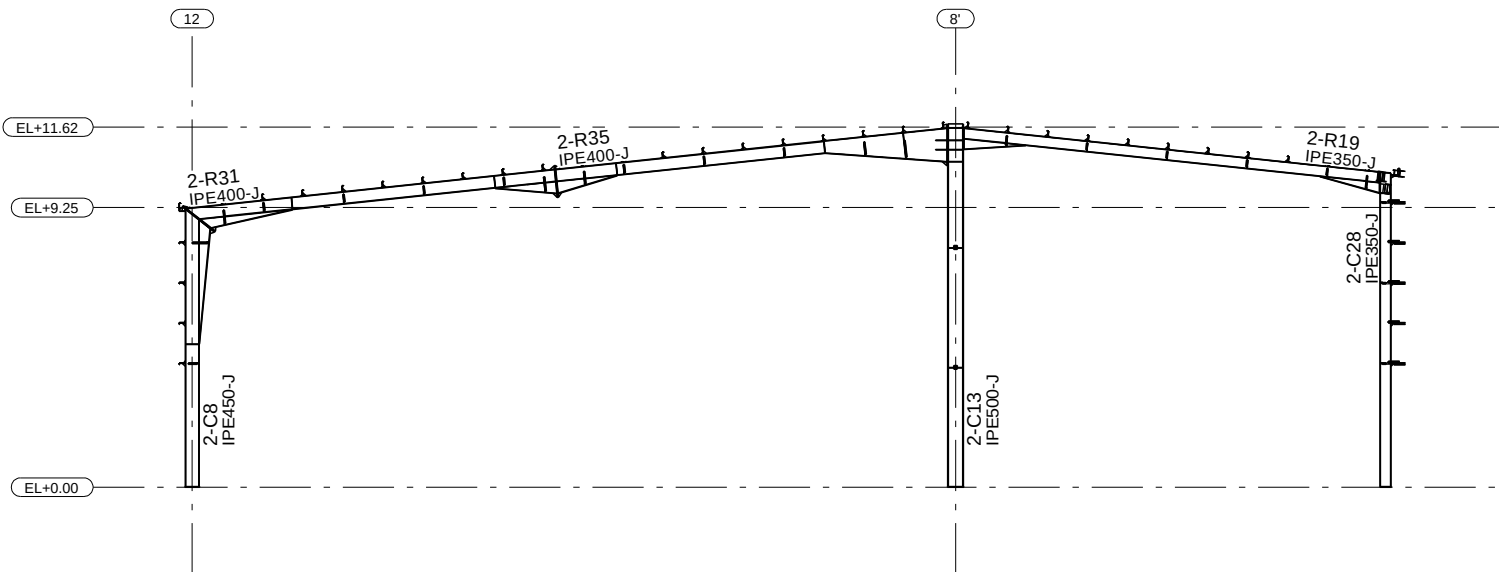


SECTION GRID E

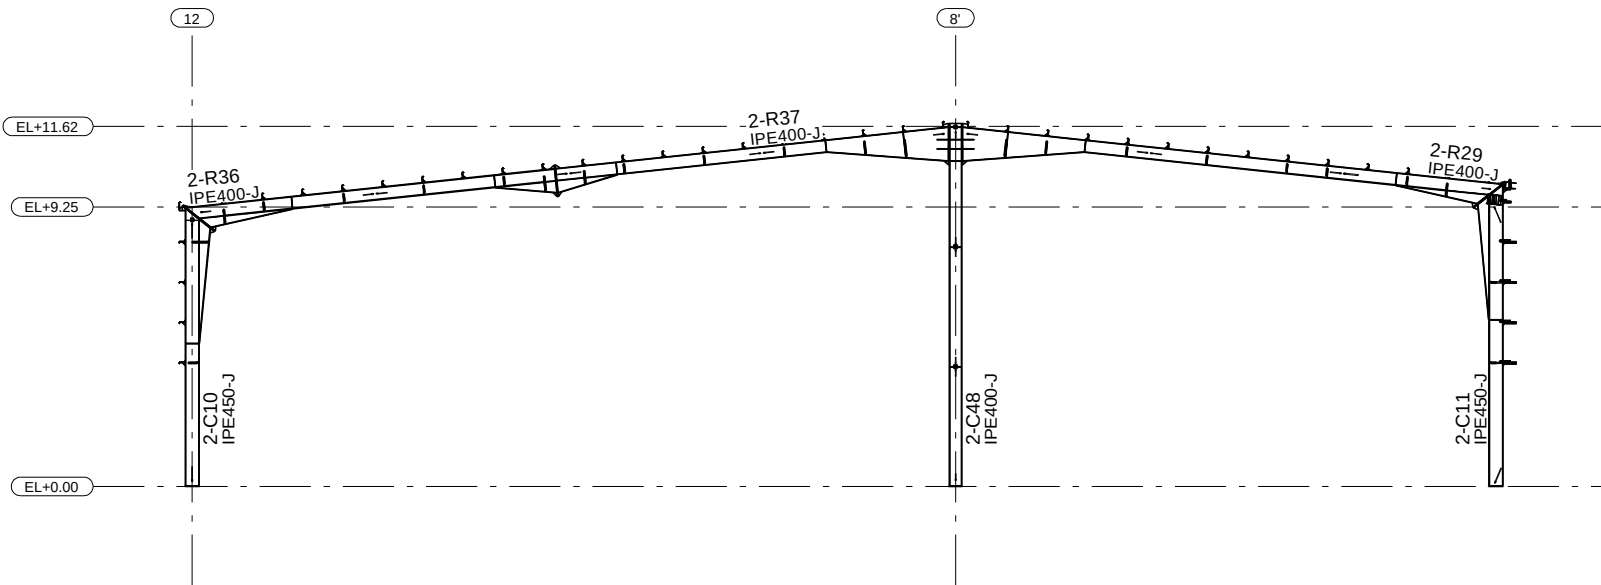


SECTION GRID F

FD	12-06-2026	ISSUED FOR FABRICATION			A.A	H.H	
REV.	DATE	DESCRIPTION			DRN	CHK	DSN


PROJECT NAME:							
SCHOOL PROJECT							
CONTRACTOR:							
--							
DRAWING TITLE:							
STEEL STRUCTURE							
SECTION GRID (D + E + F)							
CHECKED BY		A.A		SCALE			
DATE		A.A		SHEET NO.		E17	

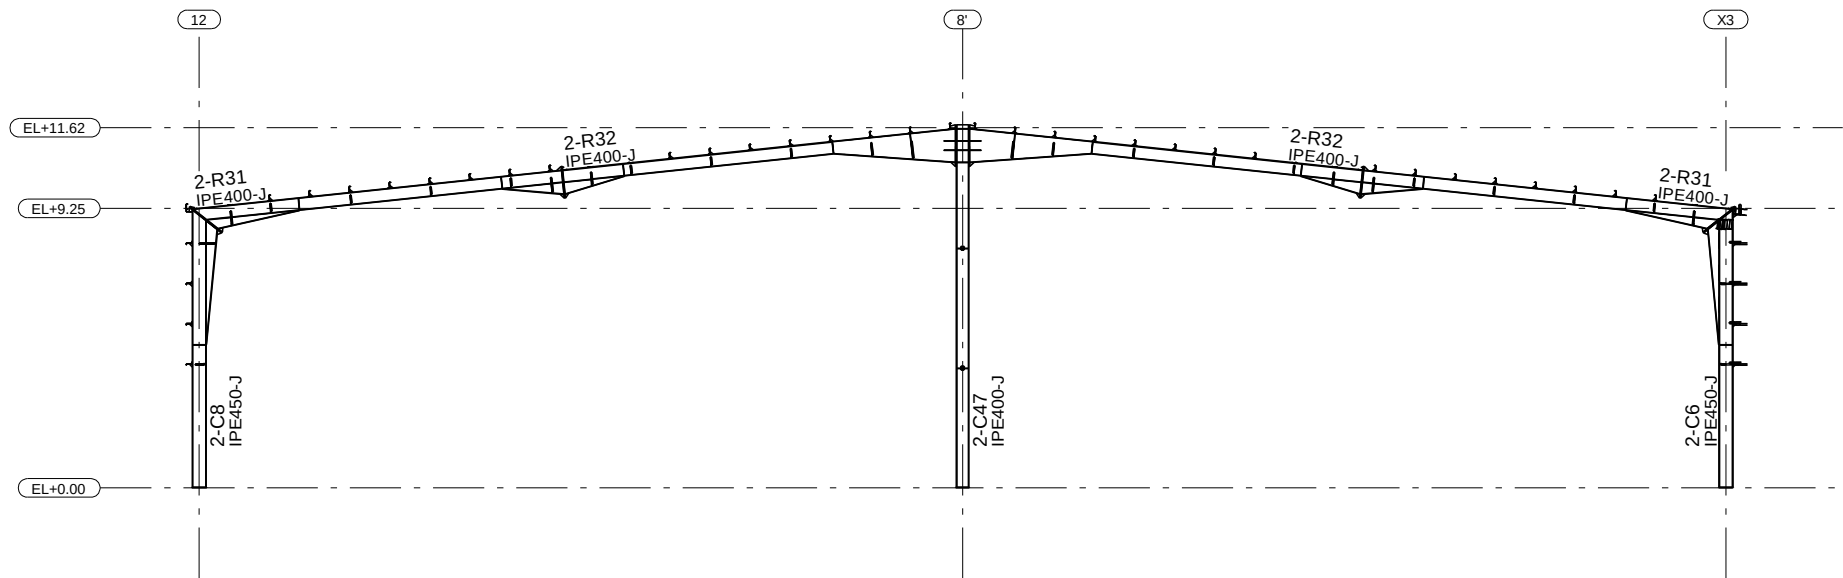

SECTION GRID G

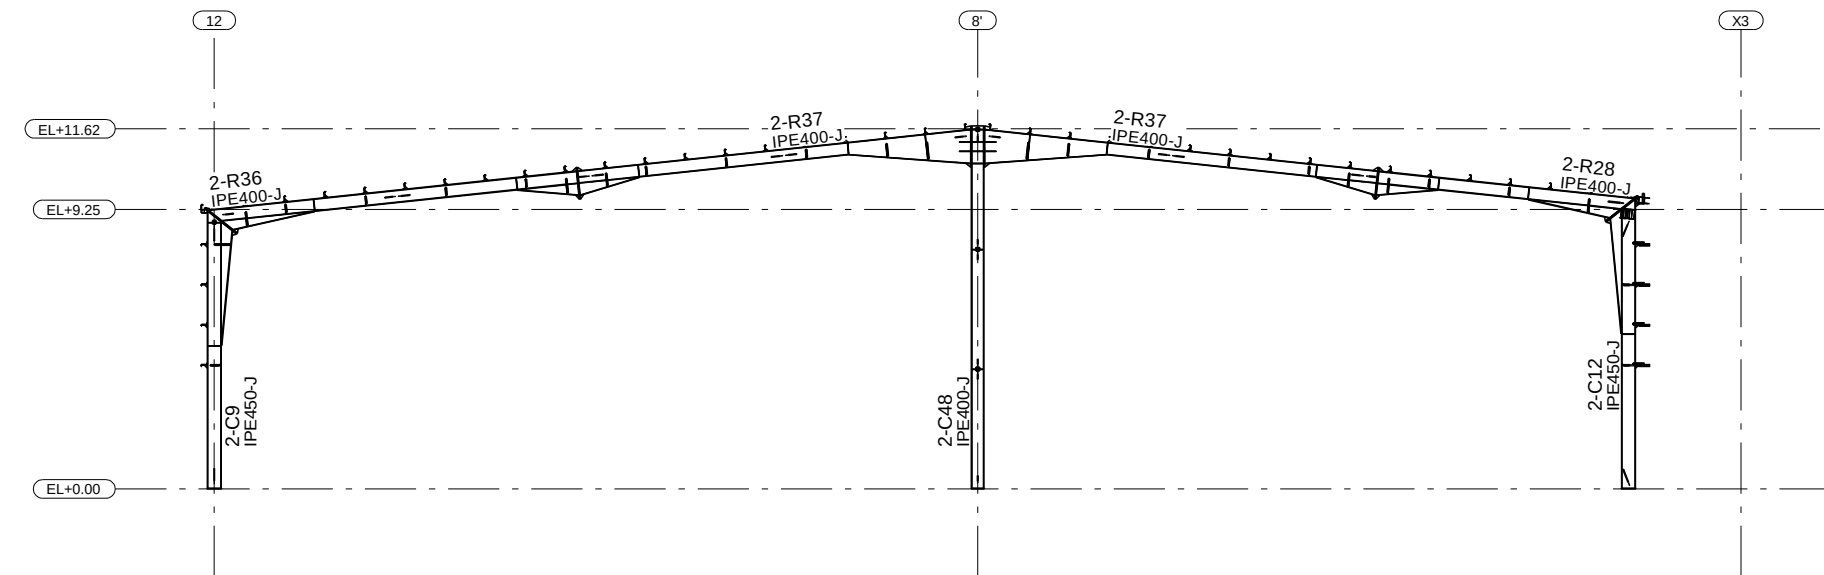


SECTION GRID G'

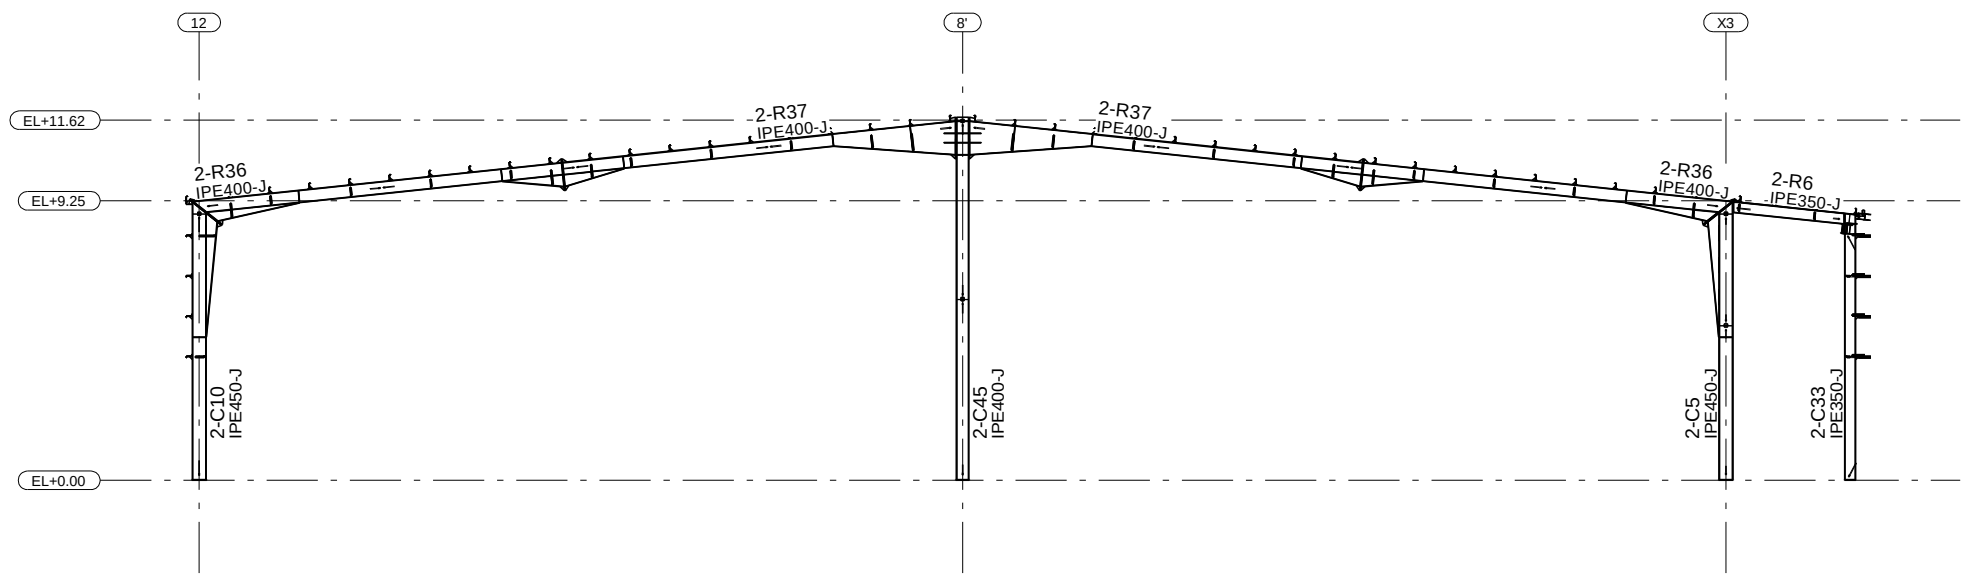


SECTION GRID H


FD	12-06-2026	ISSUED FOR FABRICATION	A.A	H.H	
REV	DATE	DESCRIPTION	DRN	CHK	DSN
.....					
PROJECT NAME:					
SCHOOL PROJECT					
CONTRACTOR:					
--					
DRAWING TITLE:					
STEEL STRUCTURE					
SECTION GRID (G + G' + H)					
CHECKED BY	A.A	SCALE			
DATE	A.A	SHEET NO.	E18		

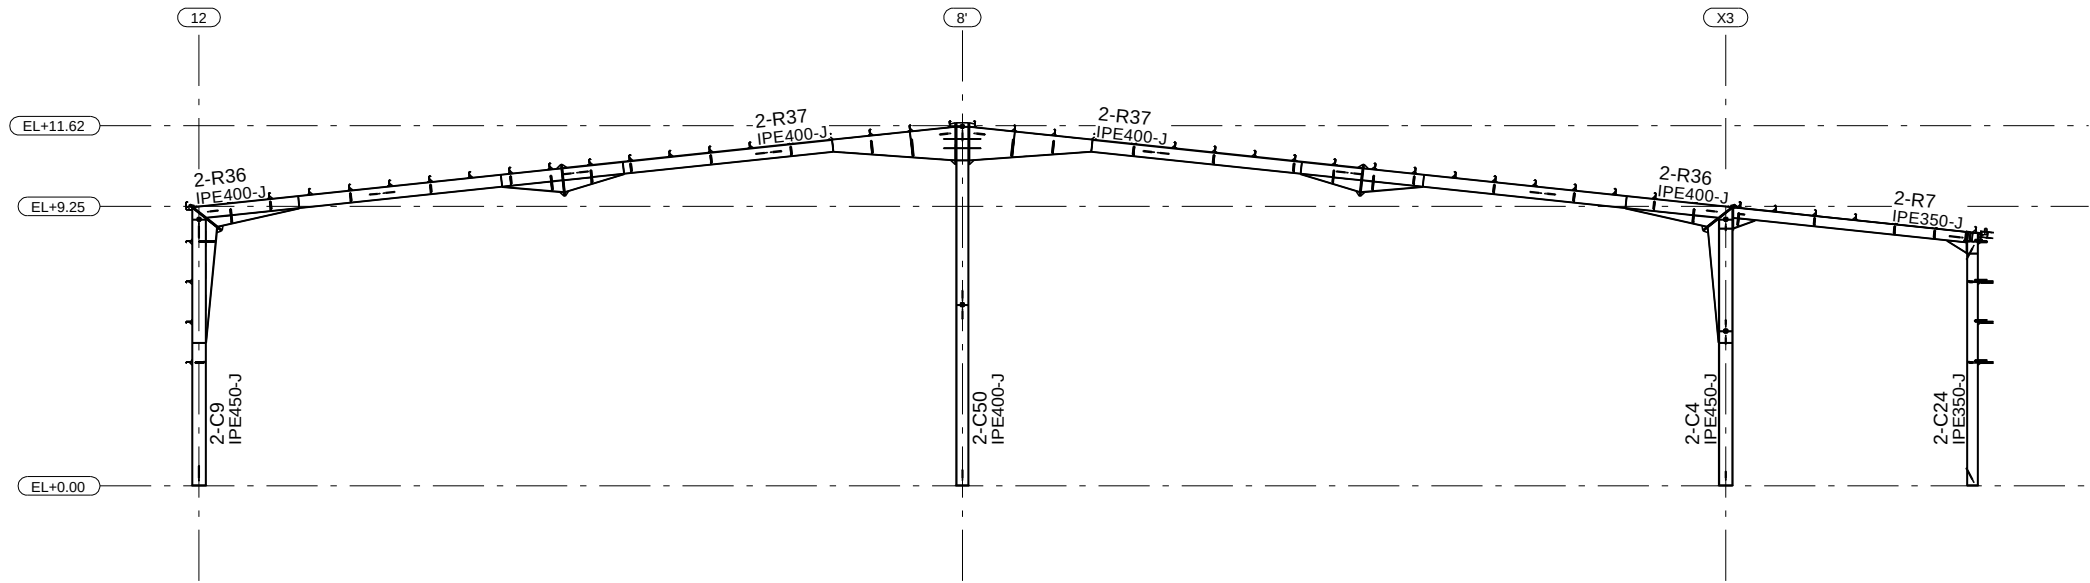

SECTION GRID J

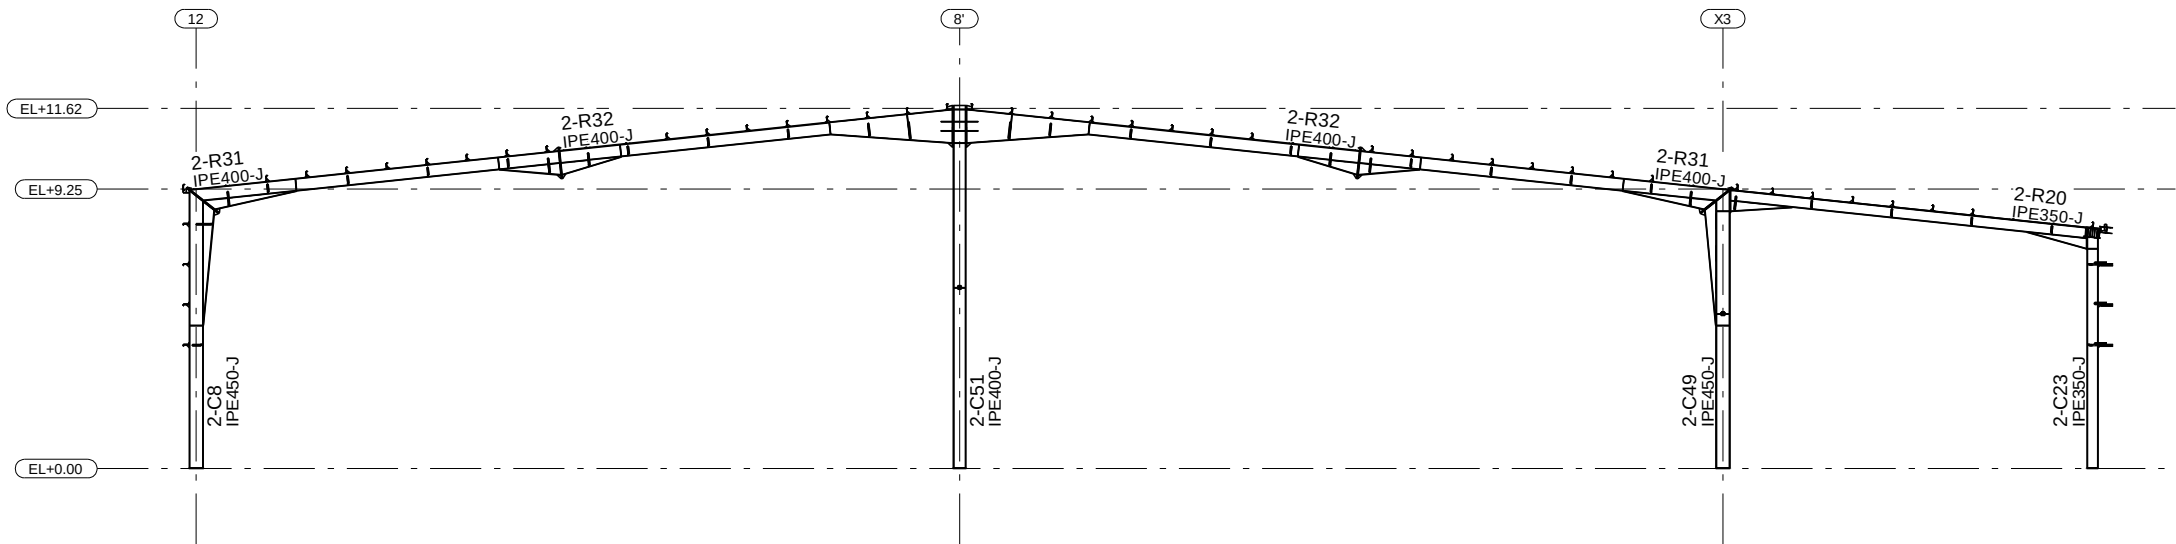


SECTION GRID K

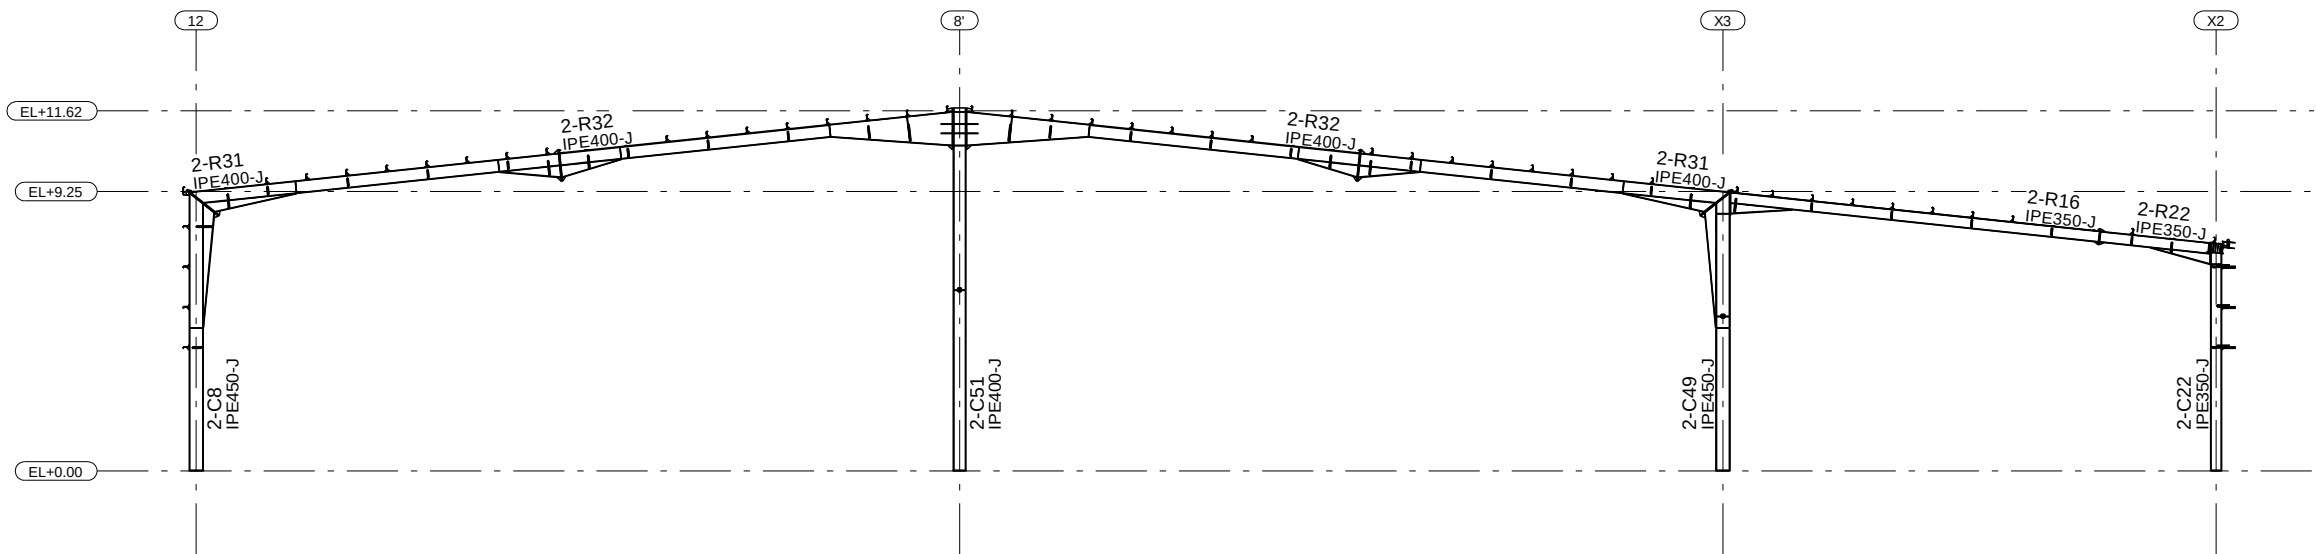


SECTION GRID L


FD	12-06-2026	ISSUED FOR FABRICATION	A.A	H.H	
REV	DATE	DESCRIPTION	DRN	CHK	DSN
.....					
PROJECT NAME:					
SCHOOL PROJECT					
CONTRACTOR:					
--					
DRAWING TITLE:					
STEEL STRUCTURE					
SECTION GRID (J + K + L)					
CHECKED BY	A.A	SCALE			
DATE	A.A	SHEET NO.	E19		

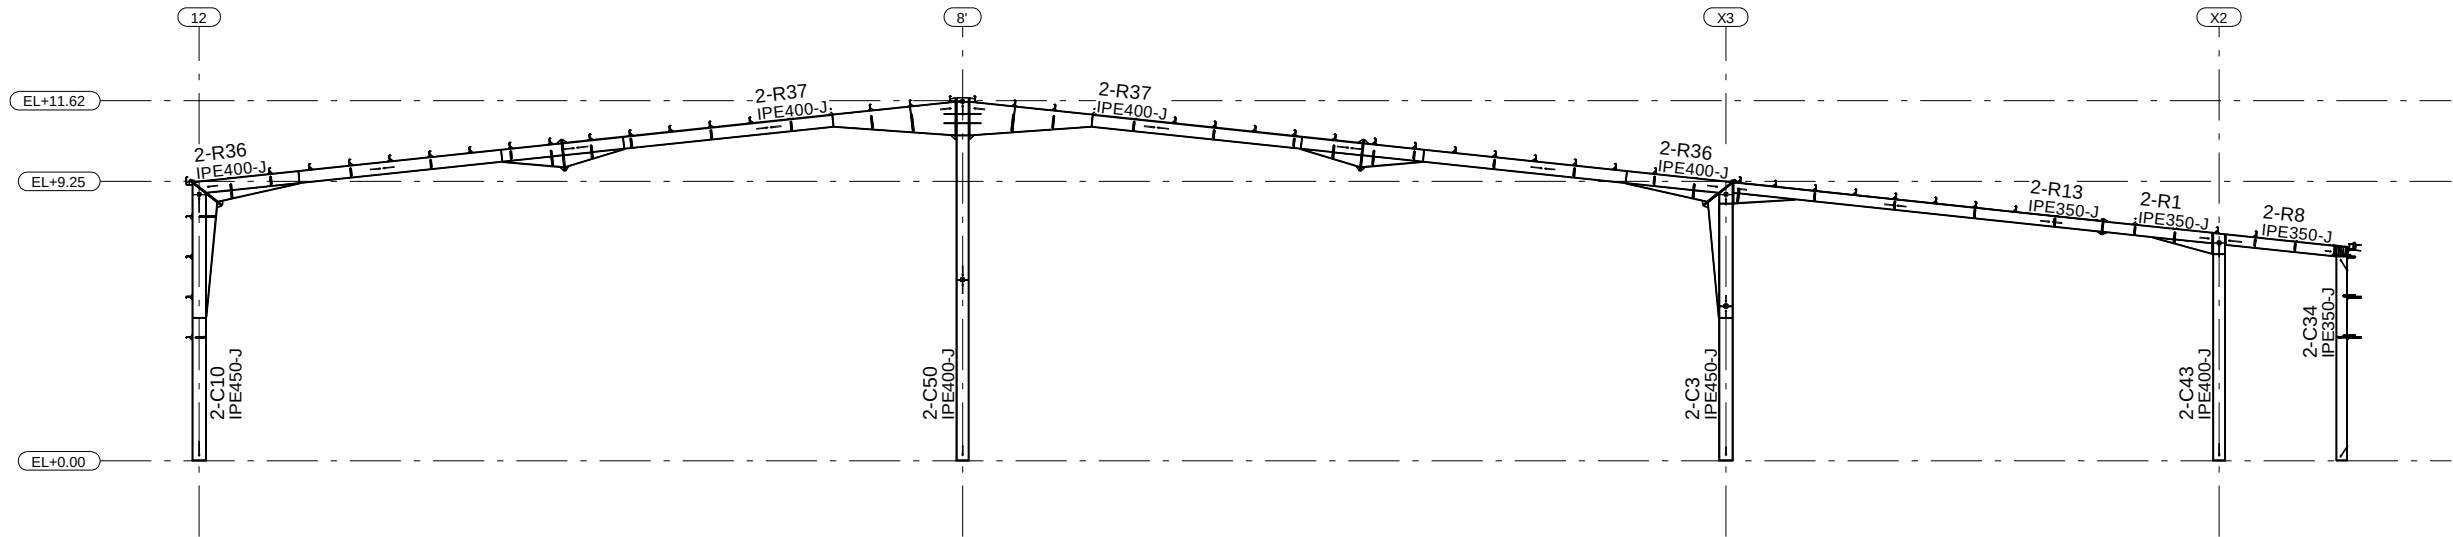

SECTION GRID M

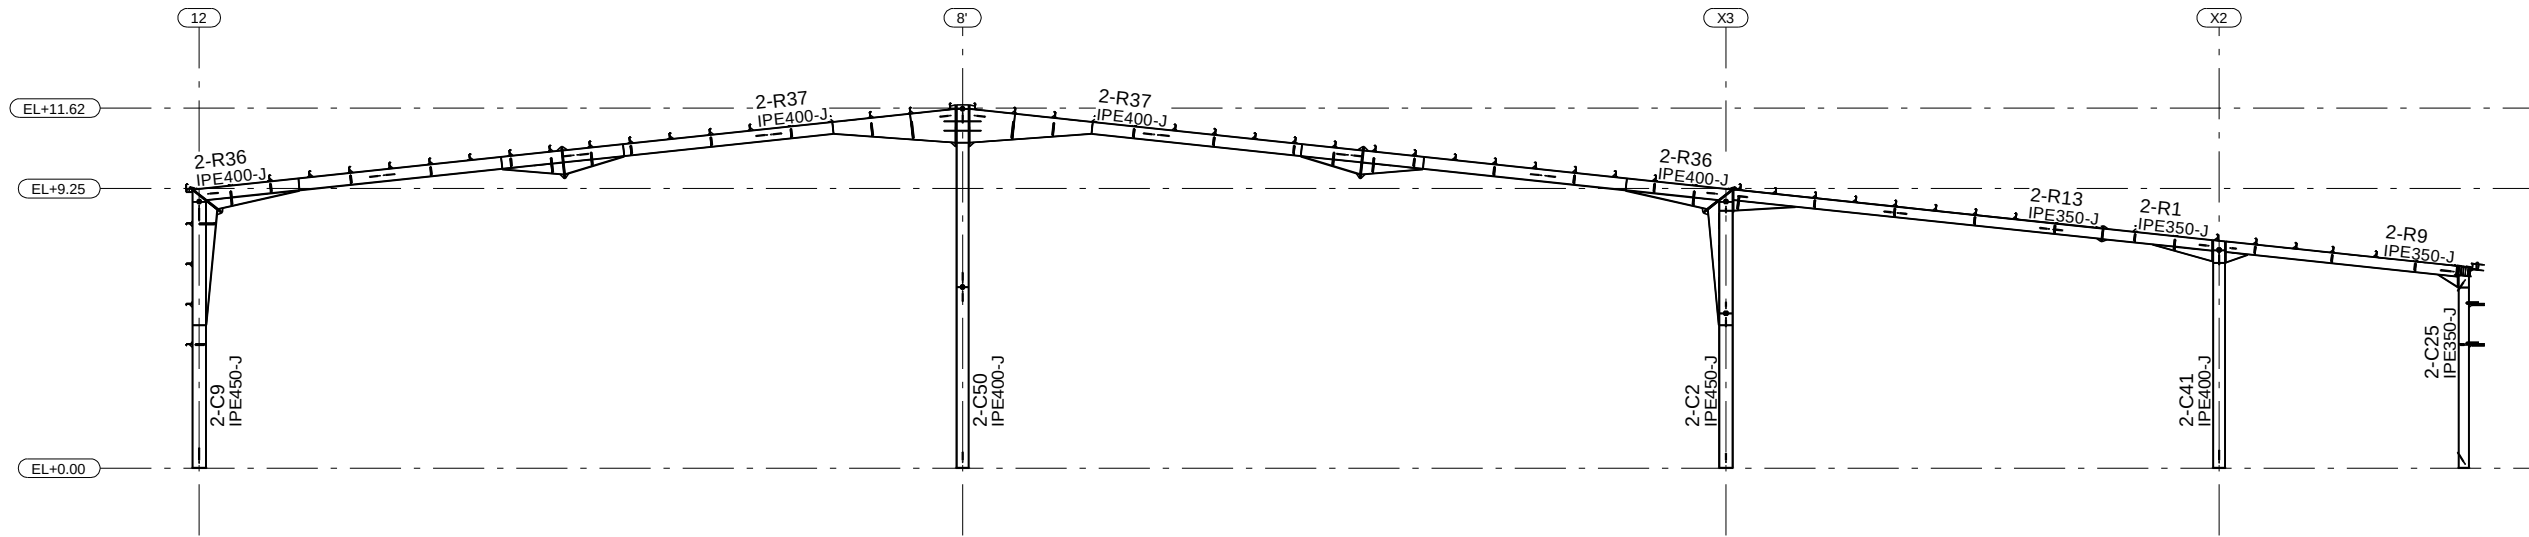


SECTION GRID N

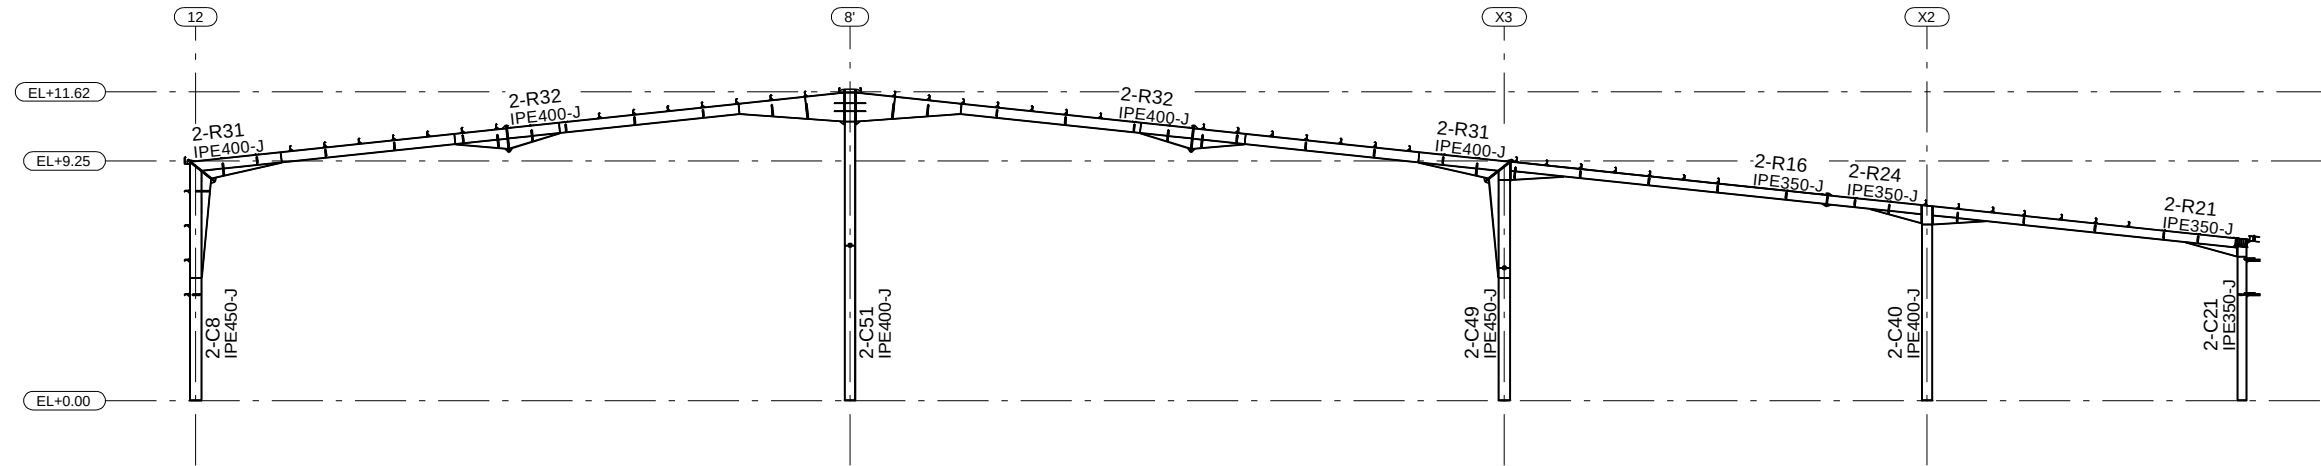


SECTION GRID P

FD	12-06-2026	ISSUED FOR FABRICATION	A.A	H.H	
REV	DATE	DESCRIPTION	DRN	CHK	DSN
PROJECT NAME:					
SCHOOL PROJECT					
CONTRACTOR:					


DRAWING TITLE:					
STEEL STRUCTURE					
SECTION GRID (M + N + P)					
CHECKED BY	A.A	SCALE			
DATE	A.A	SHEET NO.	E20		

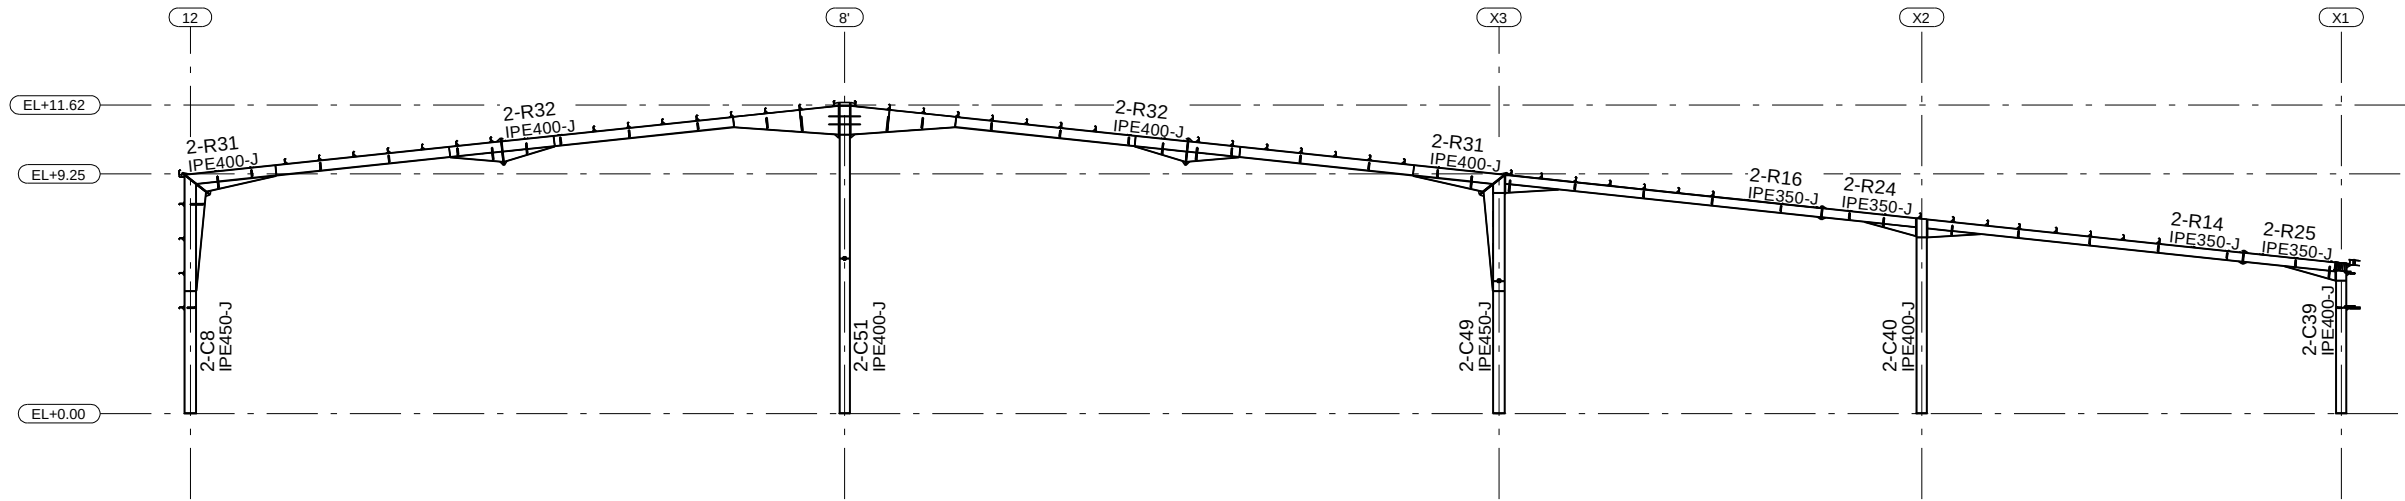

SECTION GRID Q

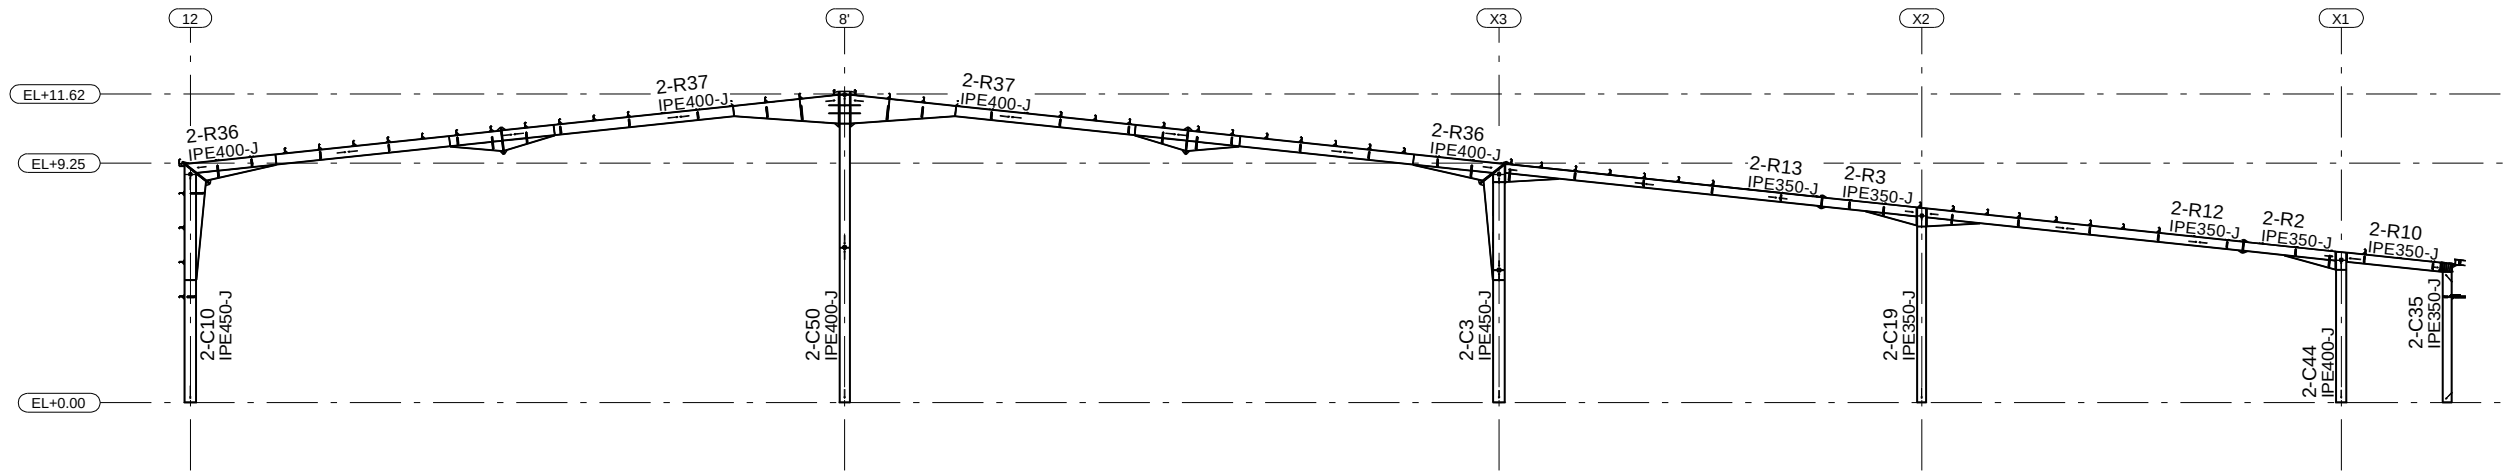


SECTION GRID R

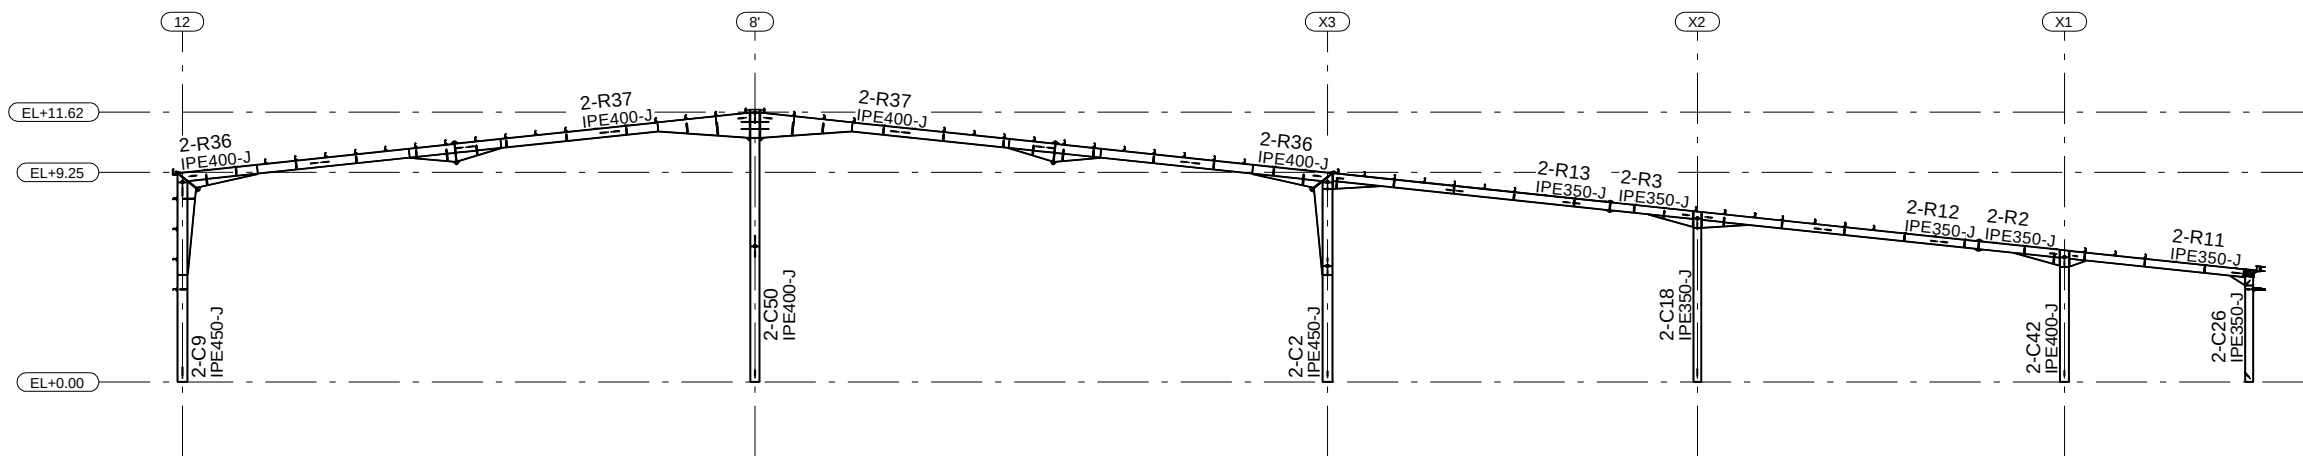

SECTION GRID R'


FD	12-06-2026	ISSUED FOR FABRICATION	A.A	H.H	
REV	DATE	DESCRIPTION	DRN	CHK	DSN
.....					
PROJECT NAME:					
SCHOOL PROJECT					
CONTRACTOR:					
--					
DRAWING TITLE:					
STEEL STRUCTURE					
SECTION GRID (Q +R + R')					
CHECKED BY	A.A	SCALE			
DATE	A.A	SHEET NO.			E21

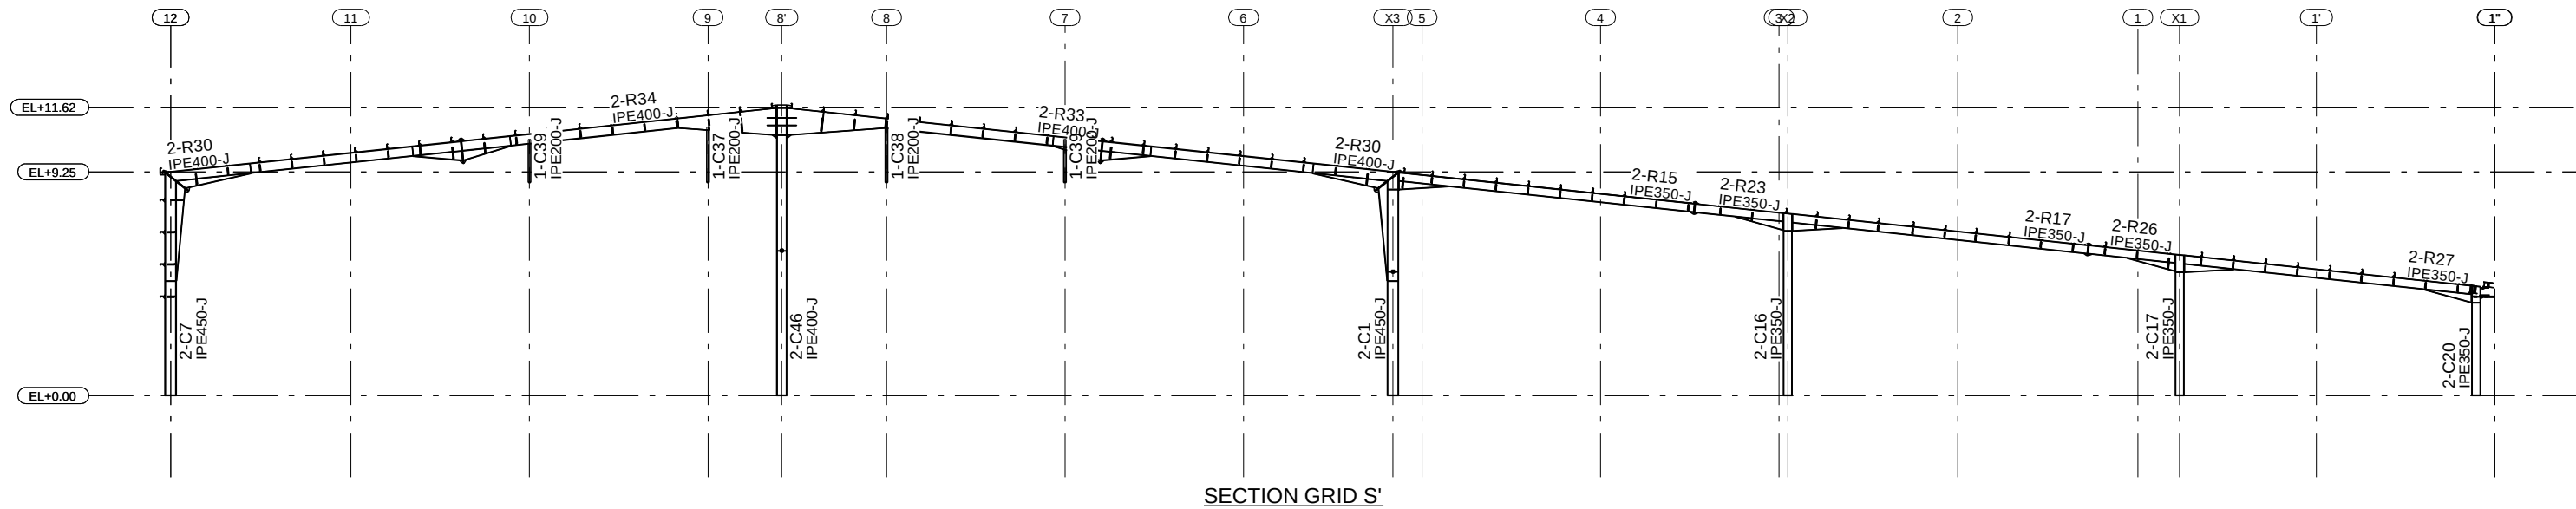


SECTION GRID S'

FD	12-06-2026	ISSUED FOR FABRICATION			A.A	H.H	
REV.	DATE	DESCRIPTION			DRN	CHK	DSN

PROJECT NAME:							
SCHOOL PROJECT							
CONTRACTOR:							
--							
DRAWING TITLE:							
STEEL STRUCTURE							
SECTION GRID (S')							
CHECKED BY		A.A		SCALE			
DATE		A.A		SHEET NO.		E22	

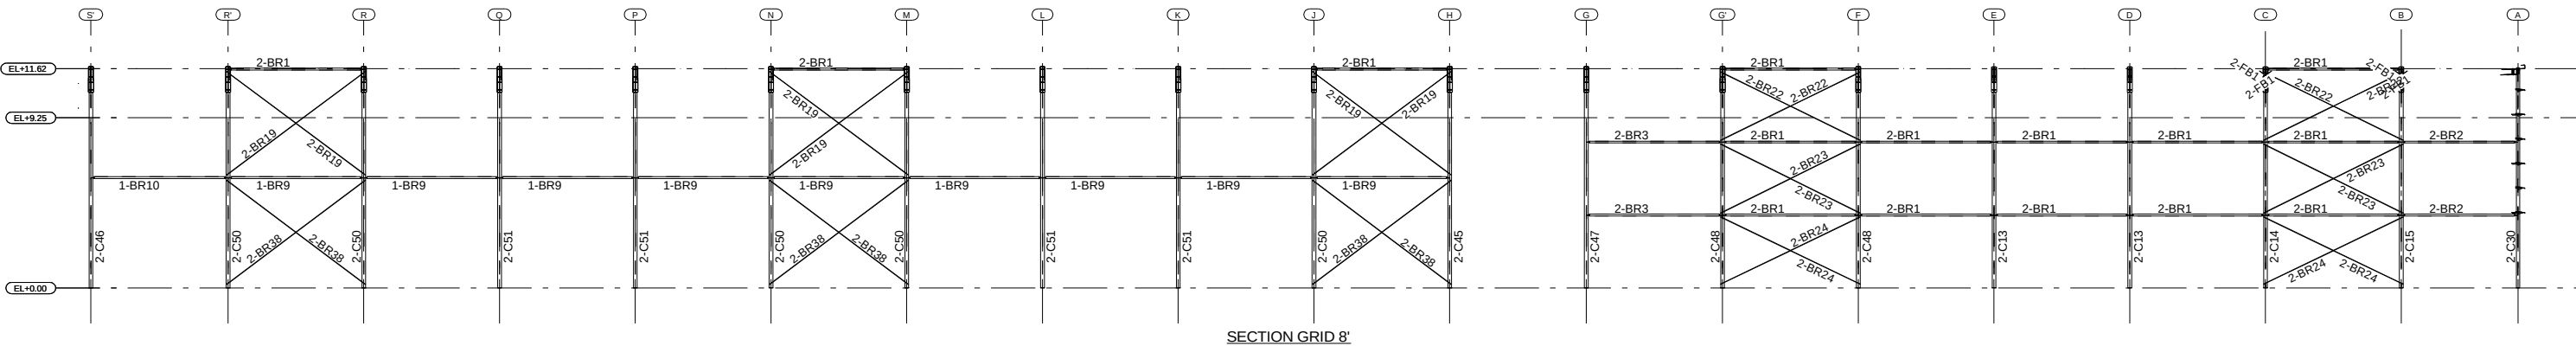


SECTION GRID 8'

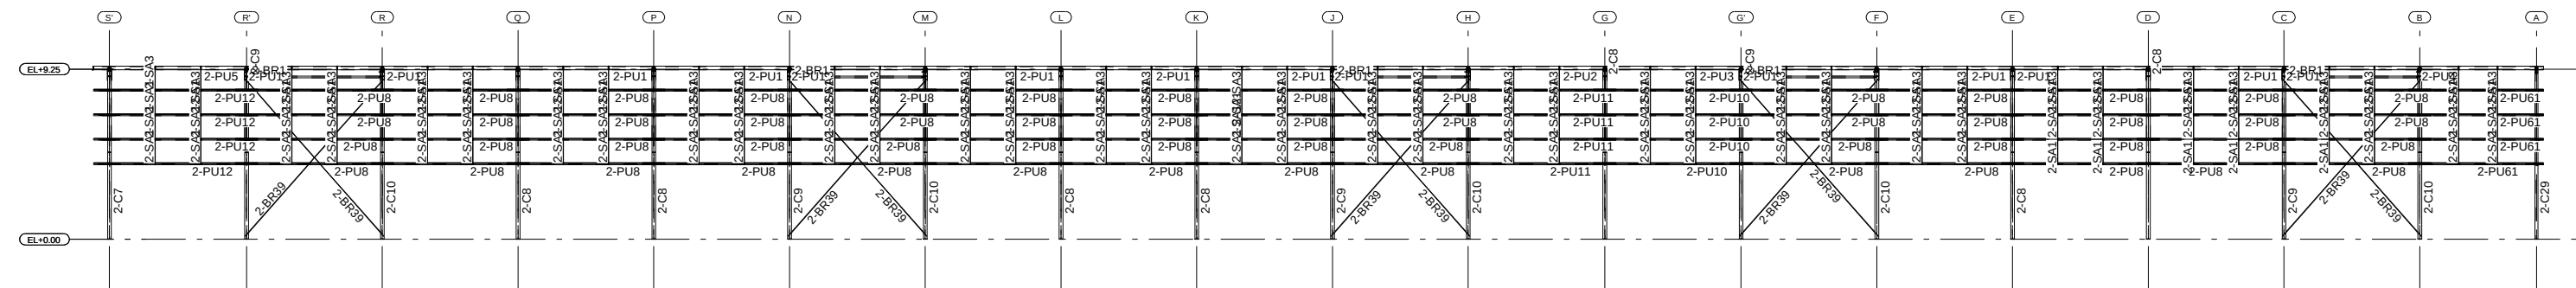


SECTION GRID 12

12-08-2024		ISSUED FOR FABRICATION		A.A.		H.H.	
REV.	DATE	DESCRIPTION		DRN	CHK	ENR	


PROJECT NAME:							
SCHOOL PROJECT							
CONTRACTOR:							
..							
DRAWING TITLE:							
STEEL STRUCTURE							
SECTION GRID (12 + 8')							
CHECKED BY		A.A.		SCALE			
DATE		A.A.		SHEET NO.		E23	

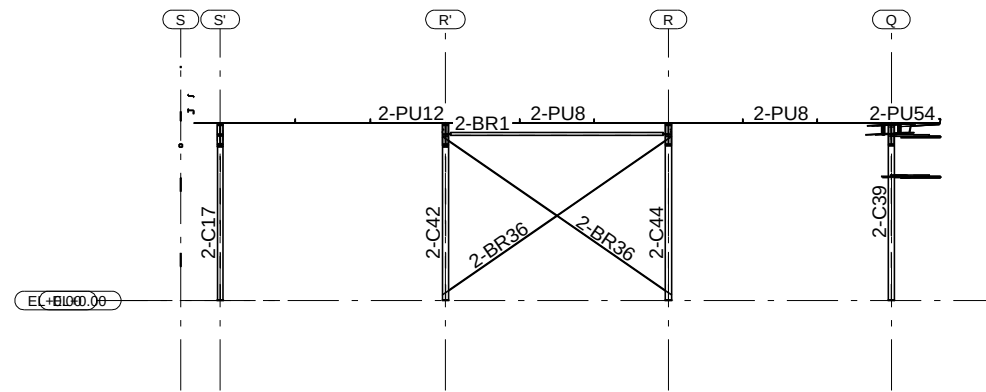

SECTION GRID X1

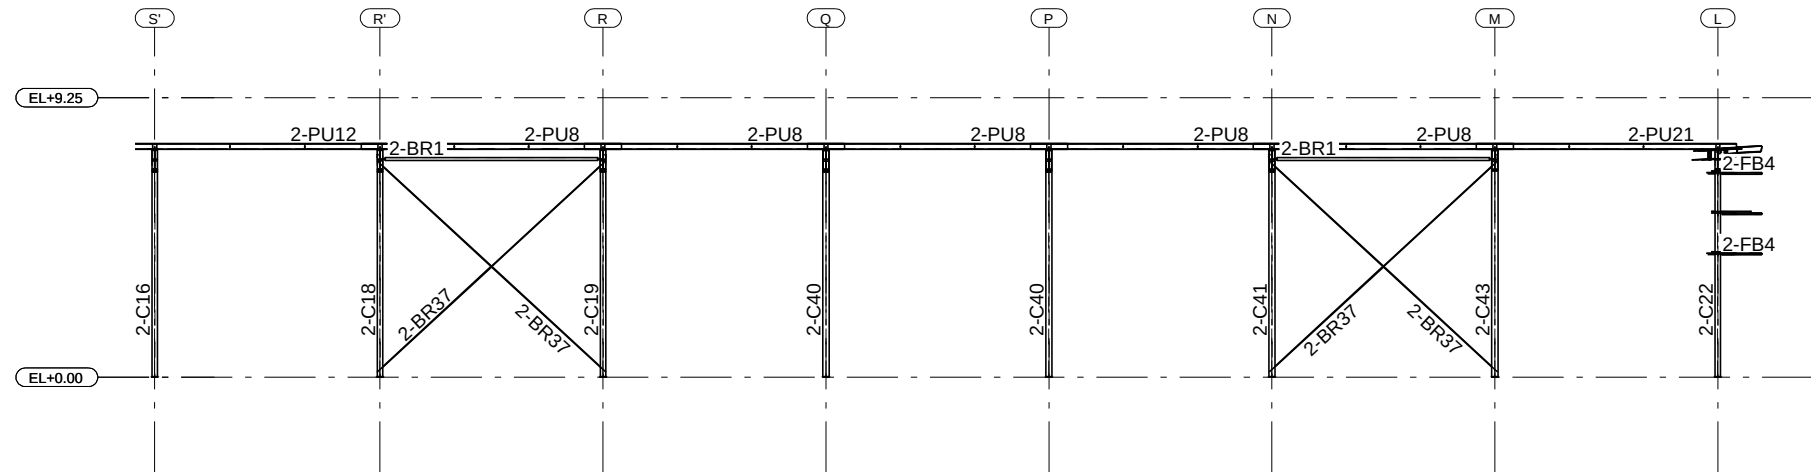


SECTION GRID X2

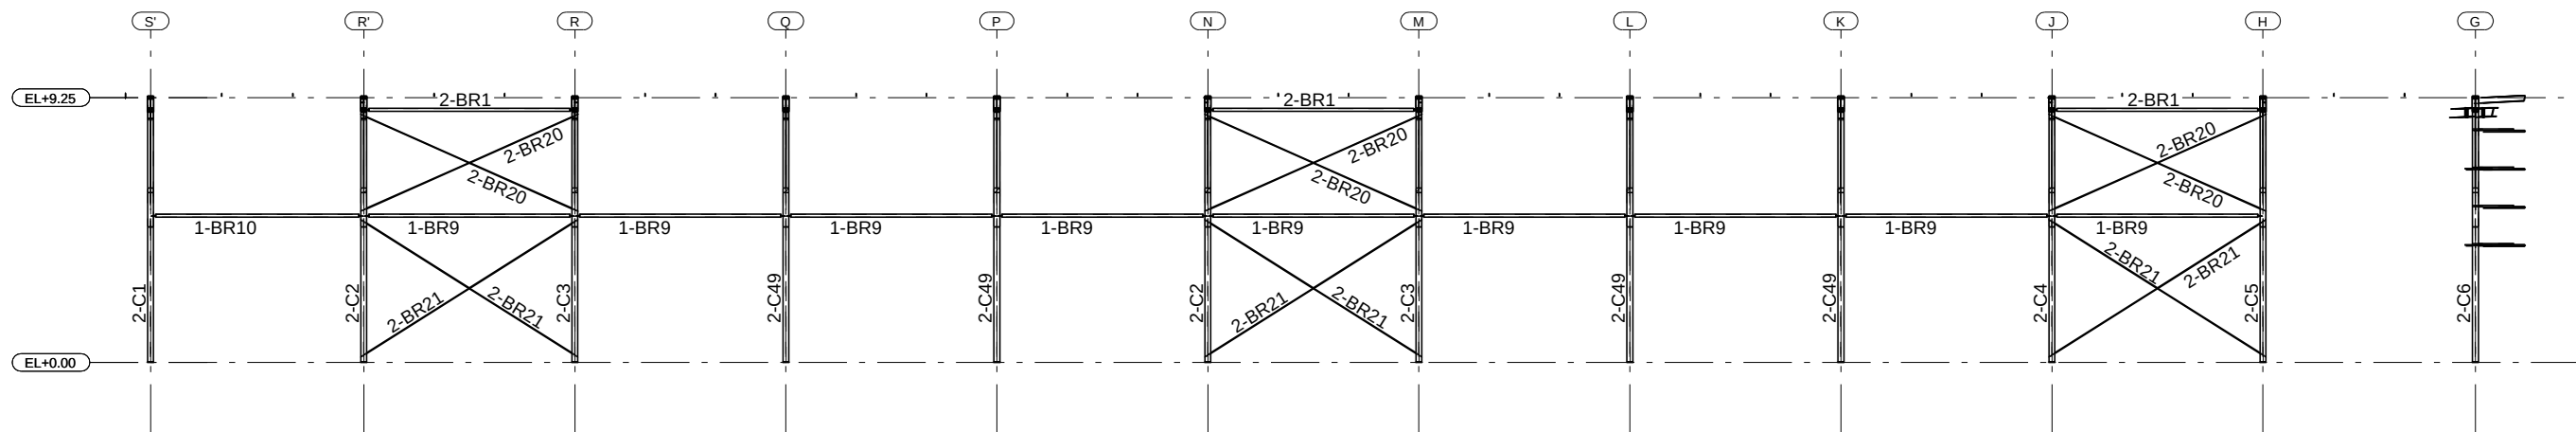

SECTION GRID X3

FD	12-06-2026	ISSUED FOR FABRICATION	A.A	H.H	
REV	DATE	DESCRIPTION	DRN	CHK	DSN
.....					
PROJECT NAME:					
SCHOOL PROJECT					
CONTRACTOR:					
--					
DRAWING TITLE:					
STEEL STRUCTURE					
SECTION GRID (X1 + X2 + X3)					
CHECKED BY	A.A	SCALE			
DATE	A.A	SHEET NO.	E24		

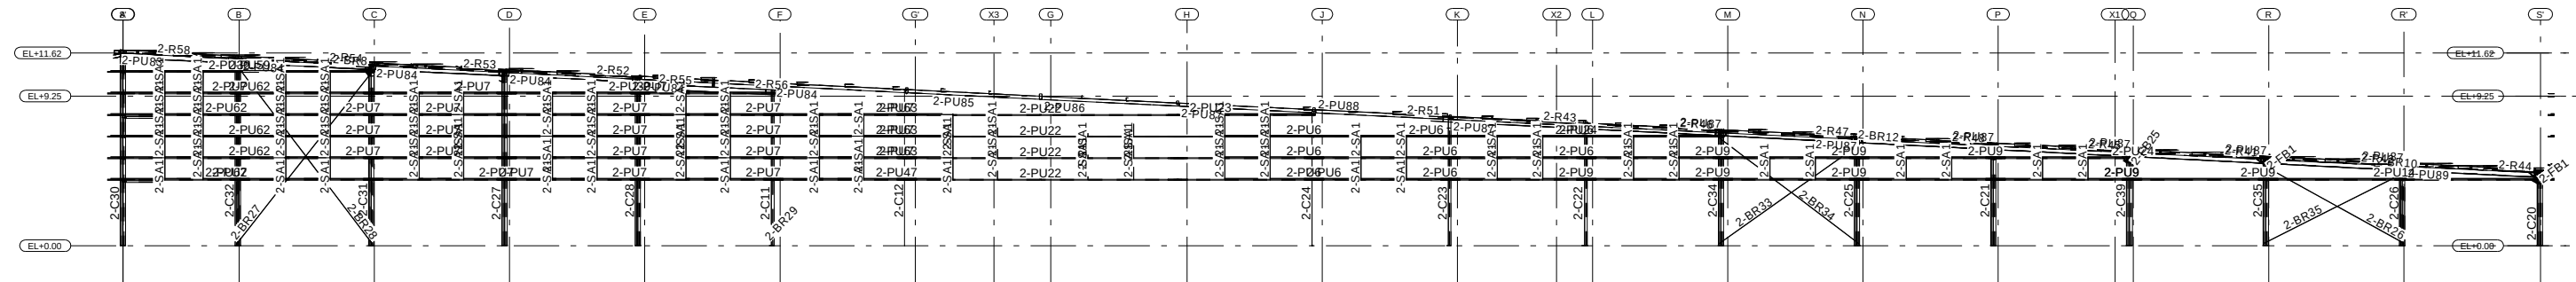

View 03 (SECTION - 1)

		12-08-2024	ISSUED FOR FABRICATION		A.A.	H.H.	
REV.	DATE	DESCRIPTION		DRN	CHK	DSN	
.....							
PROJECT NAME:							
SCHOOL PROJECT							
CONTRACTOR:							
..							
DRAWING TITLE:							
STEEL STRUCTURE							
SECTION GRID							
CHECKED BY		A.A.	SCALE				
DATE		A.A.	SHEET NO.		E25		