



| BILL OF MATERIALS |       |          | ASSEMBLY POS. 2-BR1 |          | No. Required 26  |             | POS. NO. 546 |      |
|-------------------|-------|----------|---------------------|----------|------------------|-------------|--------------|------|
| POS. NO.          | QTYN. | Profile  | LENGTH (mm)         | Material | UNIT weight kg/m | weight (kg) |              | NOTE |
|                   |       |          |                     |          |                  | QTY.        | TOTAL        |      |
| 546               | 1     | RHS100*4 | 6852.0              | S235JR   | 12.00            | 82.22       | 82.22        |      |
| 399               | 2     | PL10*120 | 120.0               | S235JR   | 1.13             | 1.13        | 2.26         |      |
| 415               | 2     | PL10*120 | 130.0               | S235JR   | 1.22             | 1.22        | 2.45         |      |
| Total Weight      |       |          |                     |          |                  | 87.0        | (kg)         |      |

| BOLT, NUT & WASHERS MATERIAL LIST |              |       |                     |             |
|-----------------------------------|--------------|-------|---------------------|-------------|
| EACH                              | REMARK       |       | UNIT WEIGHT KG/1000 | WEIGHT (KG) |
| 8                                 | M16x50 BOLTS | GR8.8 | 111.1               | 0.89        |
| 8                                 | M16 NUTS     | GR8.8 | 32.9                | 0.26        |
| 8                                 | M16 WASHERS  | GR8.8 | 11.0                | 0.18        |
| Total weight                      |              |       |                     | 1.33 (KG)   |

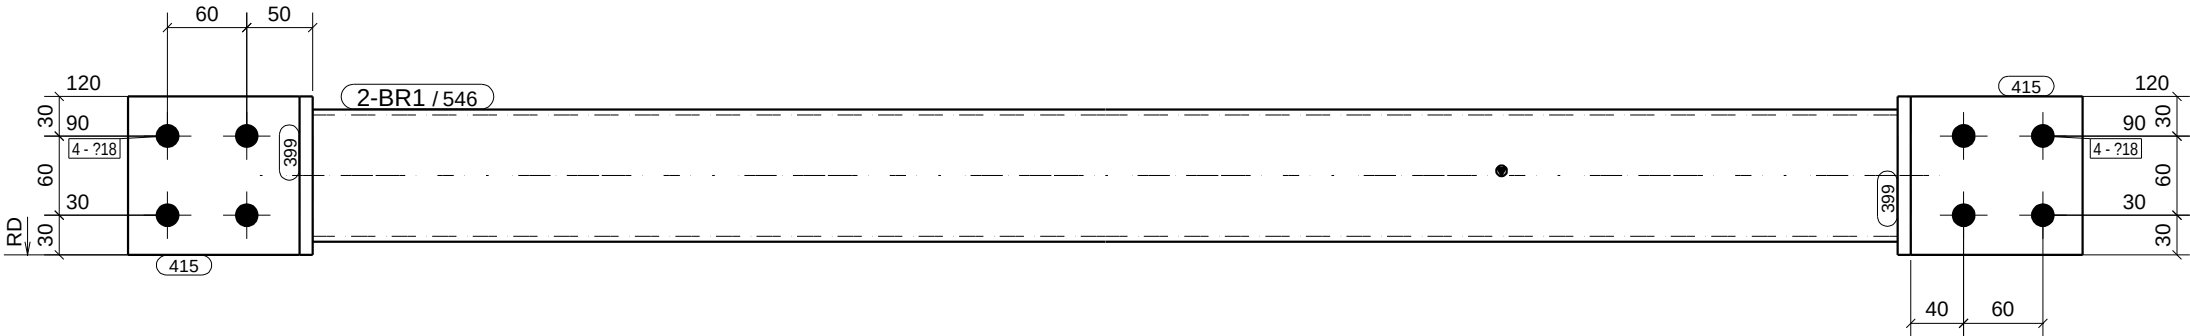

TOP VIEW

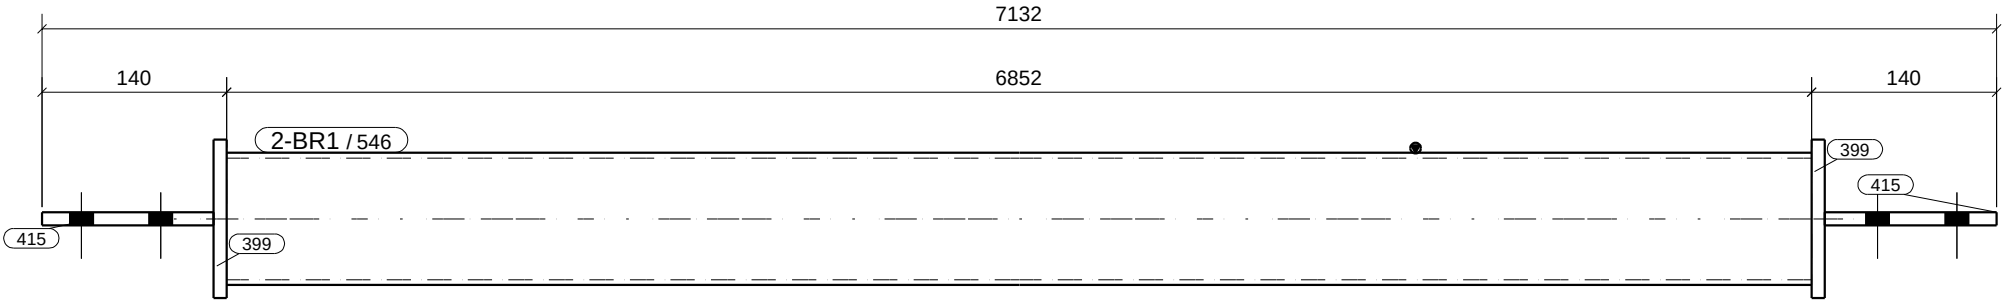

FRONT VIEW

- GENERAL NOTES:
1. ALL HOLES ARE 22 mm DIA (UON).
  2. ALL DIMENSIONS ARE IN MM (UON).
  3. UNLESS OTHERWISE NOTED ALL FILLET WELD SIZE SHALL BE 7mm FILLET CONTINUOUS(UON)
  4. RD DENOTES BASE LINE = 00

| REV.                                    | DATE | DESCRIPTION | DRN       | CHK | DSN |
|-----------------------------------------|------|-------------|-----------|-----|-----|
| -----<br>-----<br>-----                 |      |             |           |     |     |
| PROJECT NAME:<br><br>MADAR GROUP JORDAN |      |             |           |     |     |
| CONTRACTOR:<br><br>-----                |      |             |           |     |     |
| DRAWING TITLE:<br><br>BRACING<br>2-BR1  |      |             |           |     |     |
| CHECKED BY                              |      | A.A         | SCALE     |     |     |
| DATE                                    |      | A.A         | SHEET NO. |     |     |

MARK: 2-BR1  
QTY: 26  
DESC.: RHS100\*4