


| BILL OF MATERIALS |       |         | ASSEMBLY POS. 2-FB18 |          | No. Required     | 2           | POS. NO. 595 |      |
|-------------------|-------|---------|----------------------|----------|------------------|-------------|--------------|------|
| POS. NO.          | QTYN. | Profile | LENGTH (mm)          | Material | UNIT weight kg/m | weight (kg) |              | NOTE |
|                   |       |         |                      |          |                  | QTY.        | TOTAL        |      |
| 595               | 1     | L40*2   | 935.1                | S235JR   | 1.22             | 1.15        | 1.15         |      |
| Total Weight      |       |         |                      |          |                  | 1.1         | (kg)         |      |

| BOLT, NUT & WASHERS MATERIAL LIST |        |         |       |                     |             |
|-----------------------------------|--------|---------|-------|---------------------|-------------|
| EACH                              | REMARK |         |       | UNIT WEIGHT KG/1000 | WEIGHT (KG) |
| 1                                 | M12x30 | BOLTS   | GR8.8 | 40.2                | 0.04        |
| 1                                 | M12    | NUTS    | GR8.8 | 15.9                | 0.02        |
| 1                                 | M12    | WASHERS | GR8.8 | 5.9                 | 0.01        |
| Total weight                      |        |         |       |                     | 0.06 (KG)   |

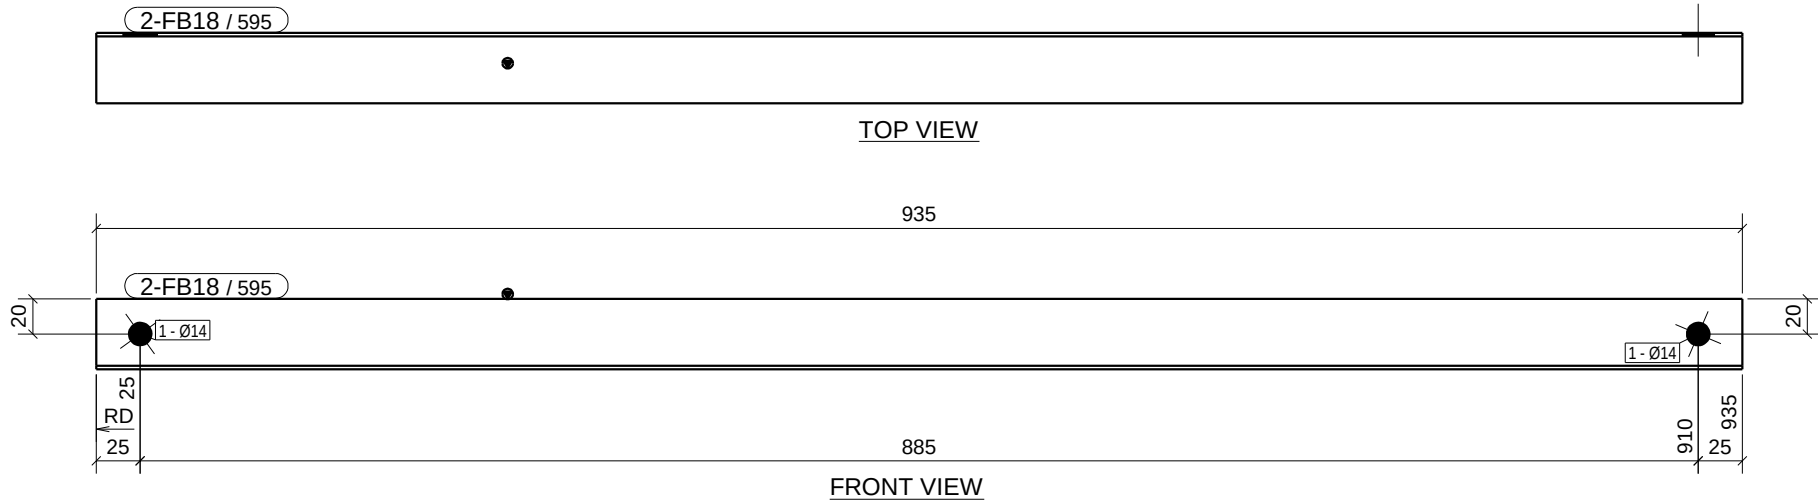

- GENERAL NOTES:
- 1. ALL HOLES ARE 22 mm DIA (UON).
  - 2. ALL DIMENSIONS ARE IN MM (UON).
  - 3. UNLESS OTHERWISE NOTED ALL FILLET WELD SIZE SHALL BE 7mm FILLET CONTINUOUS(UON)
  - 4. RD DENOTES BASE LINE = 00

| REV.                                         | DATE | DESCRIPTION | DRN       | CHK | DSN |
|----------------------------------------------|------|-------------|-----------|-----|-----|
| -----<br>-----<br>-----                      |      |             |           |     |     |
| PROJECT NAME:<br><br>MADAR GROUP JORDAN      |      |             |           |     |     |
| CONTRACTOR:<br><br>-----                     |      |             |           |     |     |
| DRAWING TITLE:<br><br>FLANGE.BRACE<br>2-FB18 |      |             |           |     |     |
| CHECKED BY                                   |      | A.A         | SCALE     |     |     |
| DATE                                         |      | A.A         | SHEET NO. |     |     |

MARK: 2-FB18  
QTY: 2  
DESC.: L40\*2