


| BILL OF MATERIALS |       |         | ASSEMBLY POS. 2-FB33 |          | No. Required     | 10          | POS. NO. 609 |      |
|-------------------|-------|---------|----------------------|----------|------------------|-------------|--------------|------|
| POS. NO.          | QTYN. | Profile | LENGTH (mm)          | Material | UNIT weight kg/m | weight (kg) |              | NOTE |
|                   |       |         |                      |          |                  | QTY.        | TOTAL        |      |
| 609               | 1     | L40*2   | 784.7                | S235JR   | 1.22             | 0.96        | 0.96         |      |
| Total Weight      |       |         |                      |          |                  | 1.0         | (kg)         |      |

| BOLT, NUT & WASHERS MATERIAL LIST |              |  |       |                     |             |
|-----------------------------------|--------------|--|-------|---------------------|-------------|
| EACH                              | REMARK       |  |       | UNIT WEIGHT KG/1000 | WEIGHT (KG) |
| 1                                 | M12x30 BOLTS |  | GR8.8 | 40.2                | 0.04        |
| 1                                 | M12 NUTS     |  | GR8.8 | 15.9                | 0.02        |
| 1                                 | M12 WASHERS  |  | GR8.8 | 5.9                 | 0.01        |
| Total weight                      |              |  |       |                     | 0.06 (KG)   |

GENERAL NOTES:

1. ALL HOLES ARE 22 mm DIA (UON).
2. ALL DIMENSIONS ARE IN MM (UON).
3. UNLESS OTHERWISE NOTED ALL FILLET WELD SIZE SHALL BE 7mm FILLET CONTINUOUS(UON)
4. RD DENOTES BASE LINE = 00

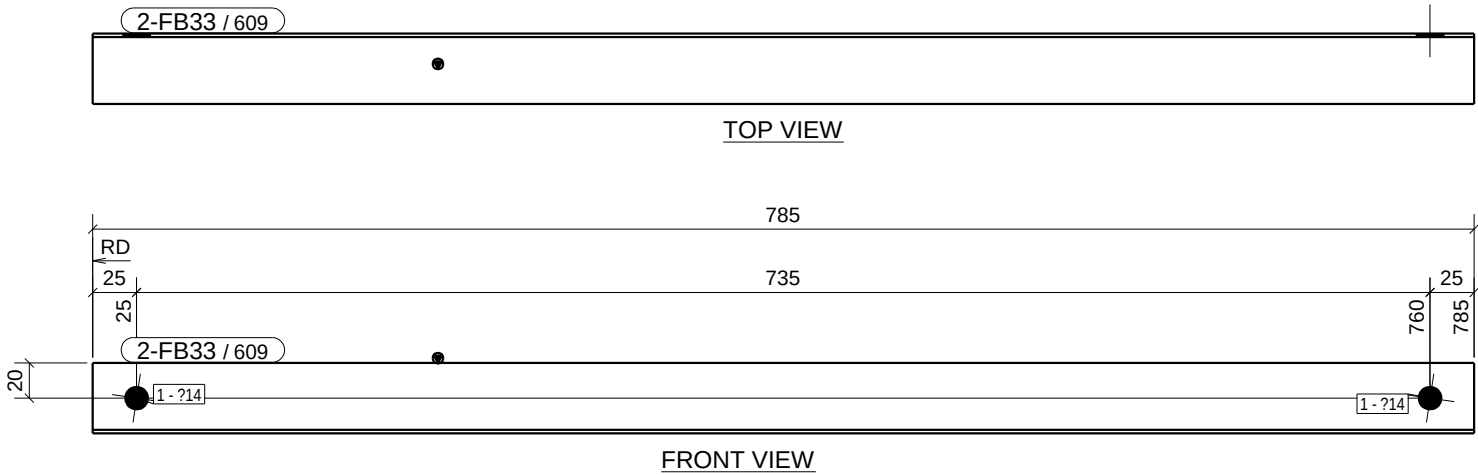

MARK: 2-FB33  
QTY: 10  
DESC.: L40\*2

| REV.                                         | DATE | DESCRIPTION | DRN       | CHK | DSN |
|----------------------------------------------|------|-------------|-----------|-----|-----|
| -----<br>-----<br>-----                      |      |             |           |     |     |
| PROJECT NAME:<br><br>MADAR GROUP JORDAN      |      |             |           |     |     |
| CONTRACTOR:<br><br>-----                     |      |             |           |     |     |
| DRAWING TITLE:<br><br>FLANGE.BRACE<br>2-FB33 |      |             |           |     |     |
| CHECKED BY                                   |      | A.A         | SCALE     |     |     |
| DATE                                         |      | A.A         | SHEET NO. |     |     |