



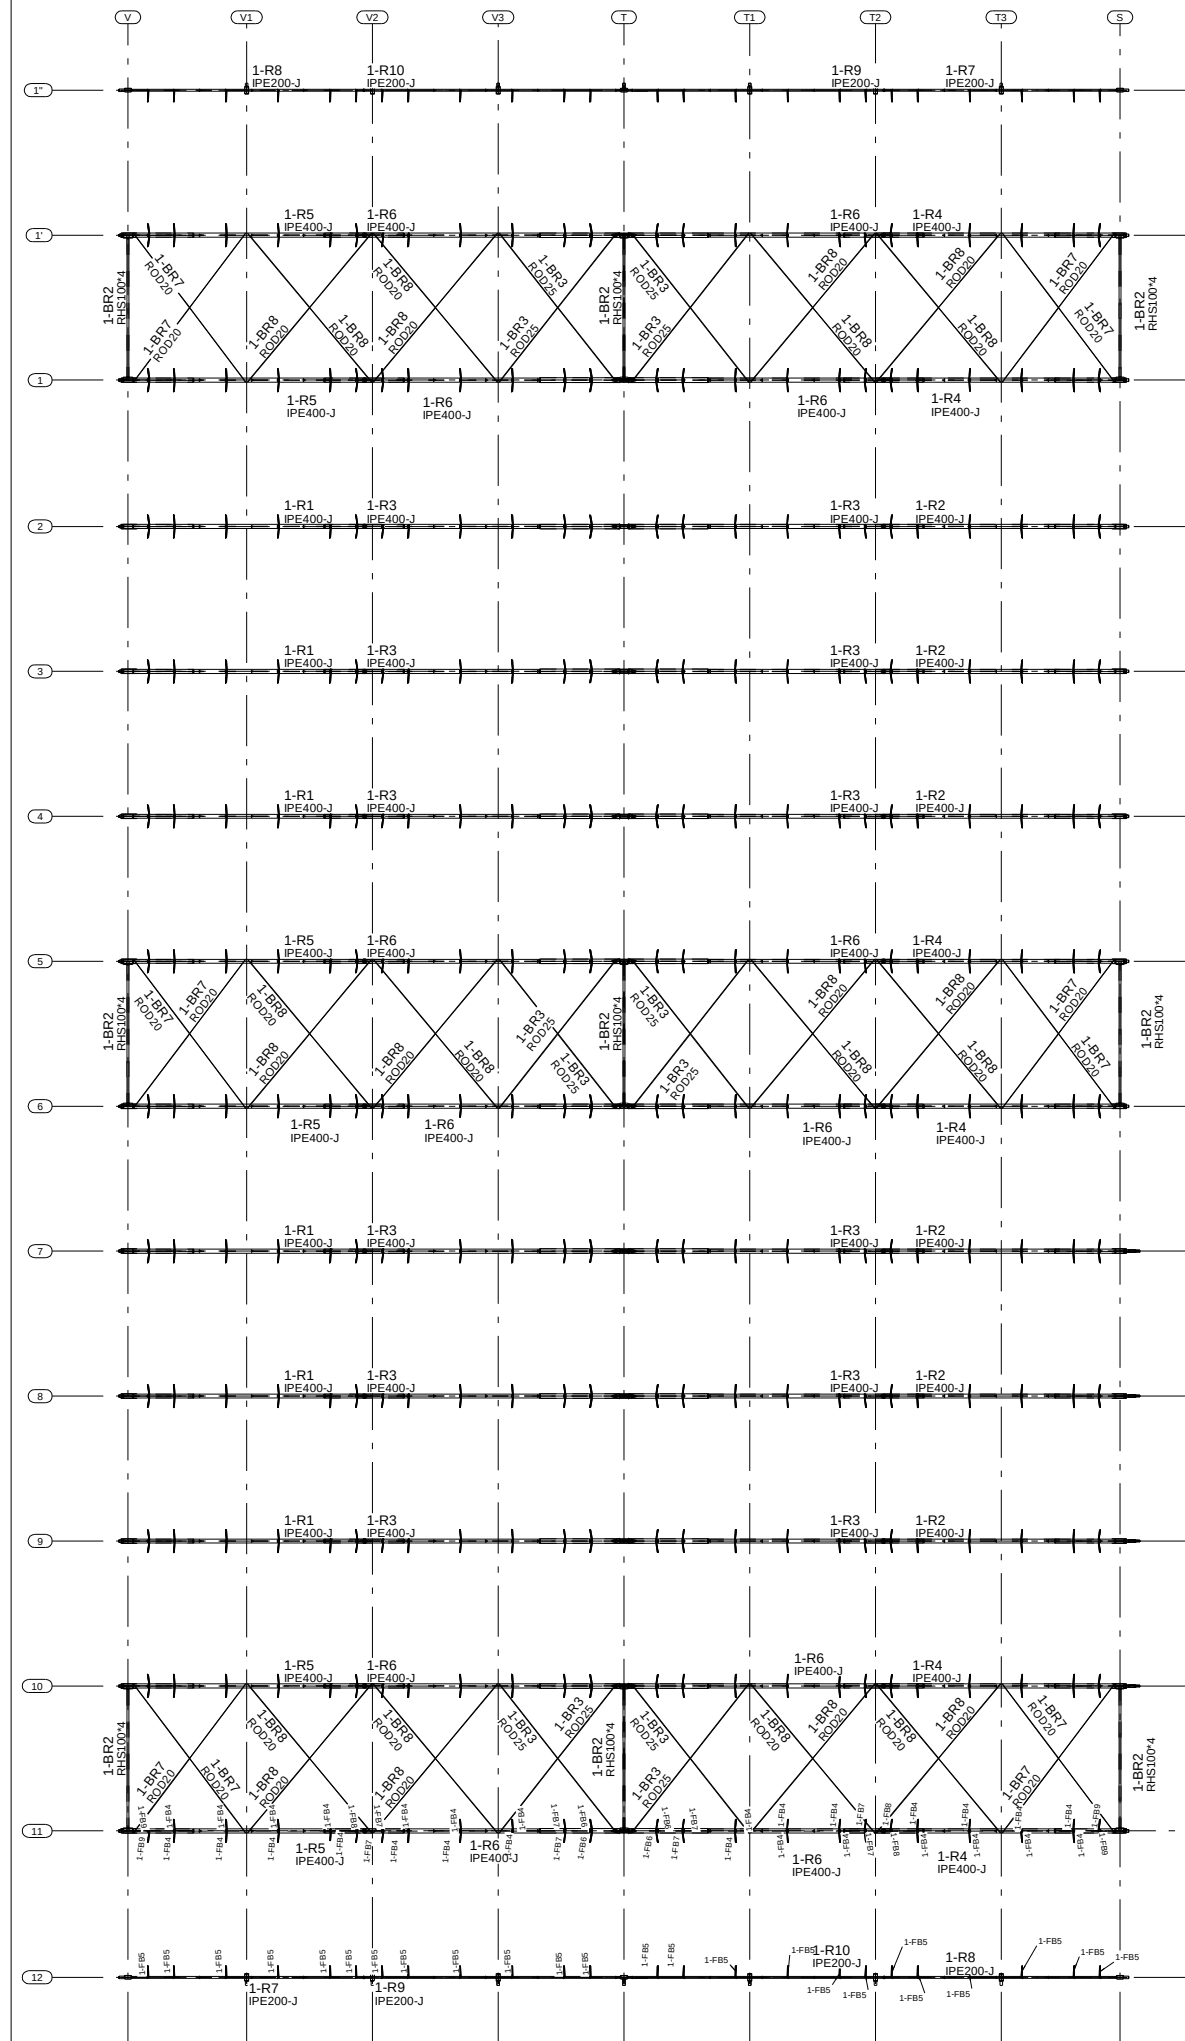

ROOF PLAN WITHOUT PURLIN - Area - 2

AREA - 1

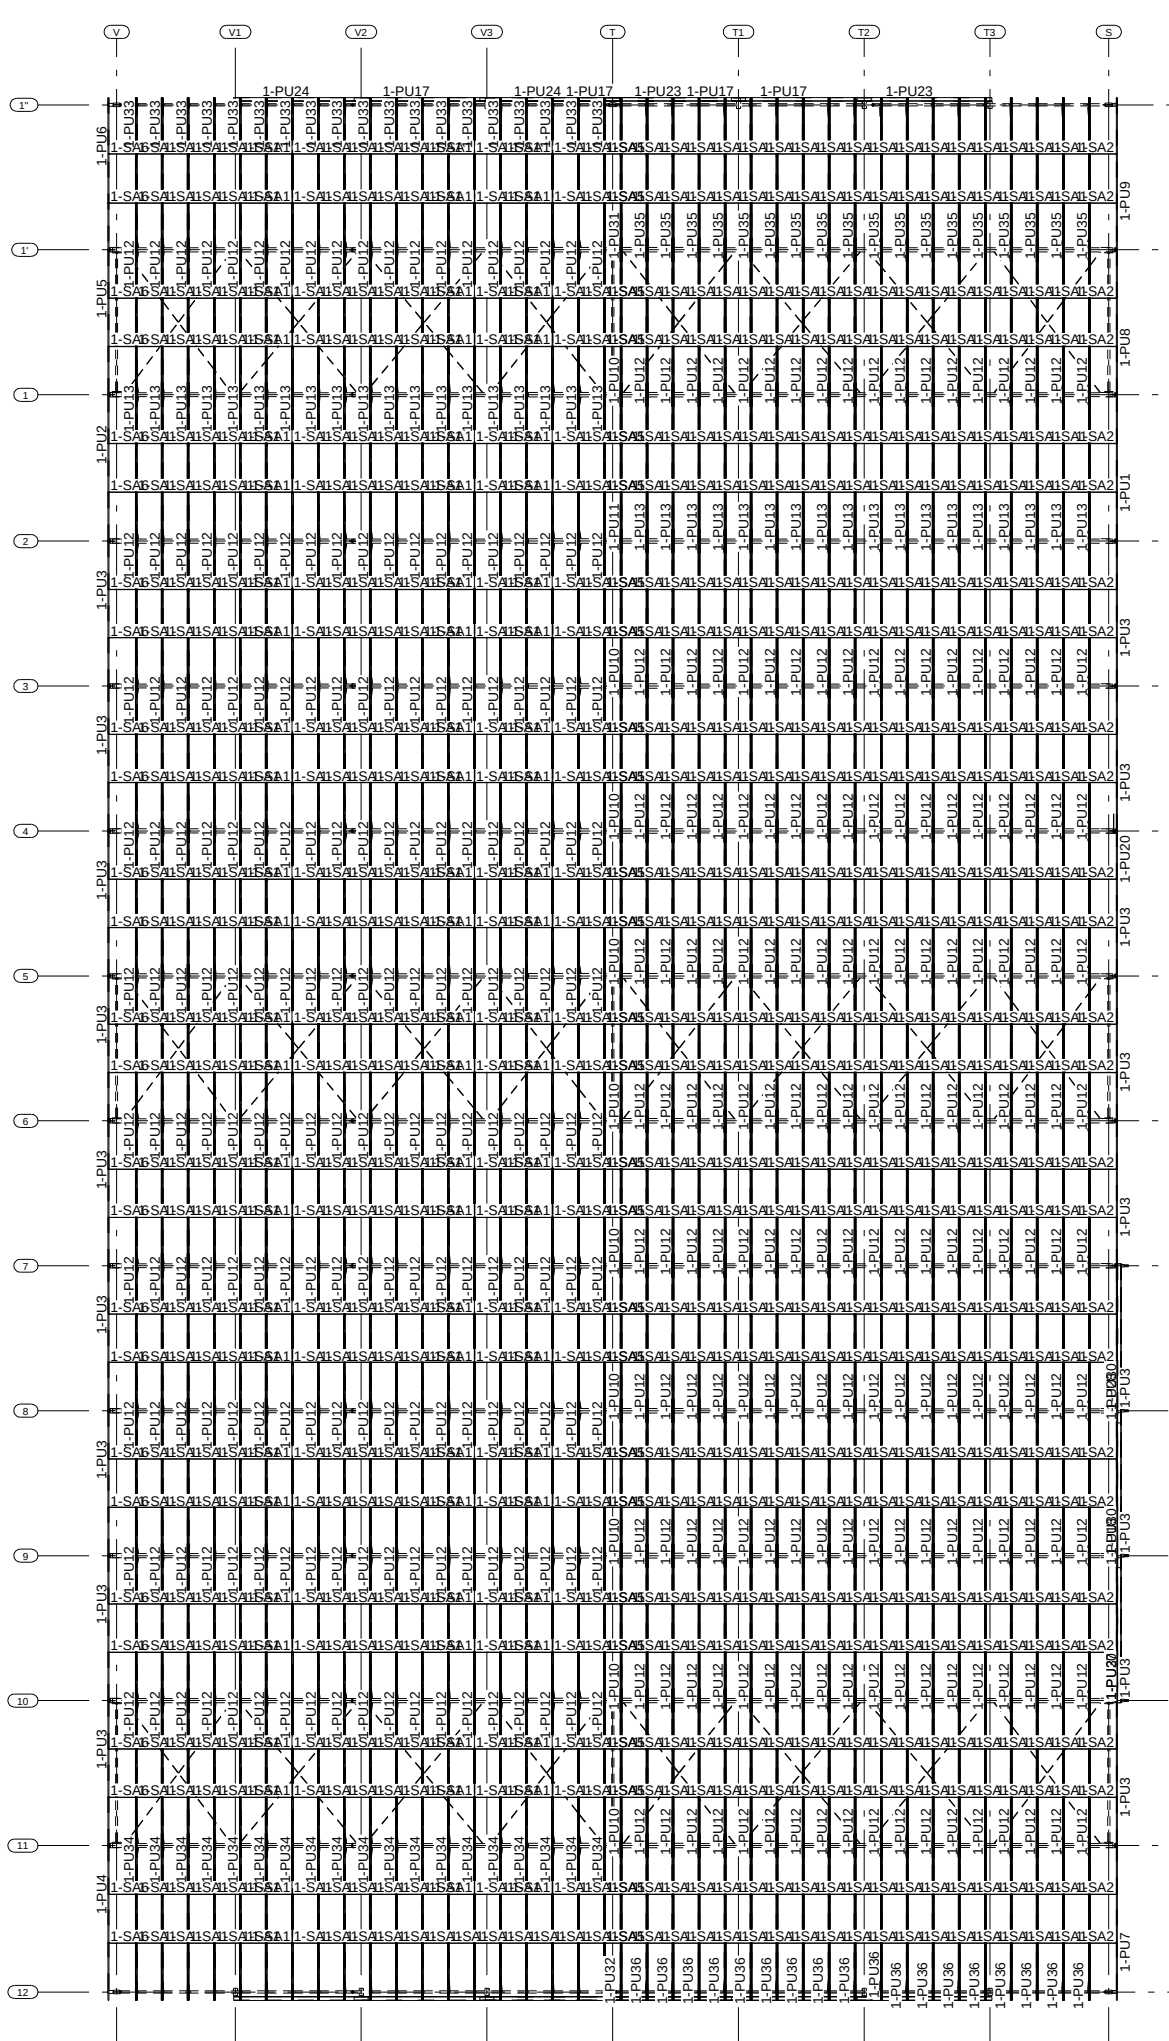

ROOF PLAN WITH PURLIN - Area - 2

		12-08-2028	ISSUED FOR FABRICATION		A.A	H.H
REV.	DATE	DESCRIPTION		DRN	CHK	EDR

PROJECT NAME:						
SCHOOL PROJECT						
CONTRACTOR:						
--						
DRAWING TITLE:						
STEEL STRUCTURE						
ROOF PLAN- Area - 2						
CHECKED BY		A.A		SCALE		
DATE		A.A		SHEET NO.		E07