


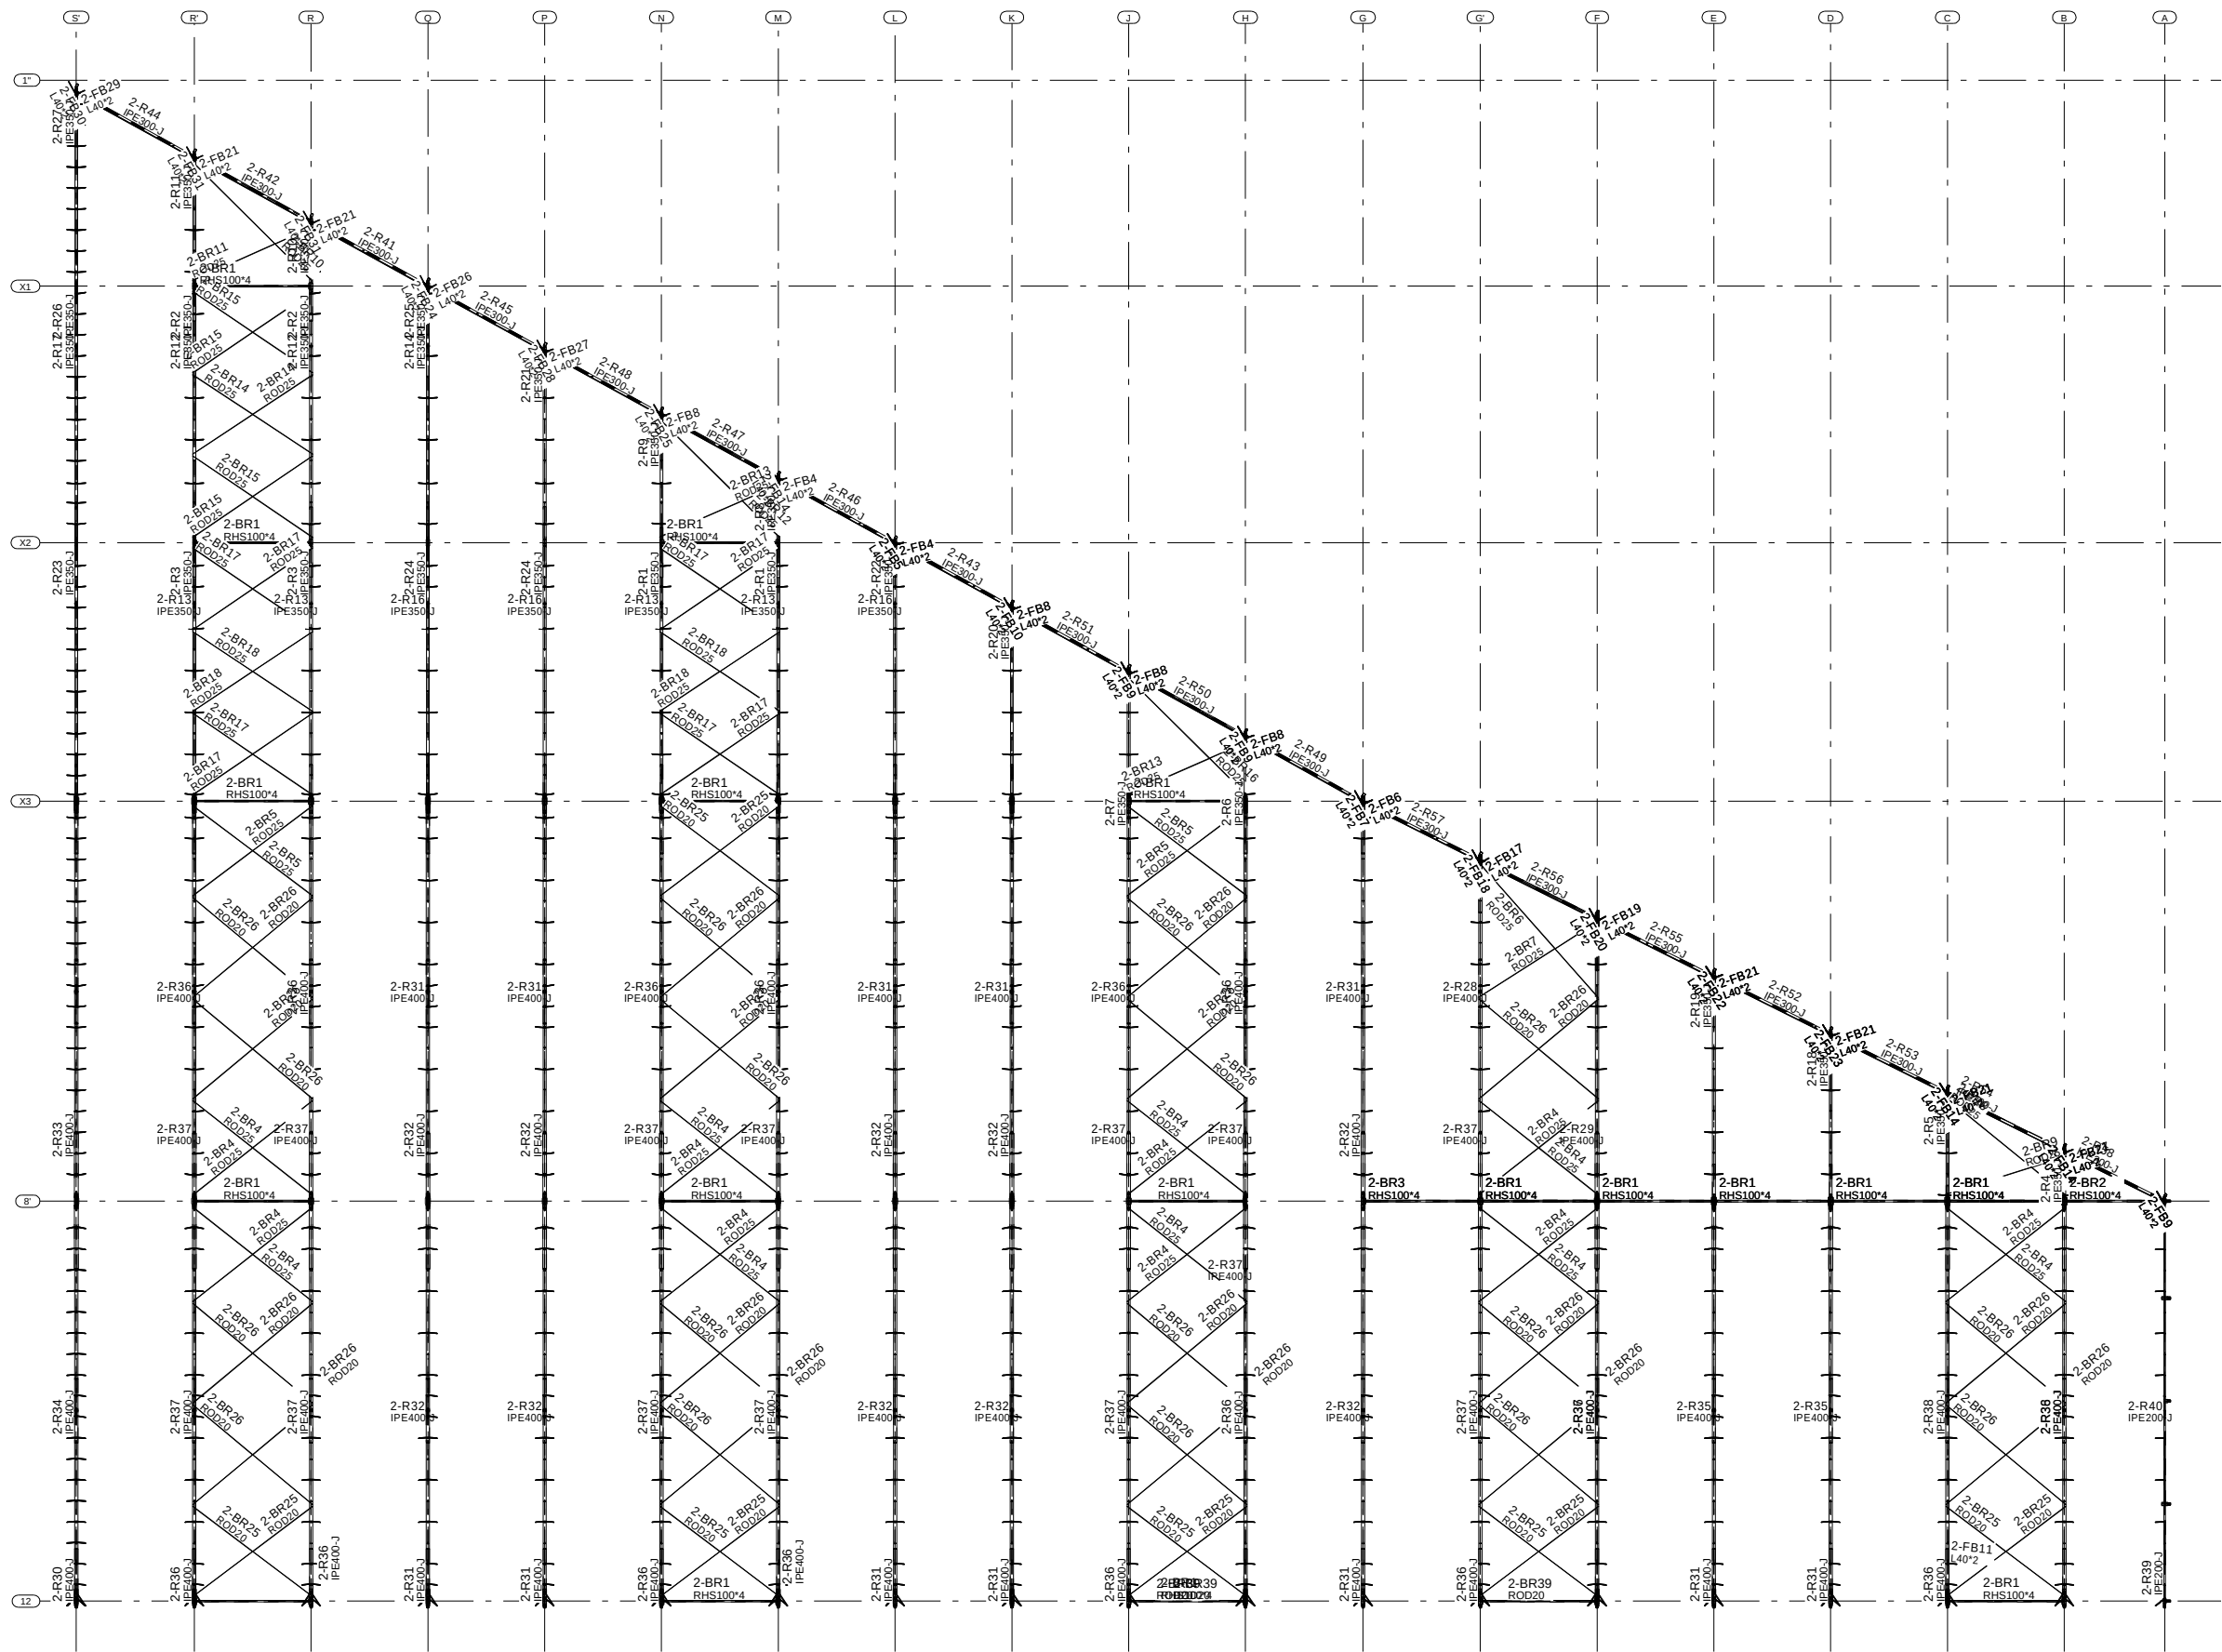

PLAN @EL+9.25

|                                    |      |                        |  |     |     |
|------------------------------------|------|------------------------|--|-----|-----|
| 12-08-2024                         |      | ISSUED FOR FABRICATION |  | A.A | H.H |
| REV.                               | DATE | DESCRIPTION            |  | DRN | CHK |
| *****                              |      |                        |  |     |     |
| PROJECT NAME:                      |      |                        |  |     |     |
| SCHOOL PROJECT                     |      |                        |  |     |     |
| CONTRACTOR:                        |      |                        |  |     |     |
| --                                 |      |                        |  |     |     |
| DRAWING TITLE:                     |      |                        |  |     |     |
| STEEL STRUCTURE                    |      |                        |  |     |     |
| ROOF PLAN WITHOUT PURLIN- Area - 3 |      |                        |  |     |     |
| CHECKED BY                         |      | SCALE                  |  |     |     |
| A.A                                |      |                        |  |     |     |
| DATE                               |      | SHEET NO.              |  | E08 |     |
| A.A                                |      |                        |  |     |     |