


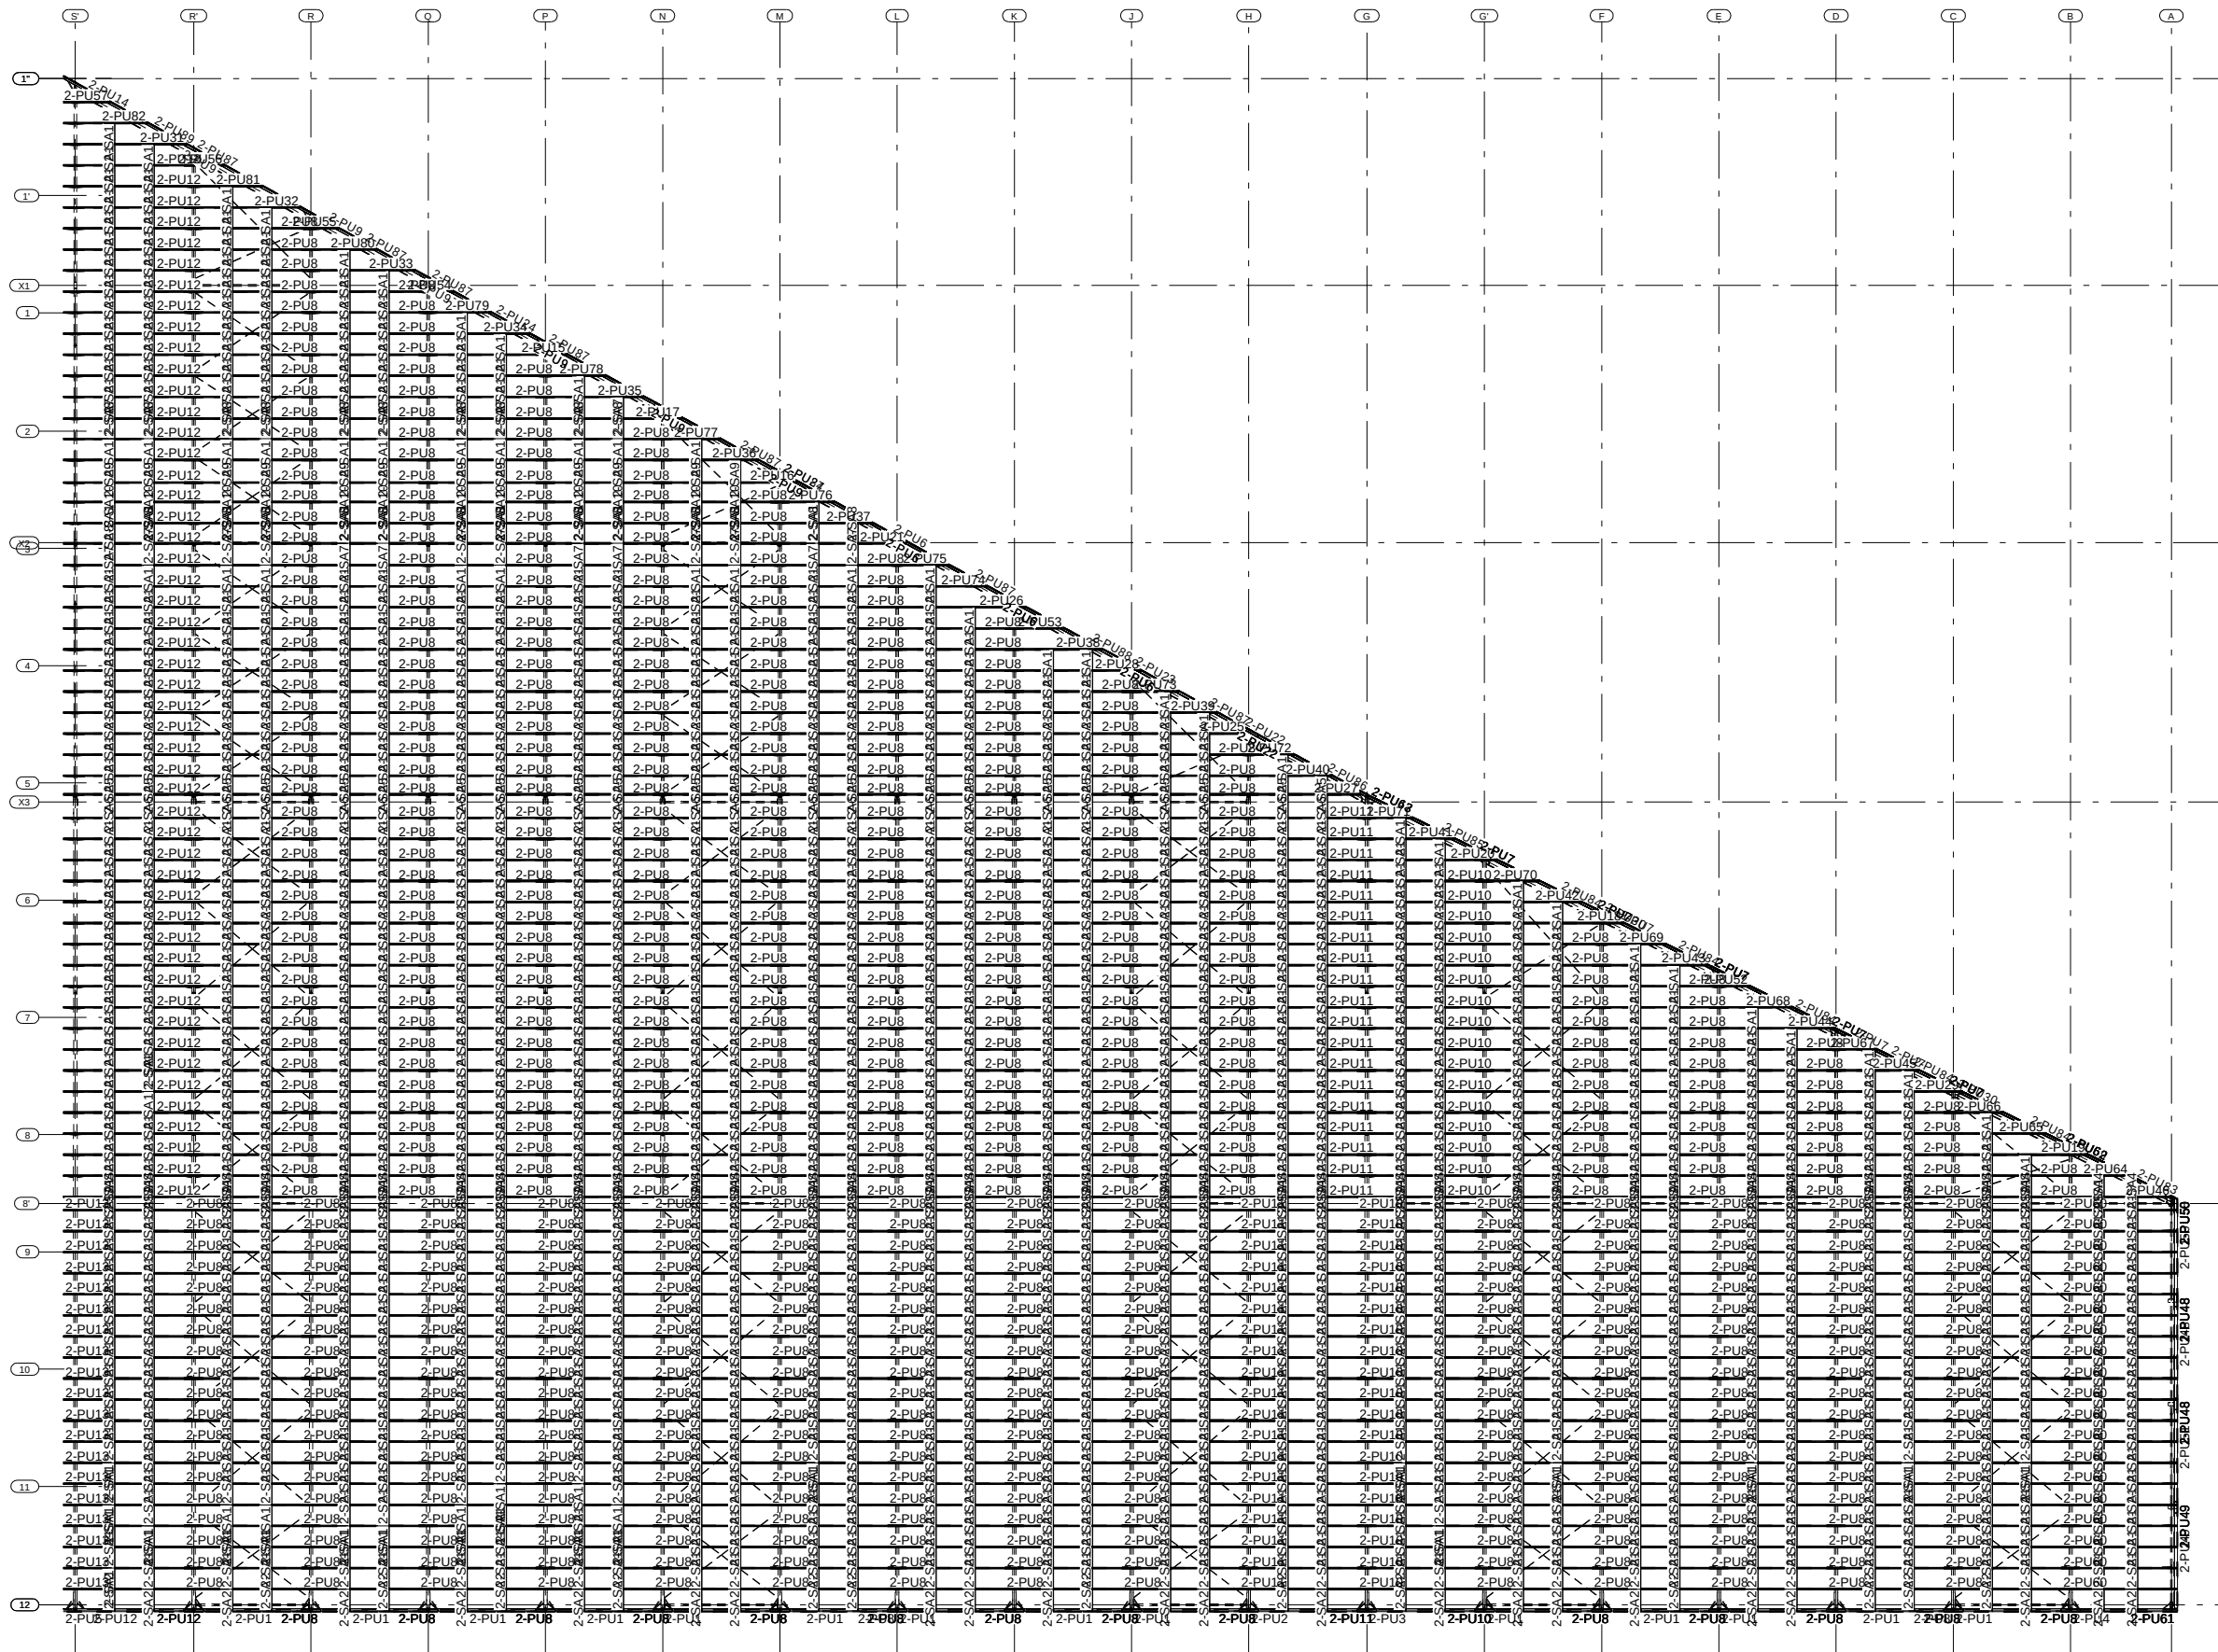

PLAN @EL+9.25

|                                                                                       |      |                        |  |           |     |     |  |
|---------------------------------------------------------------------------------------|------|------------------------|--|-----------|-----|-----|--|
|  |      | ISSUED FOR FABRICATION |  | A.A       |     | H.H |  |
| REV.                                                                                  | DATE | DESCRIPTION            |  | DRN       | CHK | CIN |  |
| *****                                                                                 |      |                        |  |           |     |     |  |
| PROJECT NAME:                                                                         |      |                        |  |           |     |     |  |
| SCHOOL PROJECT                                                                        |      |                        |  |           |     |     |  |
| CONTRACTOR:                                                                           |      |                        |  |           |     |     |  |
| --                                                                                    |      |                        |  |           |     |     |  |
| DRAWING TITLE:                                                                        |      |                        |  |           |     |     |  |
| STEEL STRUCTURE                                                                       |      |                        |  |           |     |     |  |
| ROOF PLAN WITHOUT PURLIN- Area - 3                                                    |      |                        |  |           |     |     |  |
| CHECKED BY                                                                            |      | A.A                    |  | SCALE     |     |     |  |
| DATE                                                                                  |      | A.A                    |  | SHEET NO. |     | E09 |  |