


SECTION GRID 8'

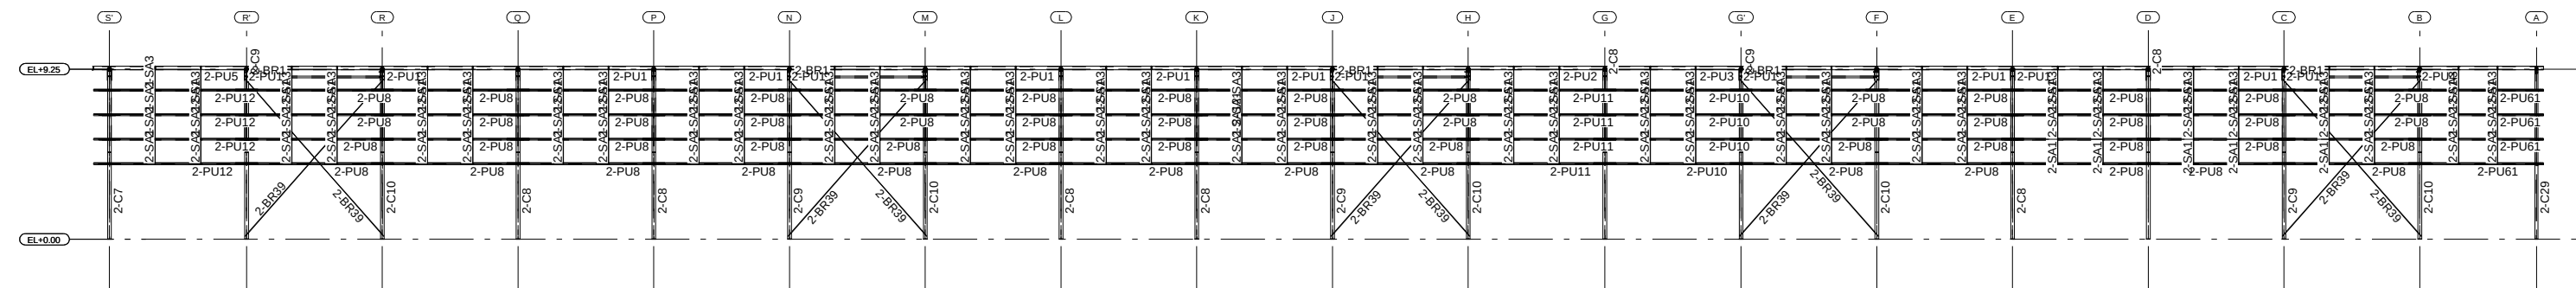

SECTION GRID 12

 12-08-2024		ISSUED FOR FABRICATION		A.A.	H.H.
REV.	DATE	DESCRIPTION		DRN	CHK

PROJECT NAME:					
SCHOOL PROJECT					
CONTRACTOR:					
--					
DRAWING TITLE:					
STEEL STRUCTURE					
SECTION GRID (12 + 8')					
CHECKED BY		A.A.	SCALE		
DATE		A.A.	SHEET NO.	E23	