




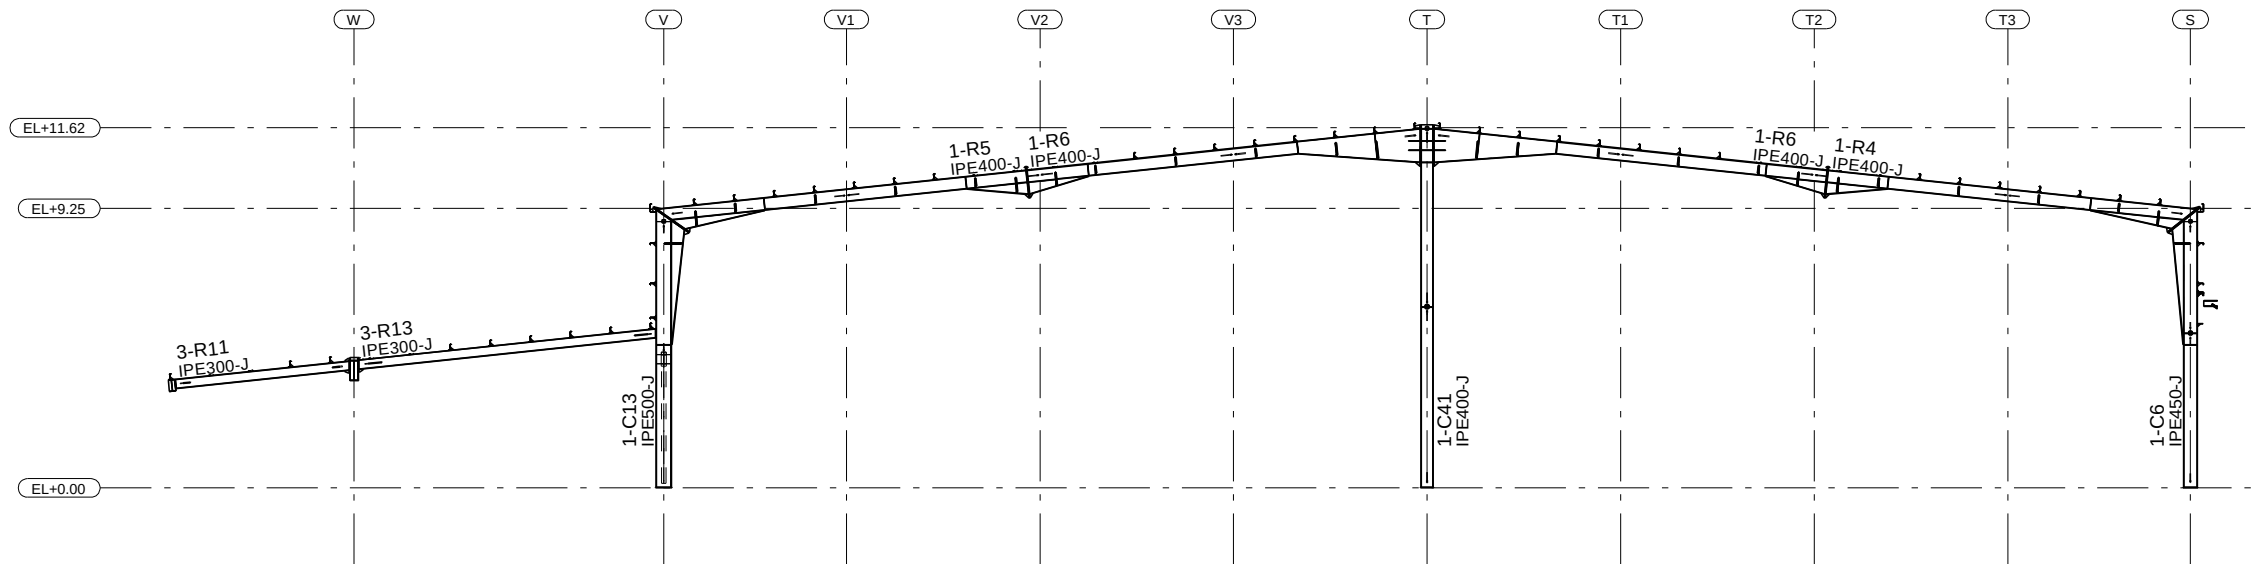

SECTION GRID 1

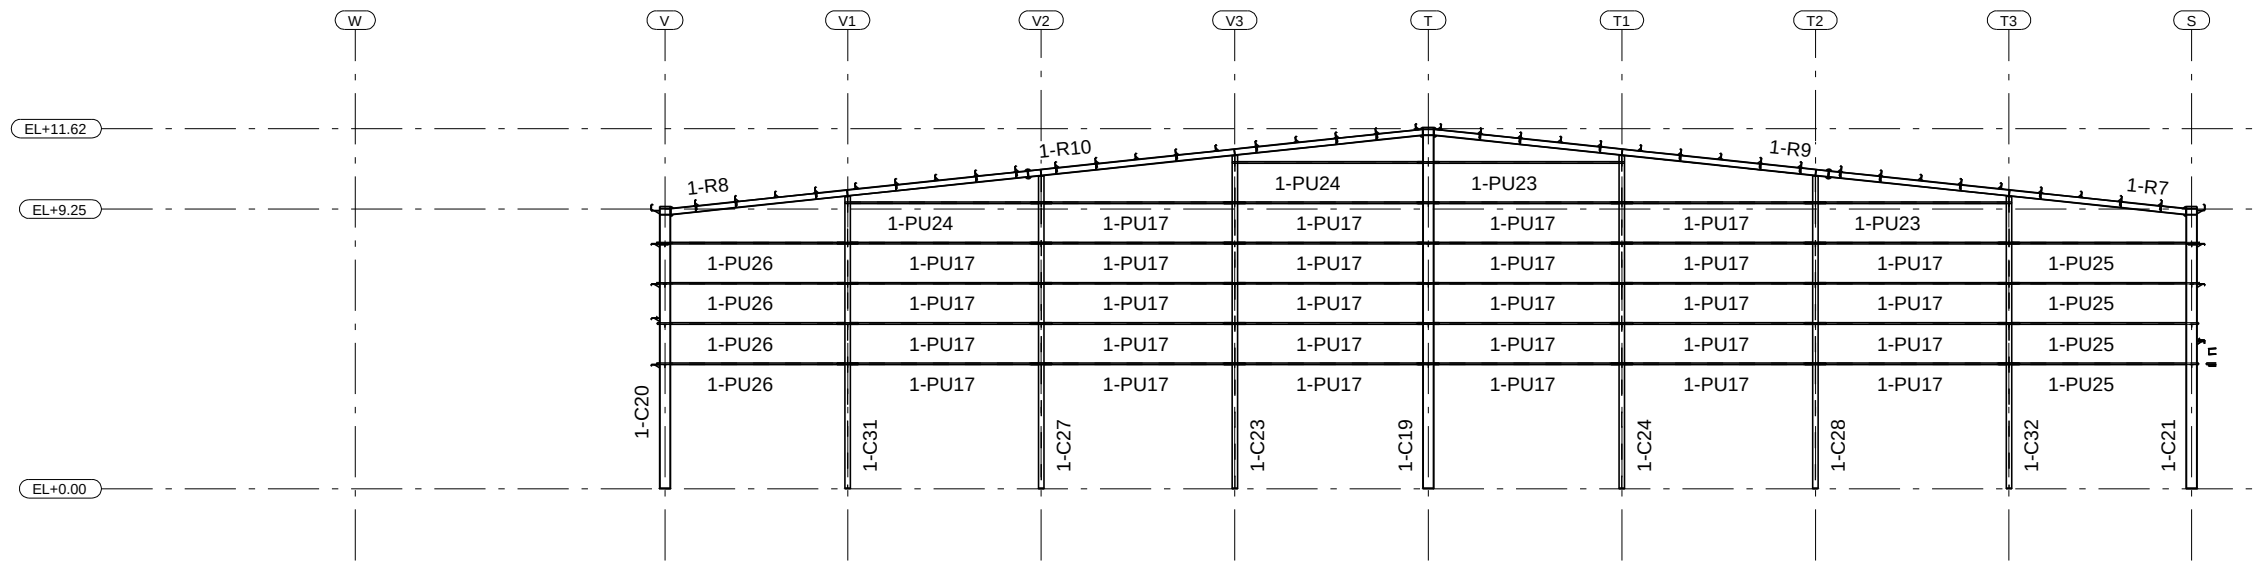

SECTION GRID 1"

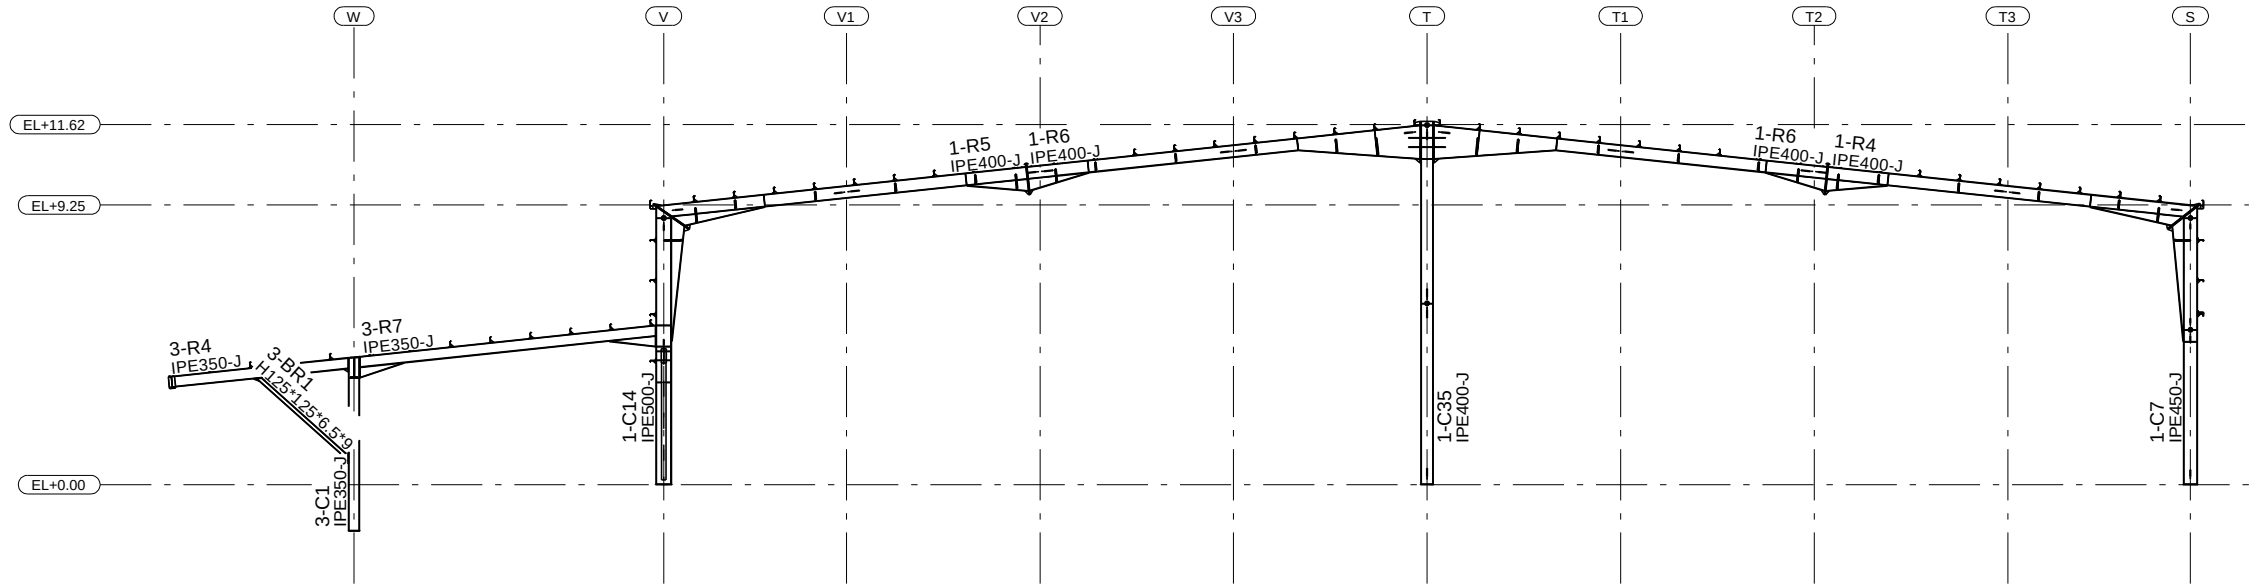

SECTION GRID 1'

|                            |            |                        |     |     |     |
|----------------------------|------------|------------------------|-----|-----|-----|
| FD                         | 12-06-2026 | ISSUED FOR FABRICATION | A.A | H.H |     |
| REV                        | DATE       | DESCRIPTION            | DRN | CHK | DSN |
| .....                      |            |                        |     |     |     |
| PROJECT NAME:              |            |                        |     |     |     |
| SCHOOL PROJECT             |            |                        |     |     |     |
| CONTRACTOR:                |            |                        |     |     |     |
| ..                         |            |                        |     |     |     |
| DRAWING TITLE:             |            |                        |     |     |     |
| STEEL STRUCTURE            |            |                        |     |     |     |
| SECTION GRID (1 + 1' + 1") |            |                        |     |     |     |
| CHECKED BY                 | A.A        | SCALE                  |     |     |     |
| DATE                       | A.A        | SHEET NO.              | E10 |     |     |