




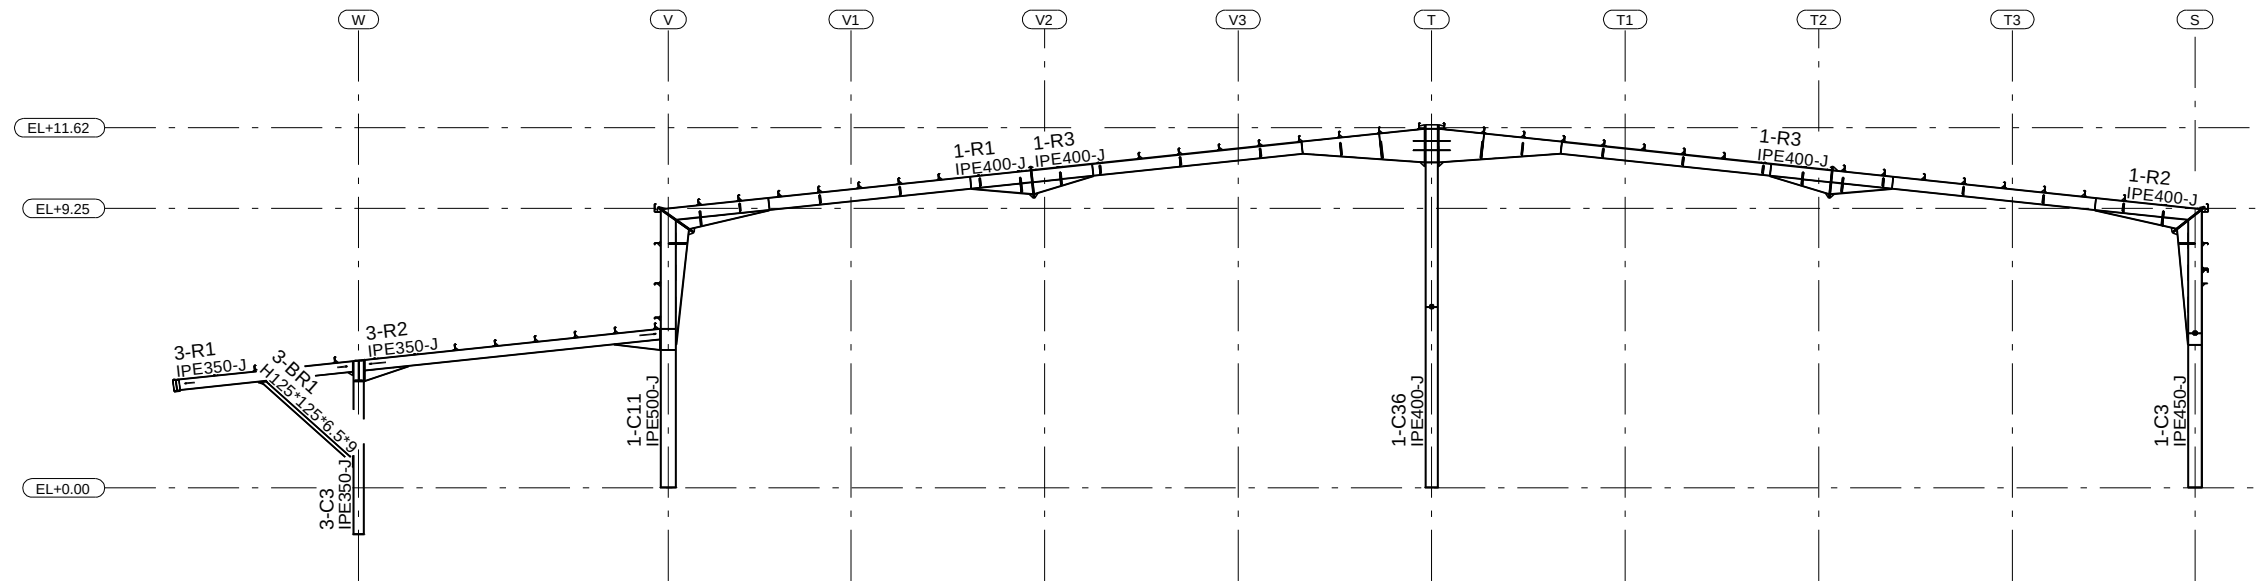

SECTION GRID 2

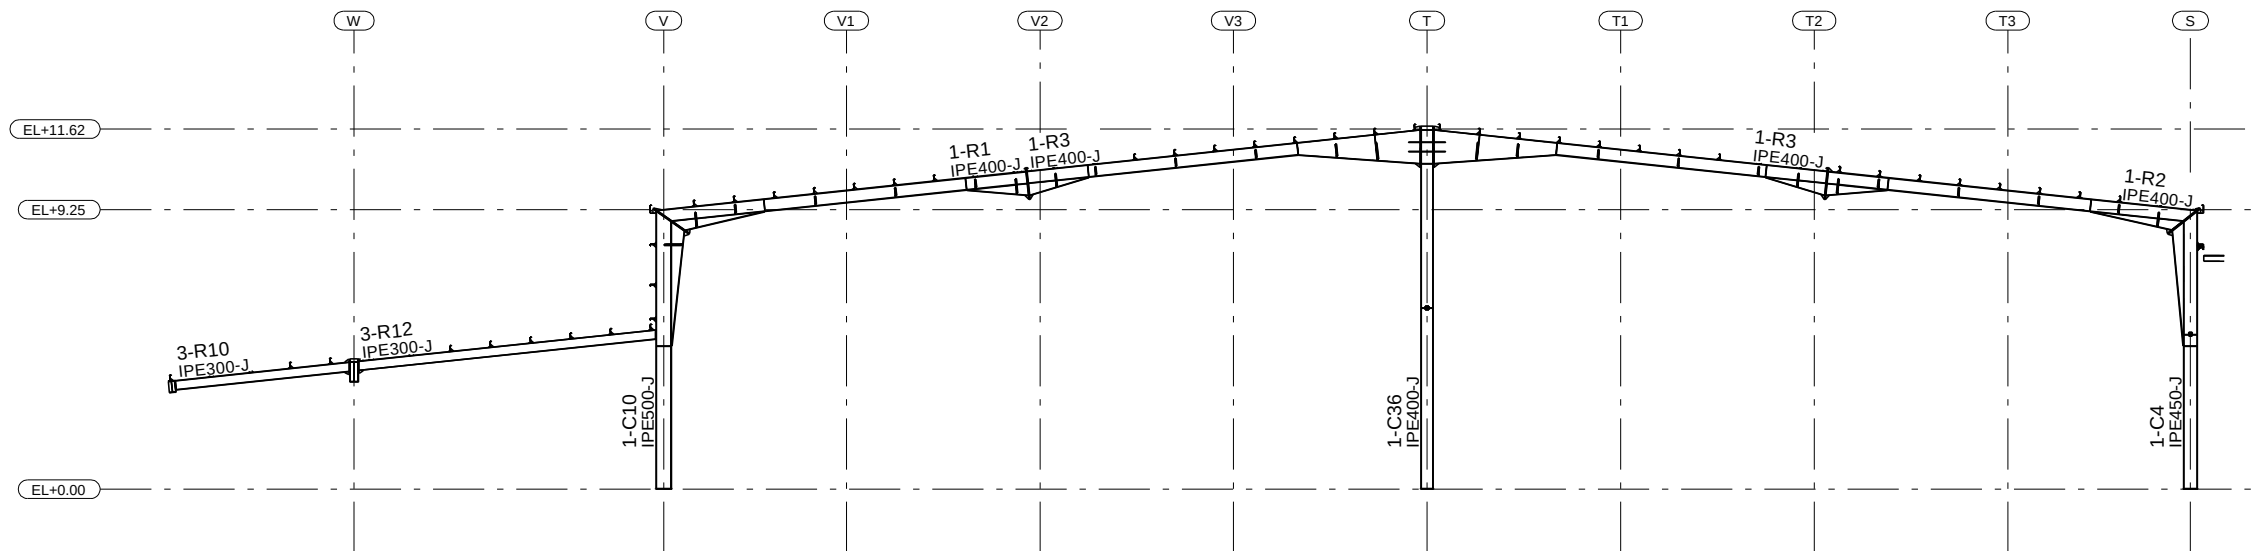

SECTION GRID 3

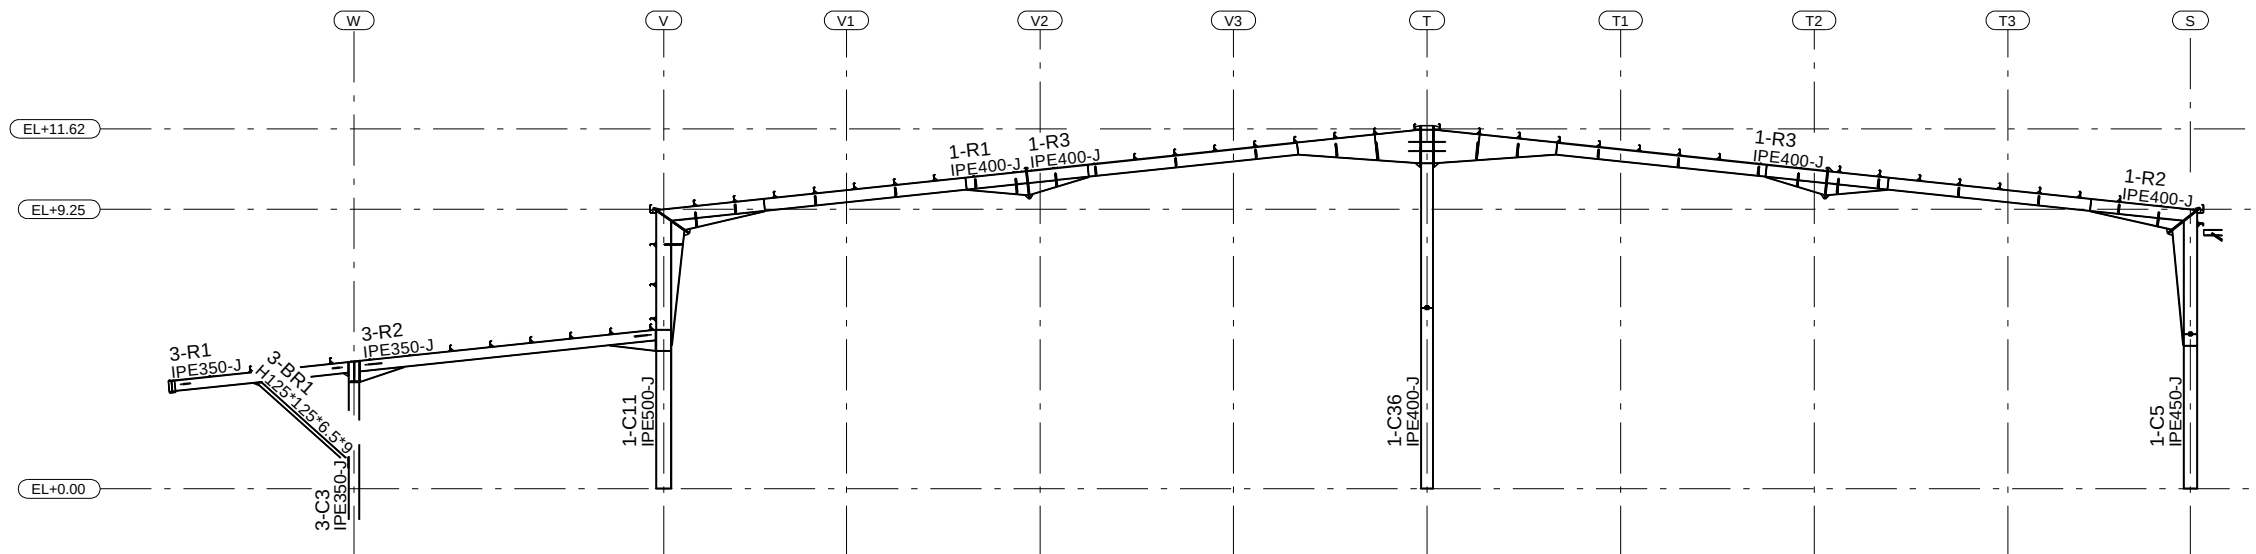

SECTION GRID 4

FD	12-06-2026	ISSUED FOR FABRICATION		A.A	H.H	
	REV	DATE	DESCRIPTION	DRN	CHK	DSN
.....						
PROJECT NAME:						
SCHOOL PROJECT						
CONTRACTOR:						
--						
DRAWING TITLE:						
STEEL STRUCTURE						
SECTION GRID (2 + 3 + 4)						
CHECKED BY		A.A		SCALE		
DATE		A.A		SHEET NO.		E11