




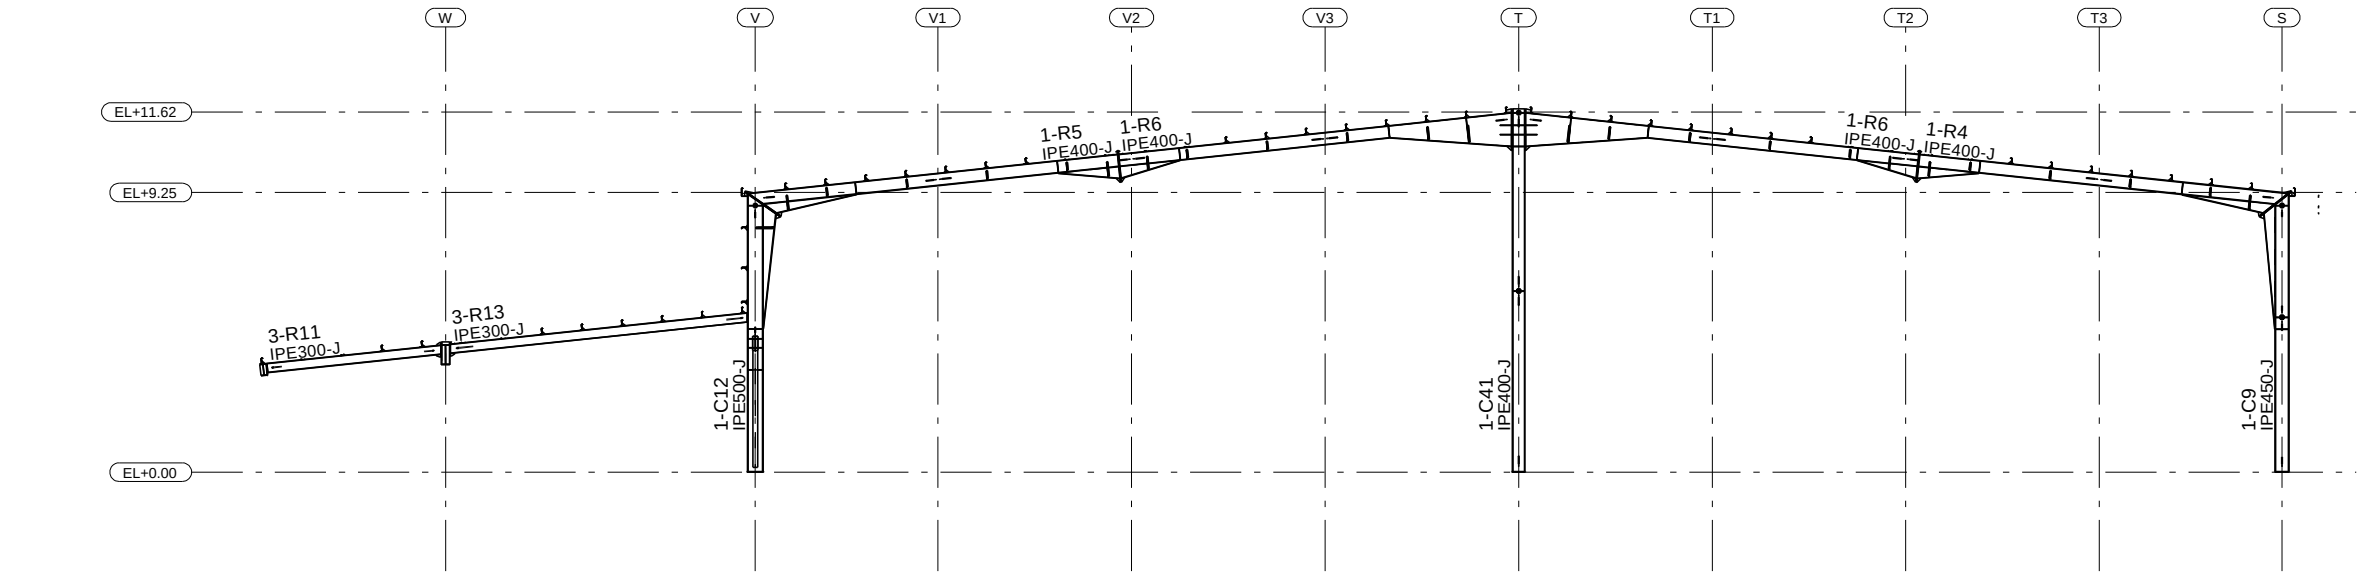

SECTION GRID 5

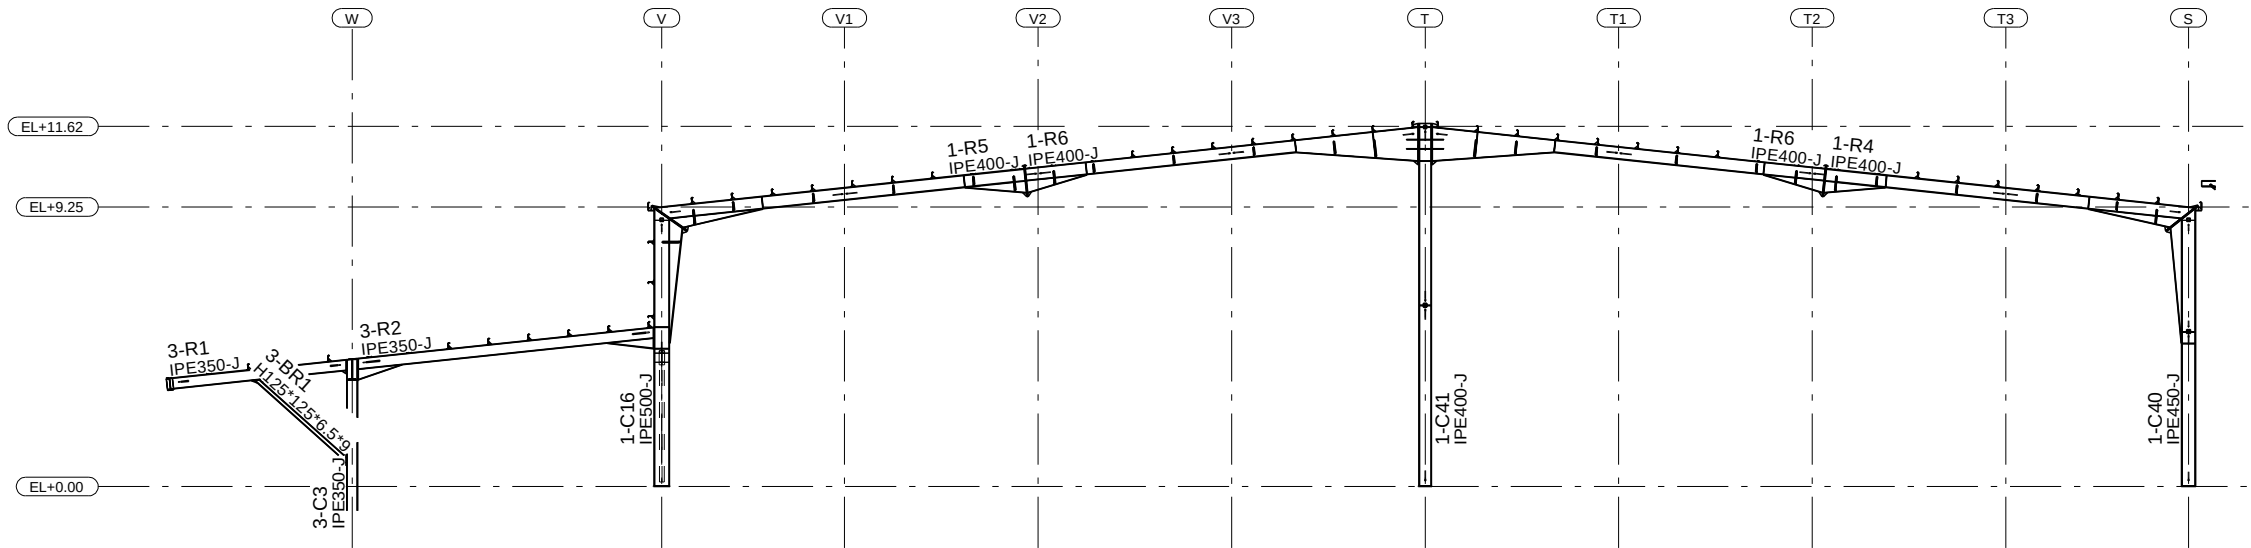

SECTION GRID 6

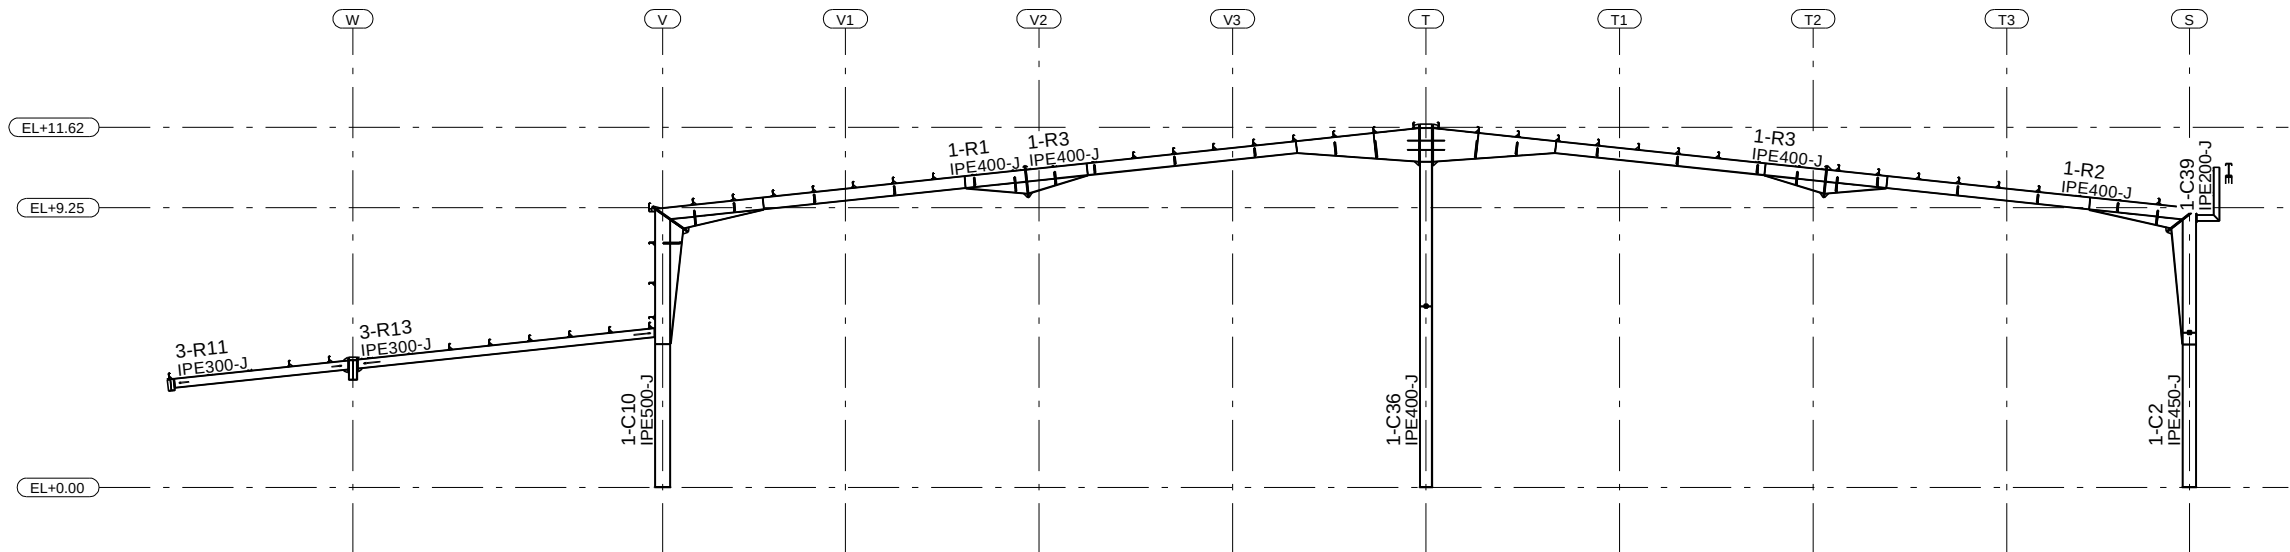

SECTION GRID 7

FD	12-06-2026	ISSUED FOR FABRICATION	A.A	H.H	
REV	DATE	DESCRIPTION	DRN	CHK	DSN
PROJECT NAME:					
SCHOOL PROJECT					
CONTRACTOR:					

DRAWING TITLE:					
STEEL STRUCTURE					
SECTION GRID (5 + 6 + 7)					
CHECKED BY	A.A	SCALE			
DATE	A.A	SHEET NO.	E12		