




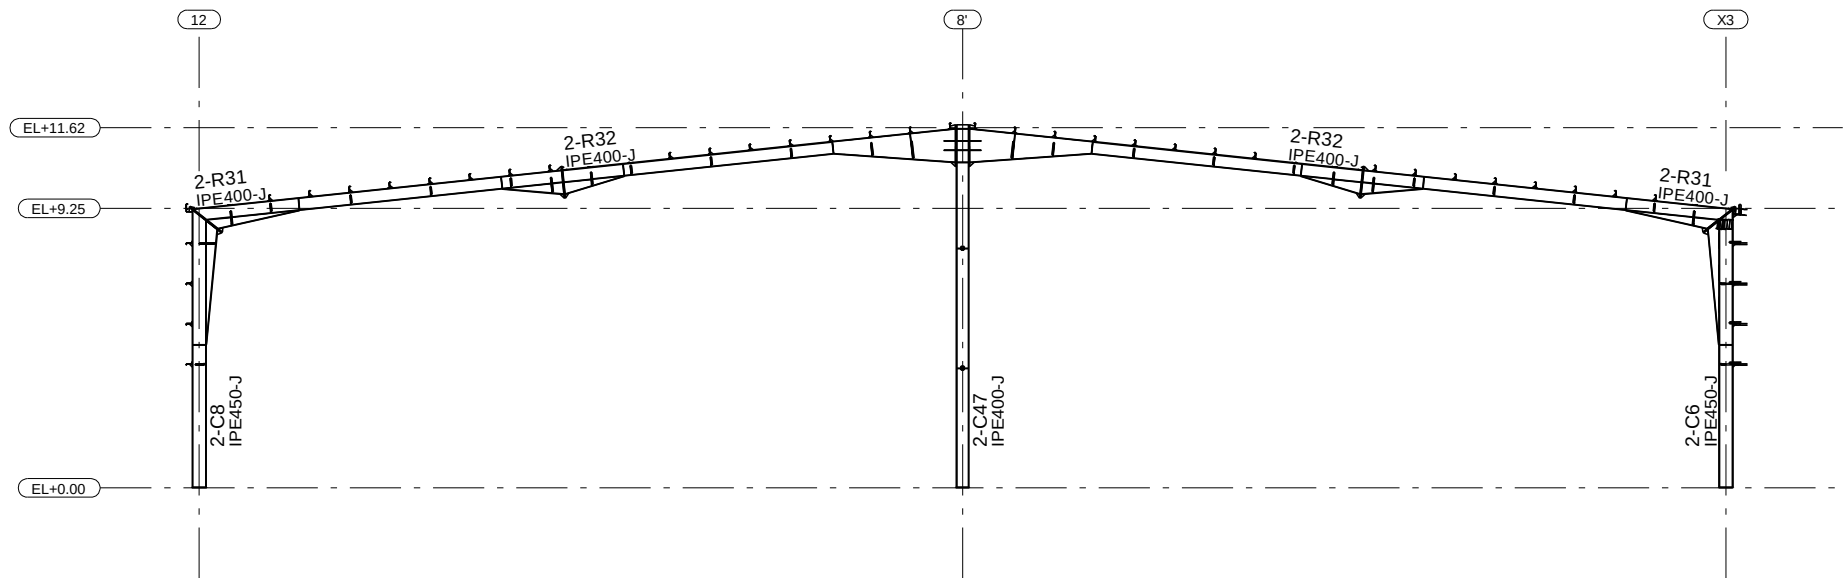

SECTION GRID G

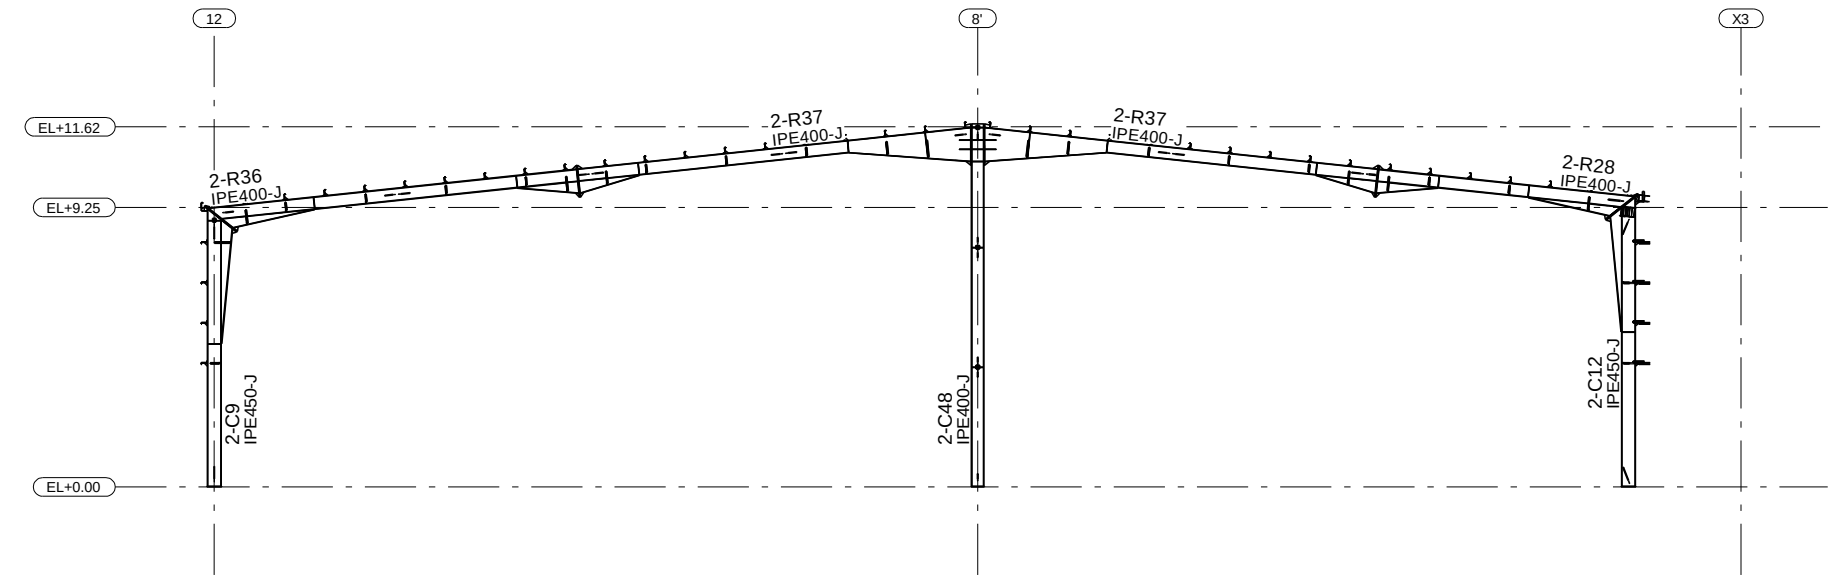

SECTION GRID G'

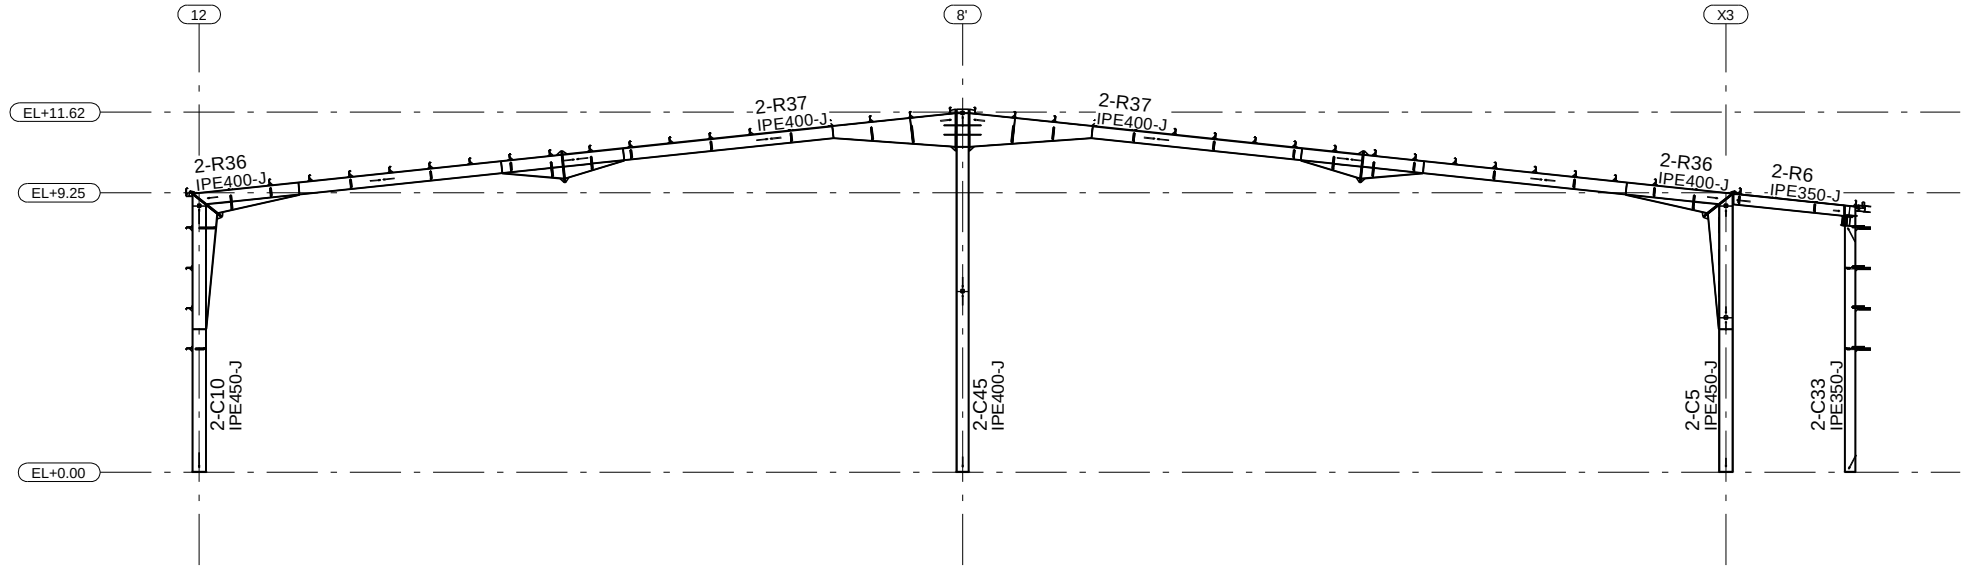

SECTION GRID H

FD	12-06-2026	ISSUED FOR FABRICATION			A.A	H.H	
REV.	DATE	DESCRIPTION			DRN	CHK	DSN

PROJECT NAME:							
SCHOOL PROJECT							
CONTRACTOR:							
--							
DRAWING TITLE:							
STEEL STRUCTURE							
SECTION GRID (G + G' + H)							
CHECKED BY		A.A		SCALE			
DATE		A.A		SHEET NO.		E18	