




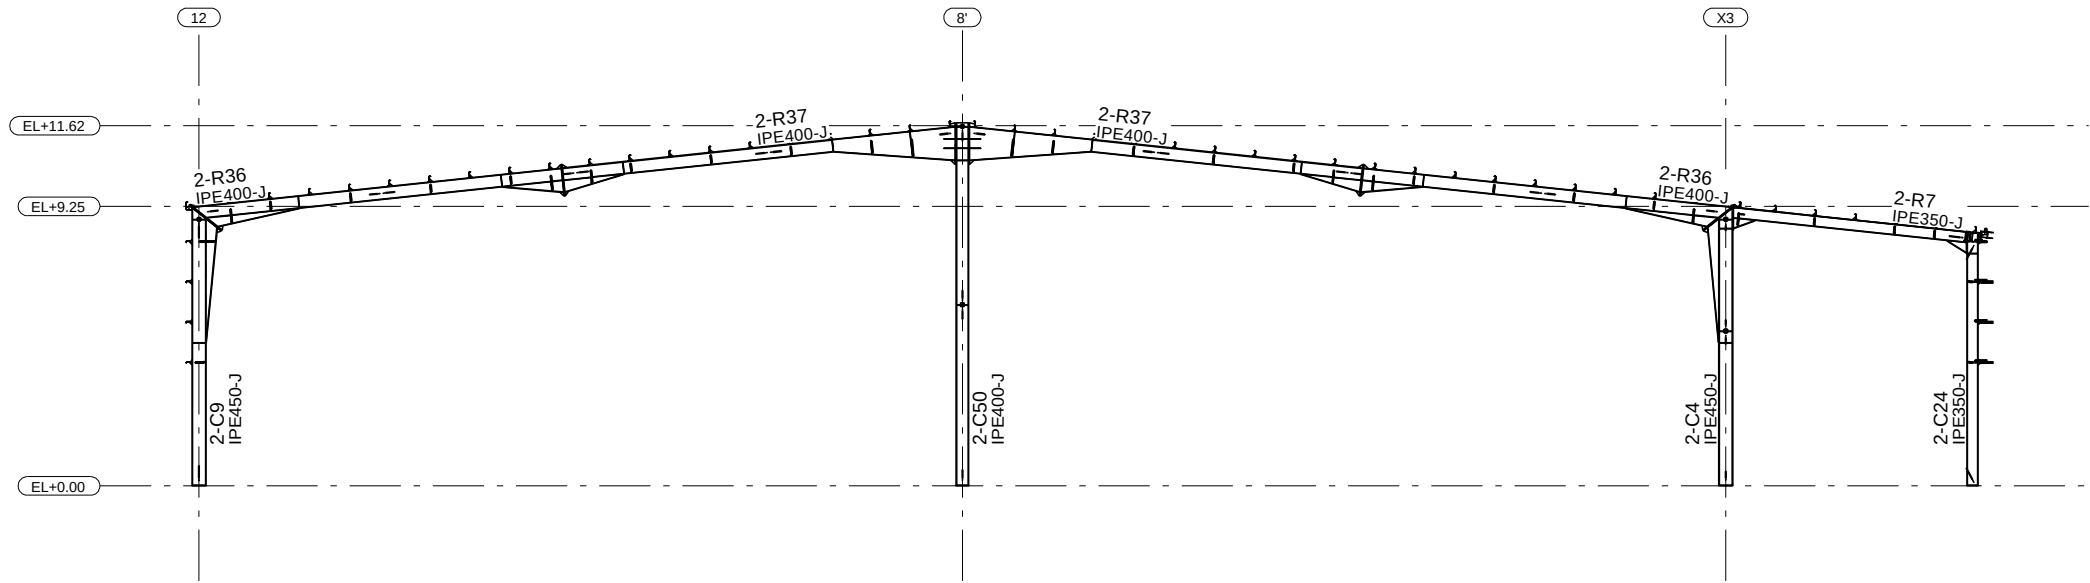

SECTION GRID J

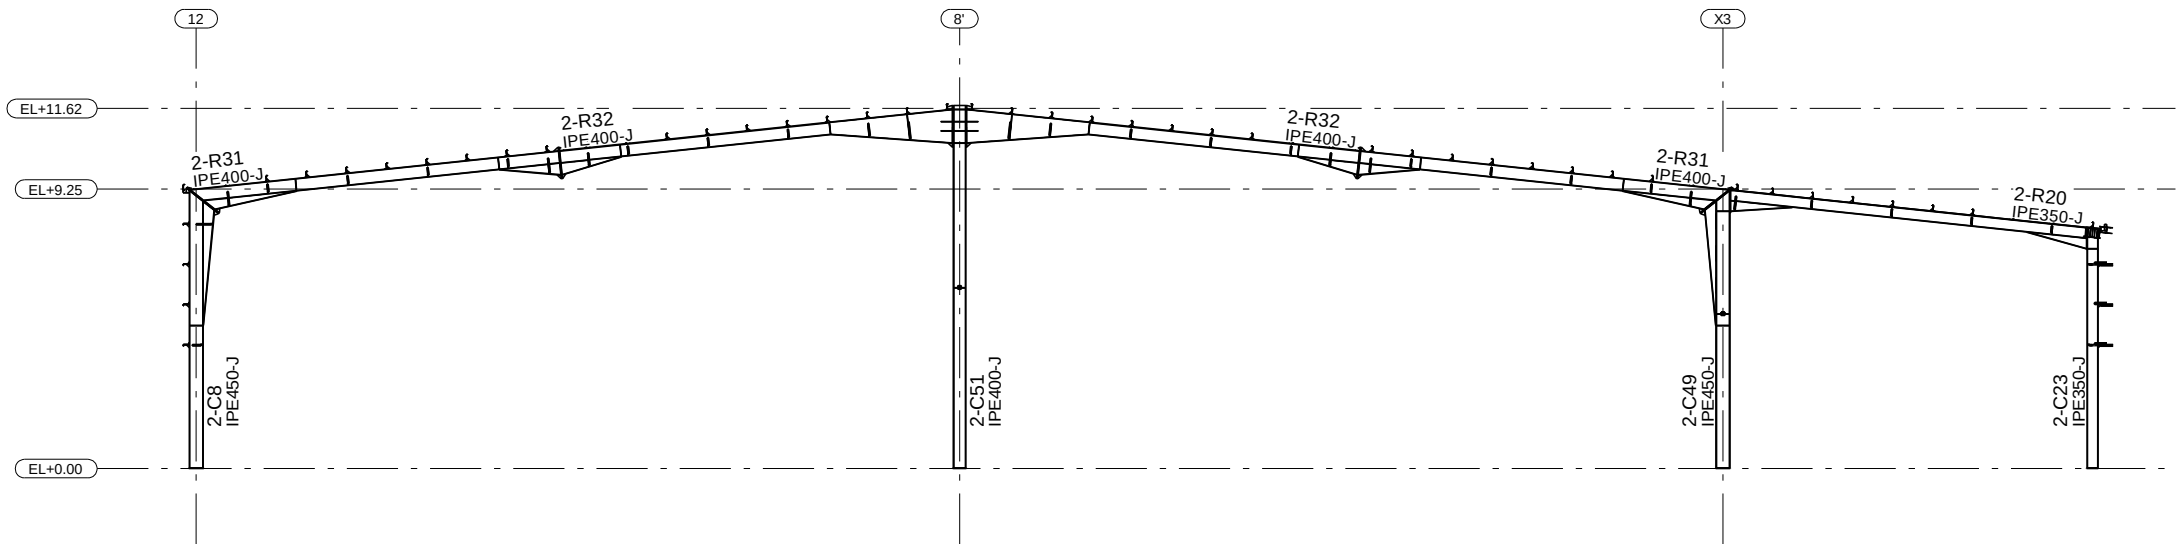

SECTION GRID K

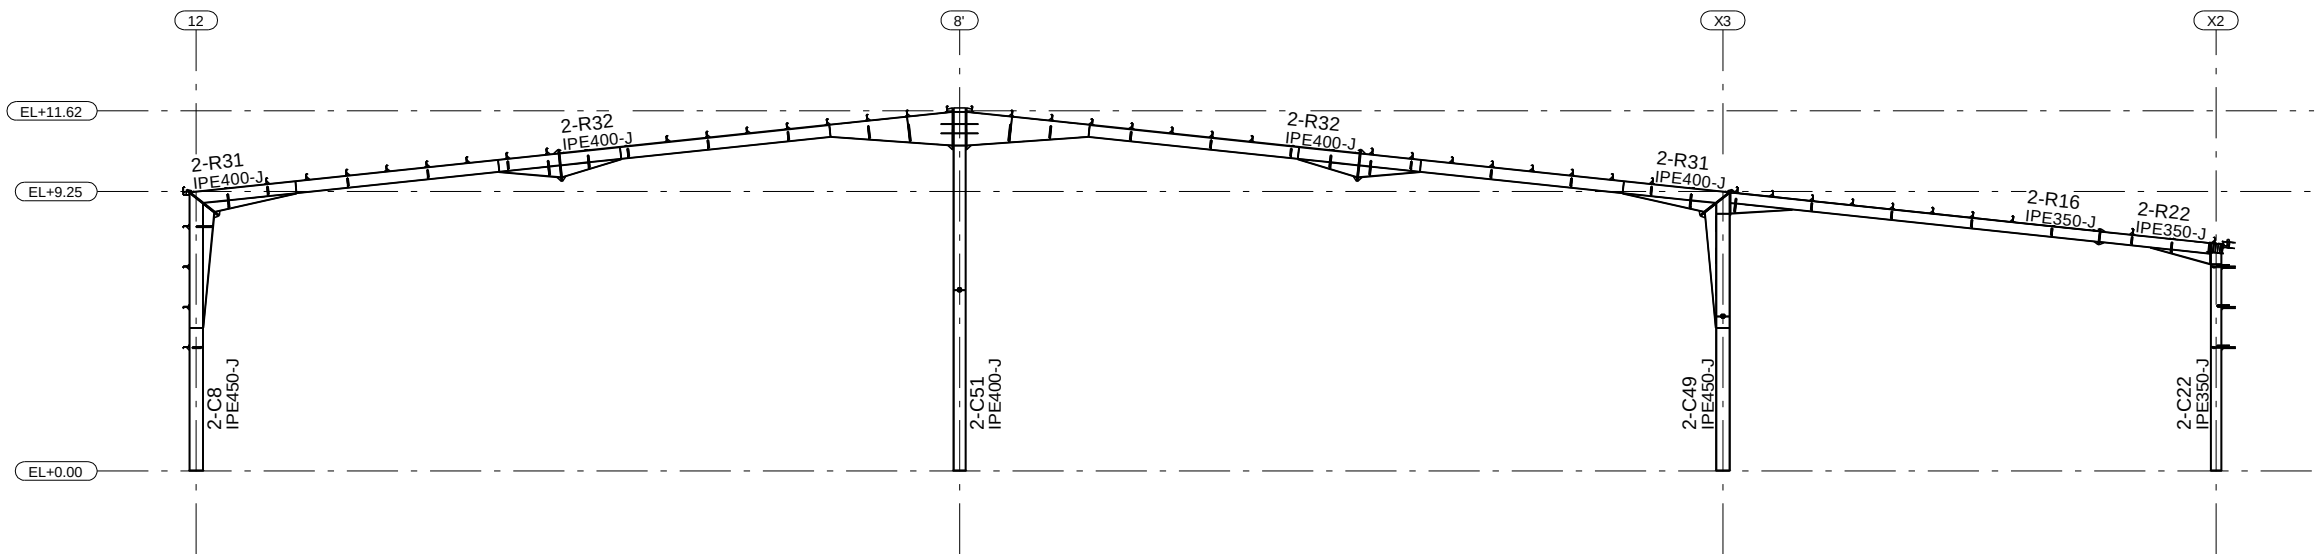

SECTION GRID L

FD	12-06-2026	ISSUED FOR FABRICATION	A.A	H.H	
REV	DATE	DESCRIPTION	DRN	CHK	DSN
.....					
PROJECT NAME:					
SCHOOL PROJECT					
CONTRACTOR:					
--					
DRAWING TITLE:					
STEEL STRUCTURE					
SECTION GRID (J + K + L)					
CHECKED BY	A.A	SCALE			
DATE	A.A	SHEET NO.	E19		