




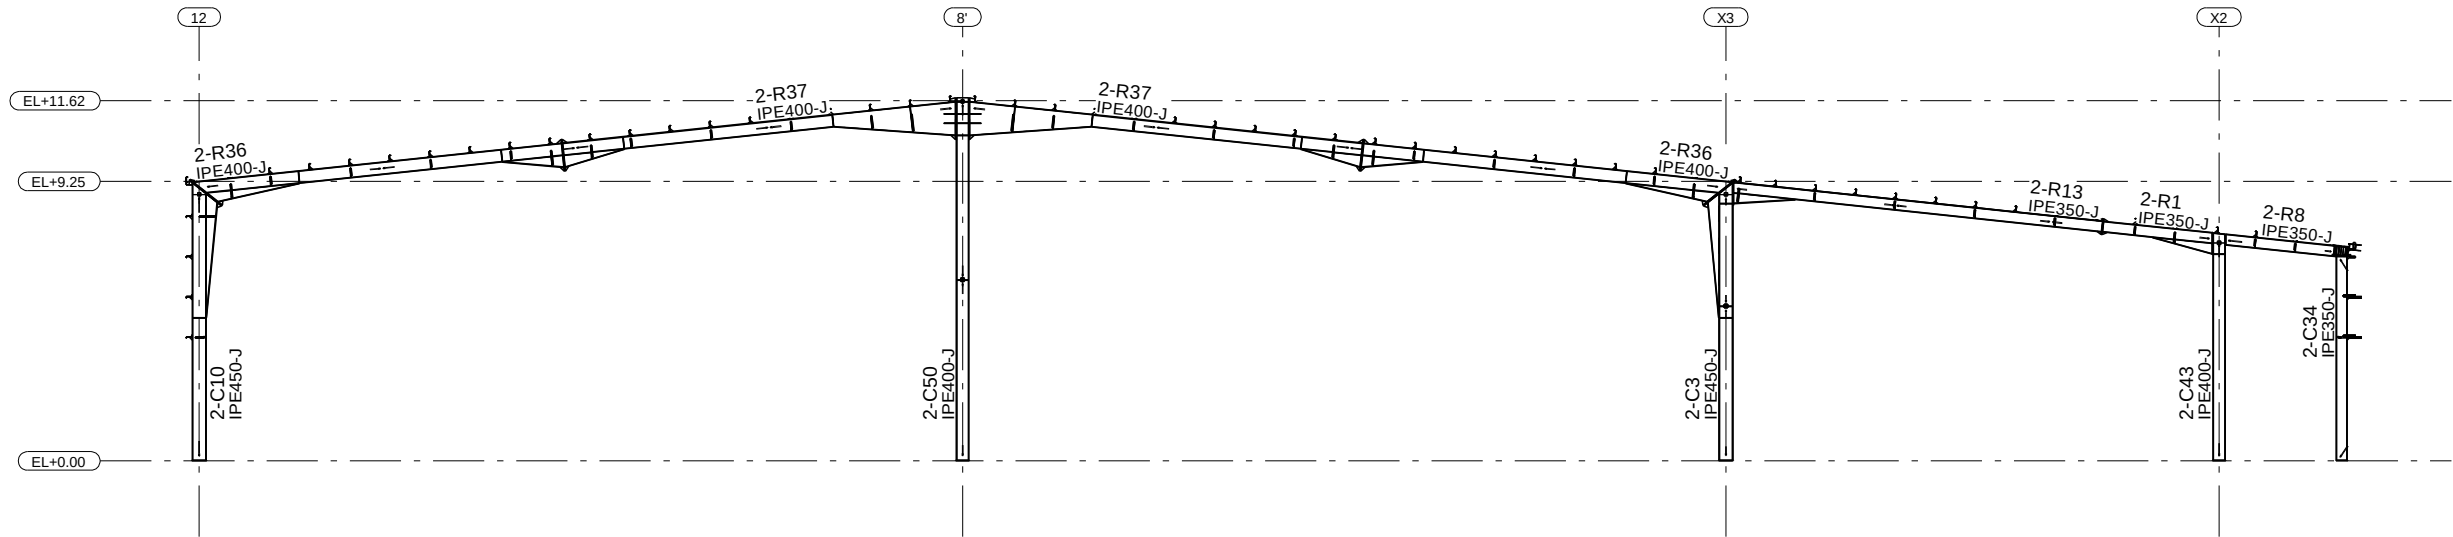

SECTION GRID M

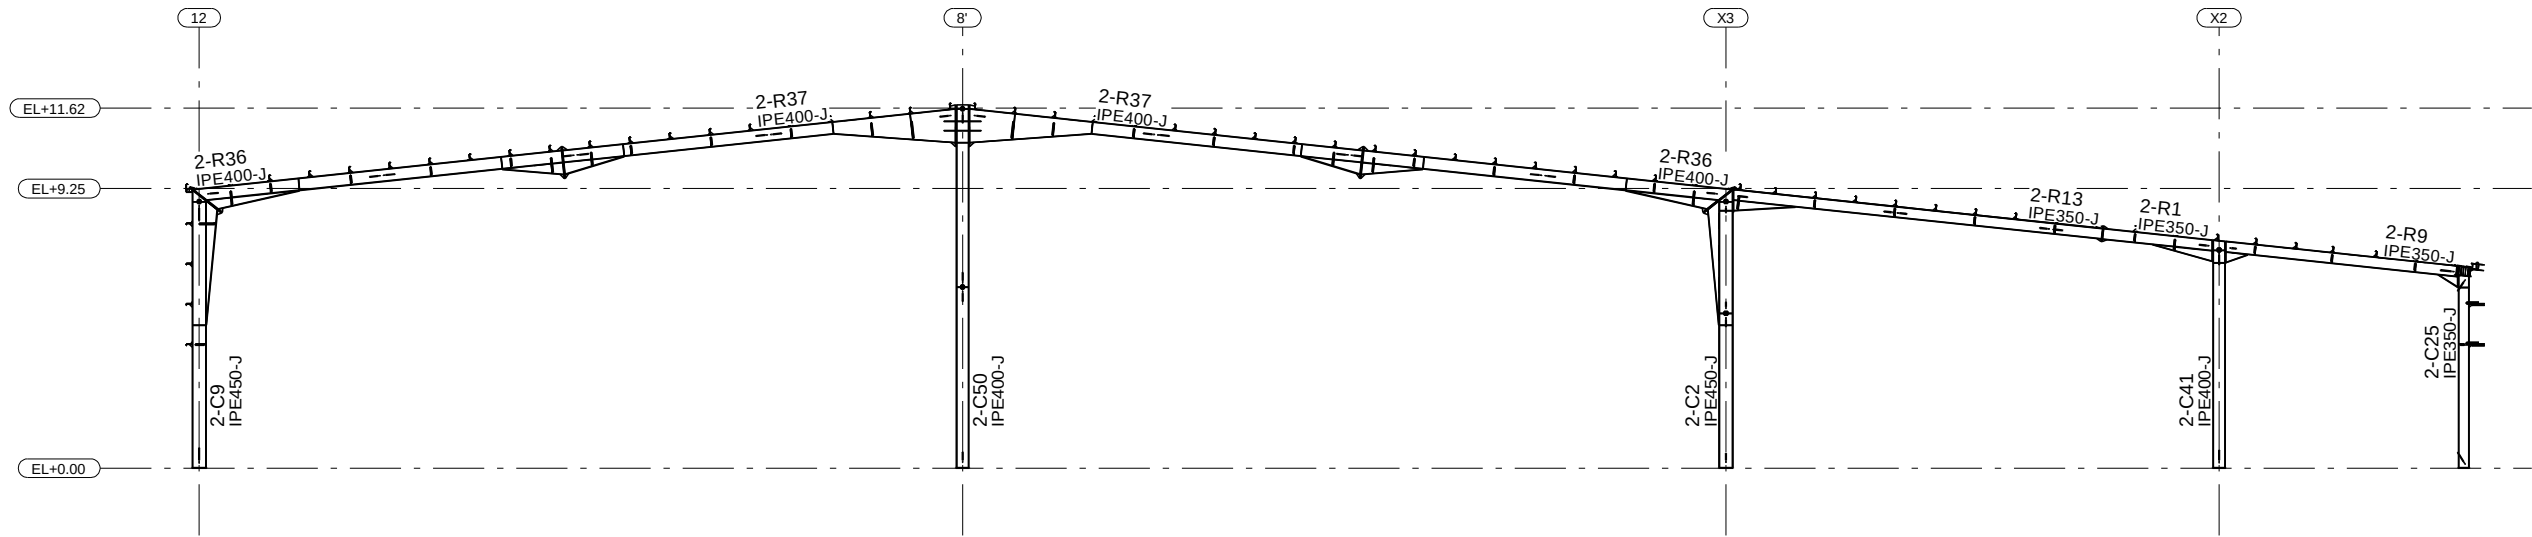

SECTION GRID N

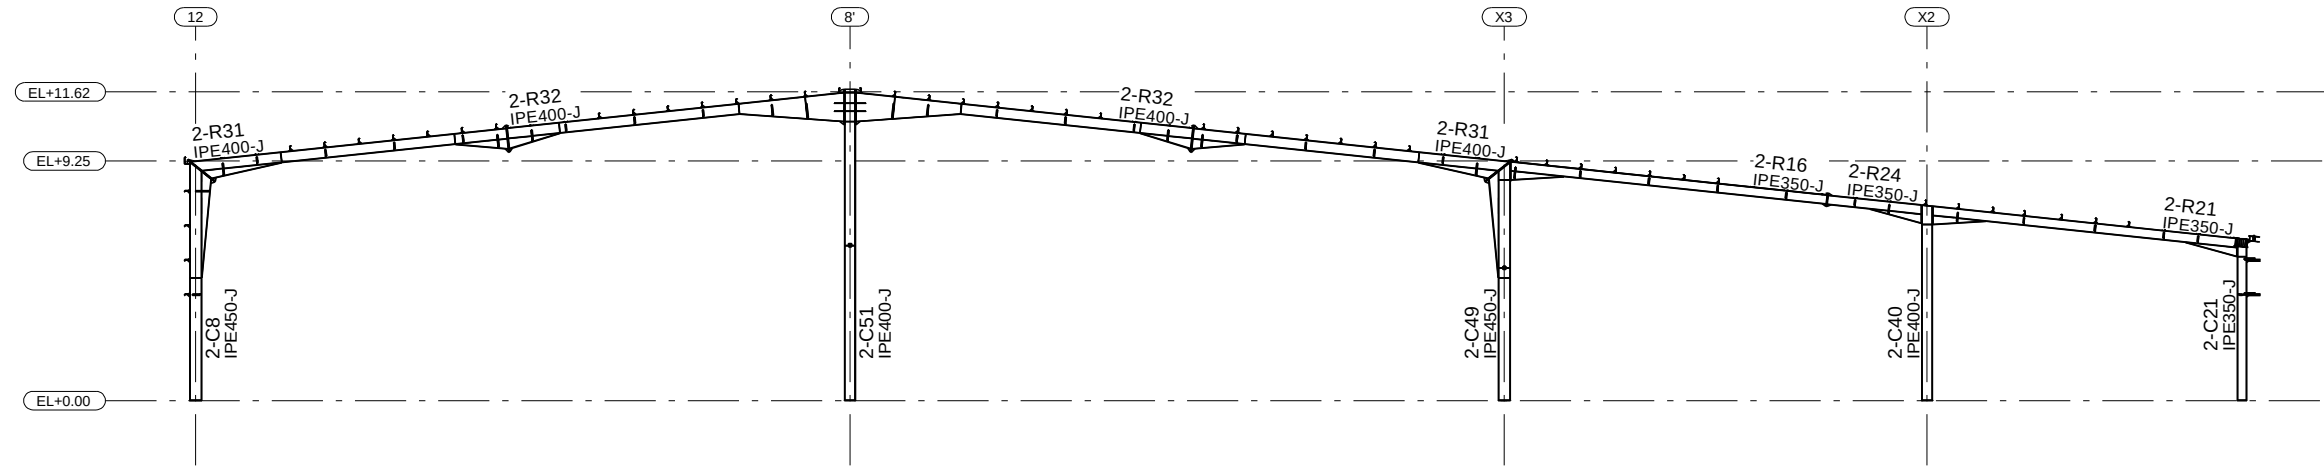

SECTION GRID P

FD	12-06-2026	ISSUED FOR FABRICATION			A.A	H.H		
REV.	DATE	DESCRIPTION				DRN	CHK	DSN

PROJECT NAME:								
SCHOOL PROJECT								
CONTRACTOR:								
--								
DRAWING TITLE:								
STEEL STRUCTURE								
SECTION GRID (M + N + P)								
CHECKED BY		A.A		SCALE				
DATE		A.A		SHEET NO.		E20		