




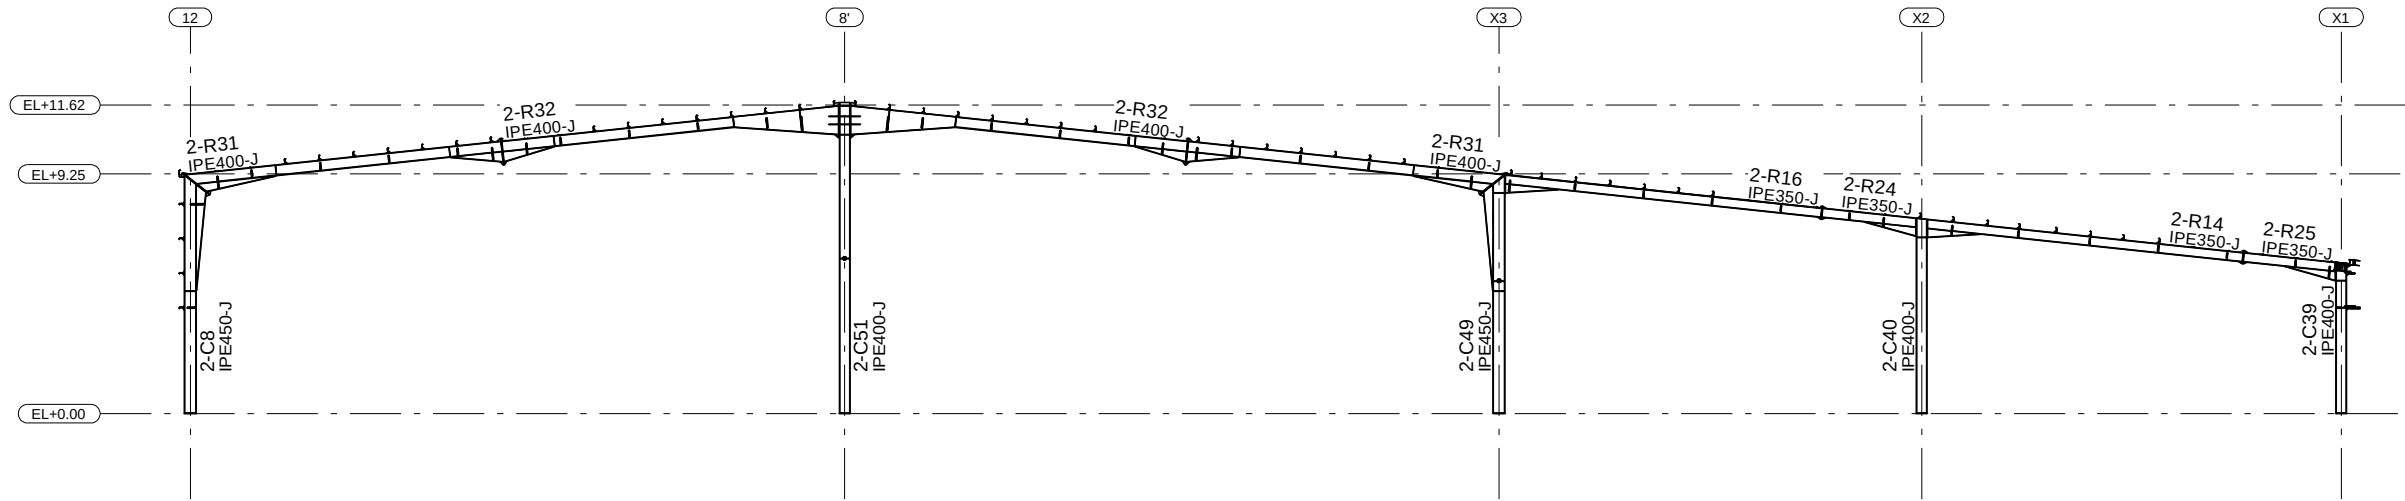

SECTION GRID Q

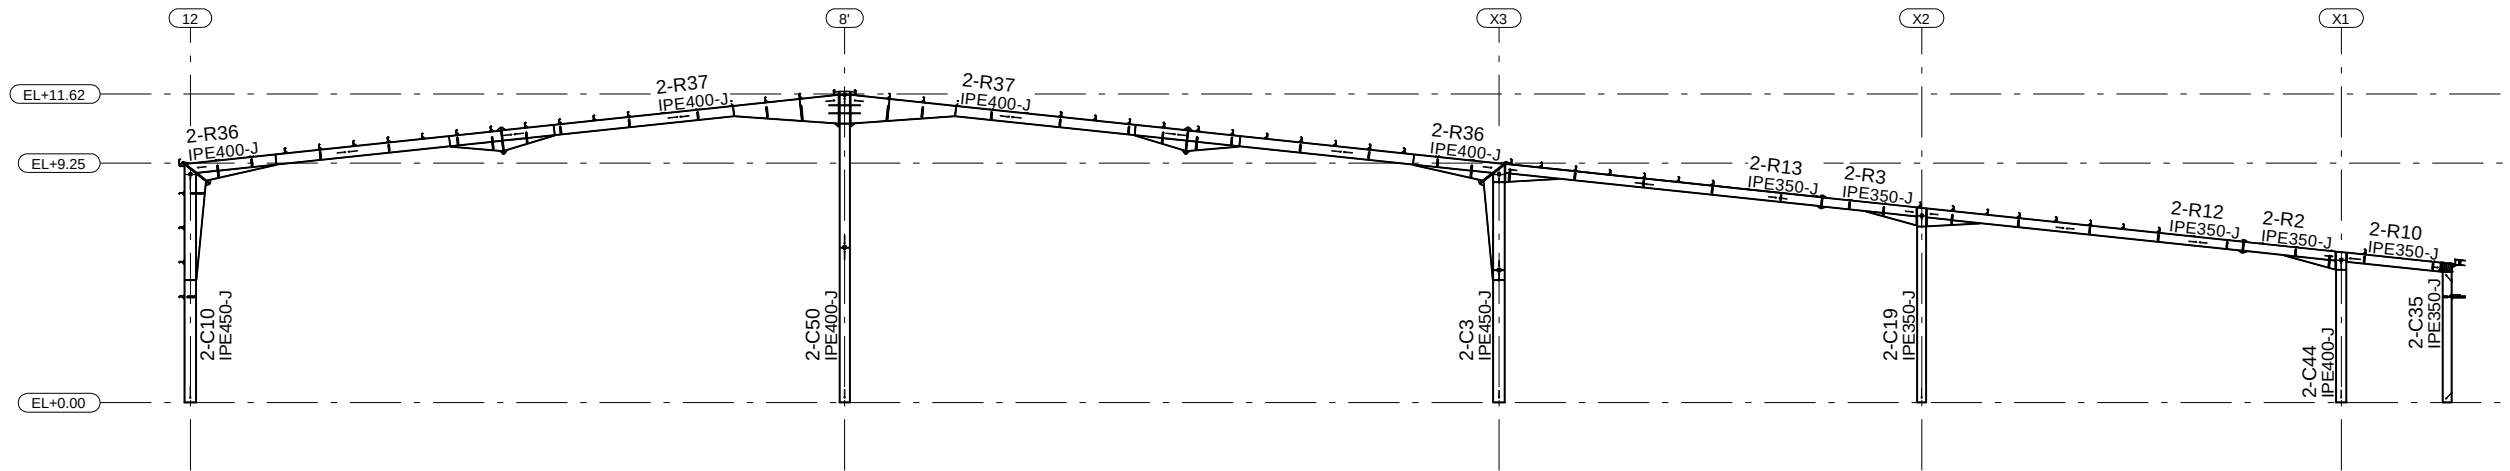

SECTION GRID R

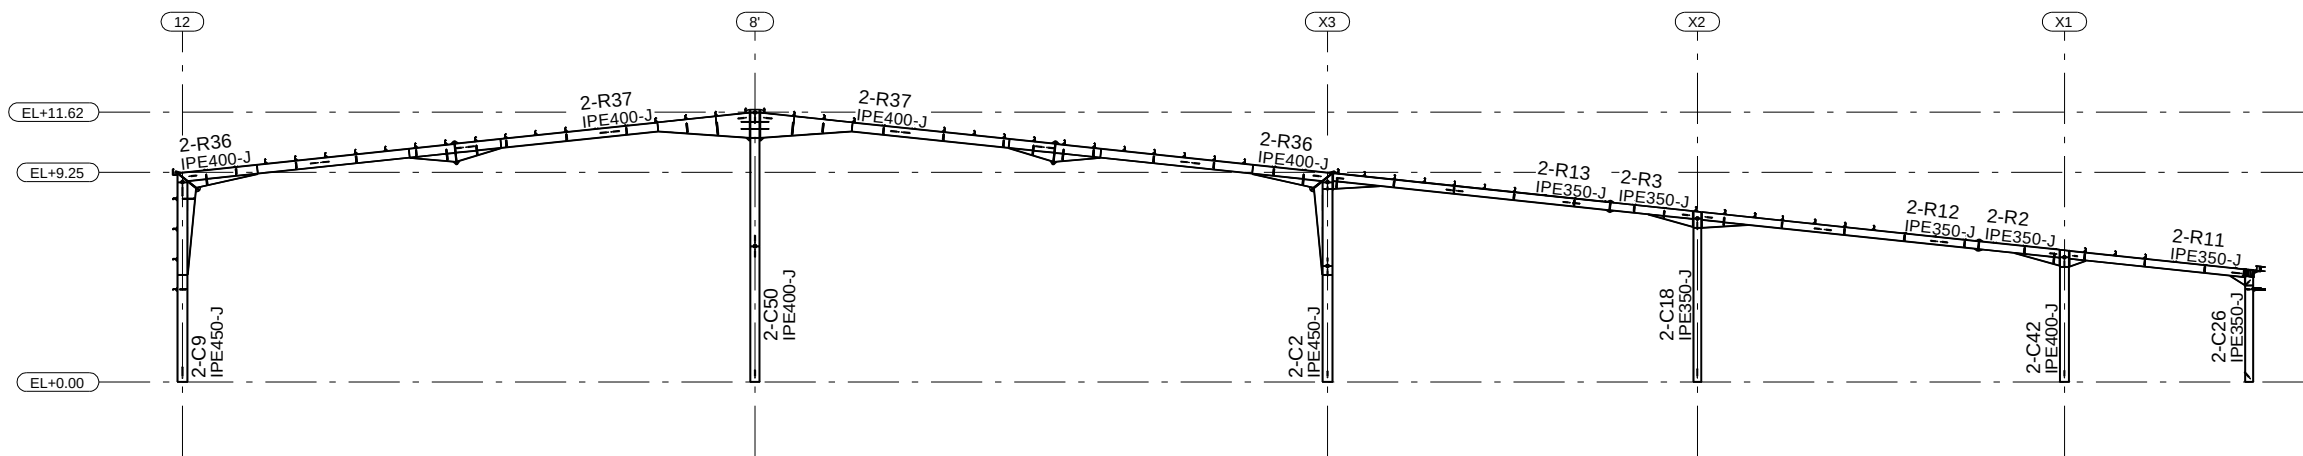

SECTION GRID R'

FD	12-06-2026	ISSUED FOR FABRICATION			A.A	H.H		
	REV.	DATE	DESCRIPTION			DRN	CHK	DSN

PROJECT NAME:								
SCHOOL PROJECT								
CONTRACTOR:								
--								
DRAWING TITLE:								
STEEL STRUCTURE								
SECTION GRID (Q +R + R')								
CHECKED BY		A.A		SCALE				
DATE		A.A		SHEET NO.		E21		