




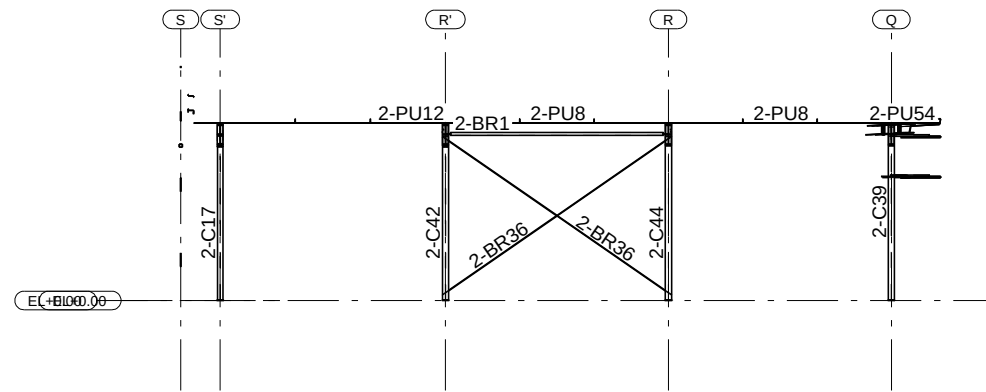

SECTION GRID X1

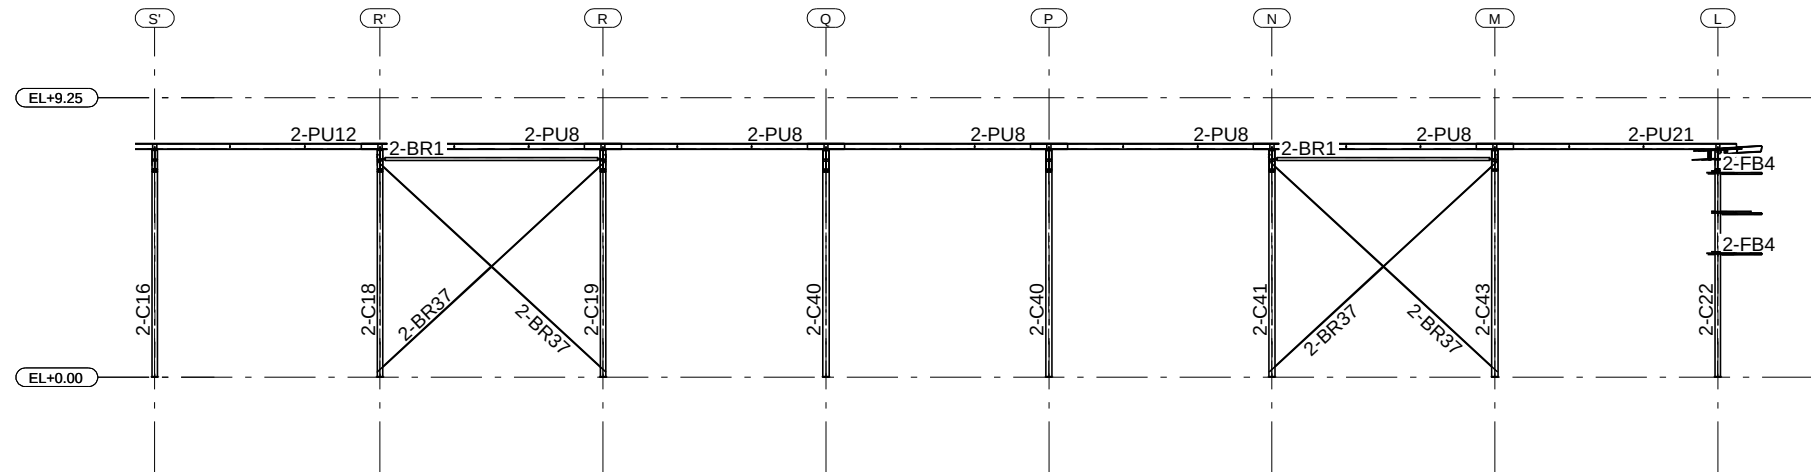

SECTION GRID X2

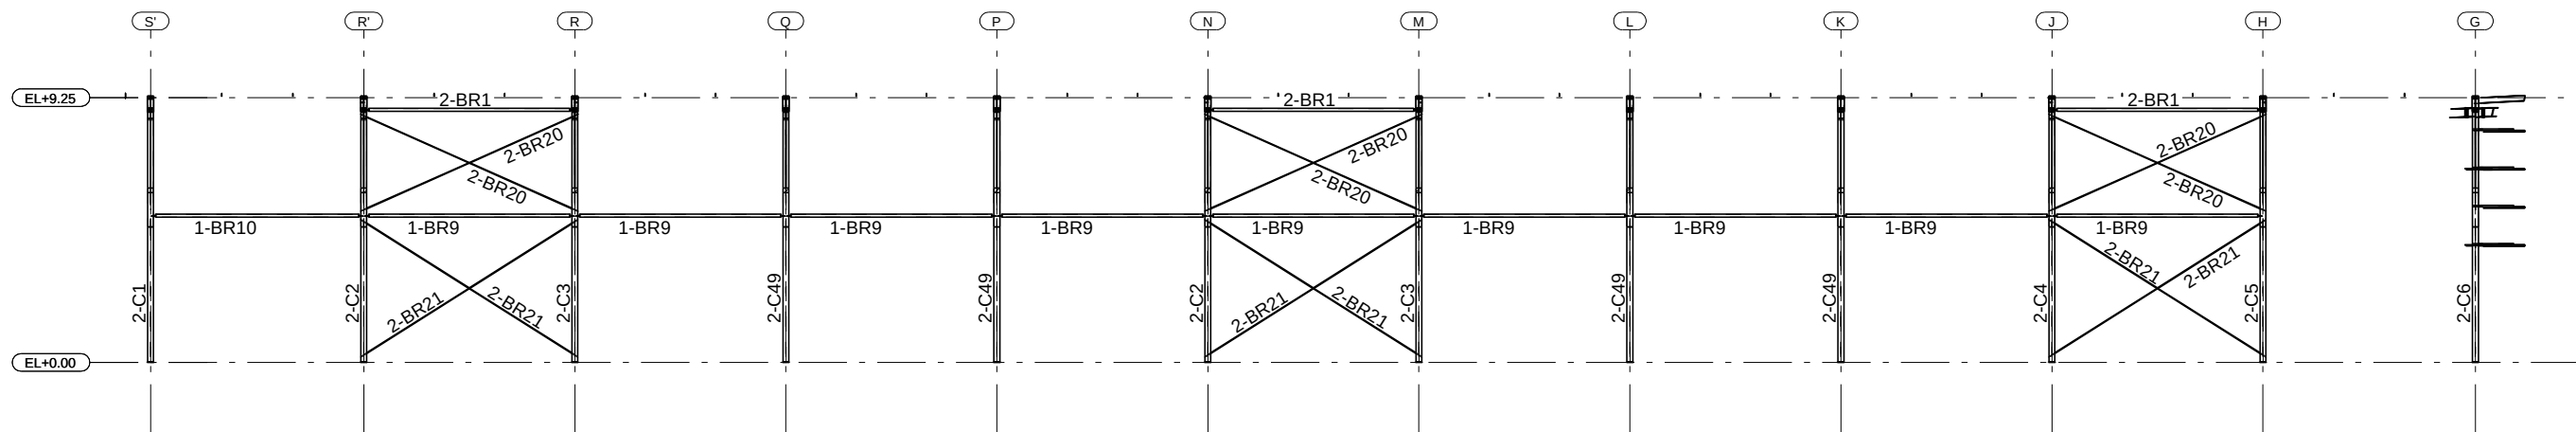

SECTION GRID X3

|                               |            |                        |     |     |     |
|-------------------------------|------------|------------------------|-----|-----|-----|
| FD                            | 12-06-2026 | ISSUED FOR FABRICATION | A.A | H.H |     |
| REV                           | DATE       | DESCRIPTION            | DRN | CHK | DSN |
| .....                         |            |                        |     |     |     |
| PROJECT NAME:                 |            |                        |     |     |     |
| SCHOOL PROJECT                |            |                        |     |     |     |
| CONTRACTOR:                   |            |                        |     |     |     |
| --                            |            |                        |     |     |     |
| DRAWING TITLE:                |            |                        |     |     |     |
| STEEL STRUCTURE               |            |                        |     |     |     |
| SECTION GRID ( X1 + X2 + X3 ) |            |                        |     |     |     |
| CHECKED BY                    | A.A        | SCALE                  |     |     |     |
| DATE                          | A.A        | SHEET NO.              | E24 |     |     |