



SECTION GRID S

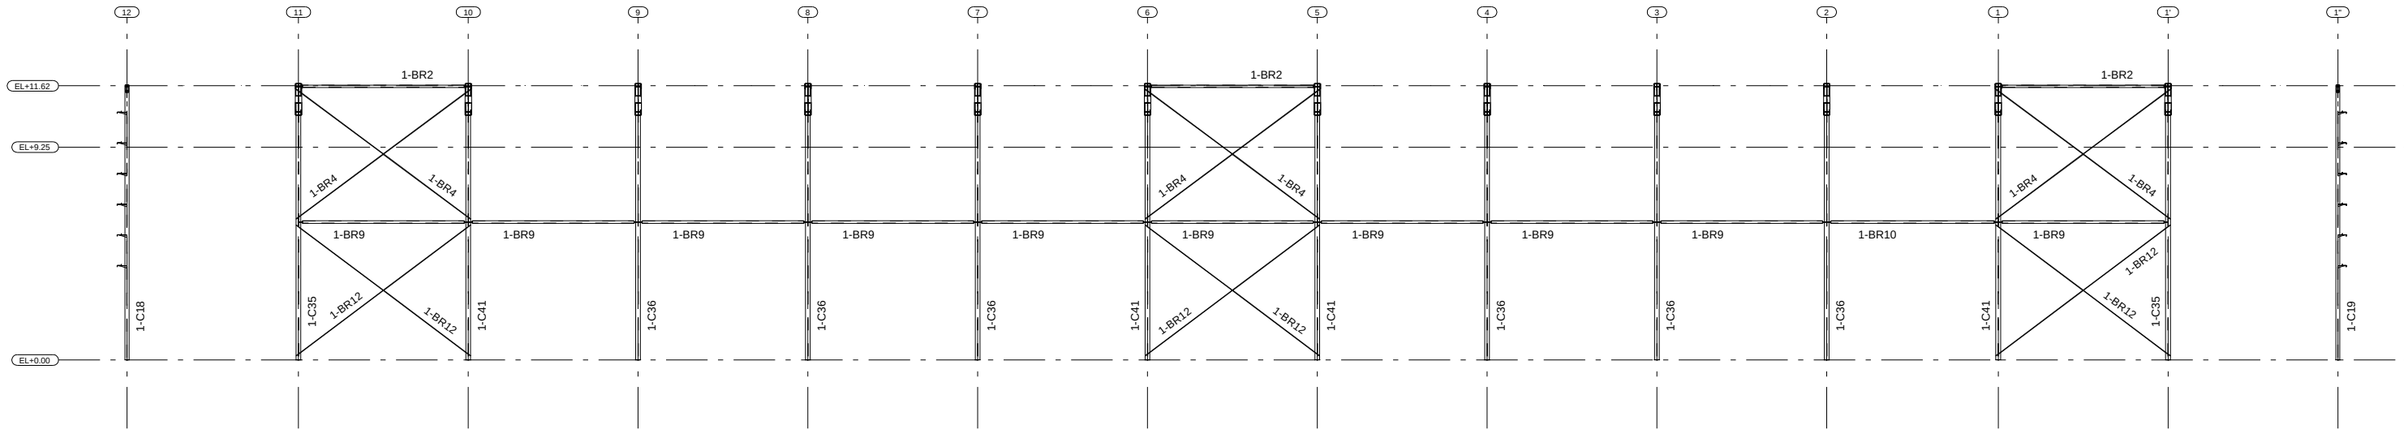

SECTION GRID T

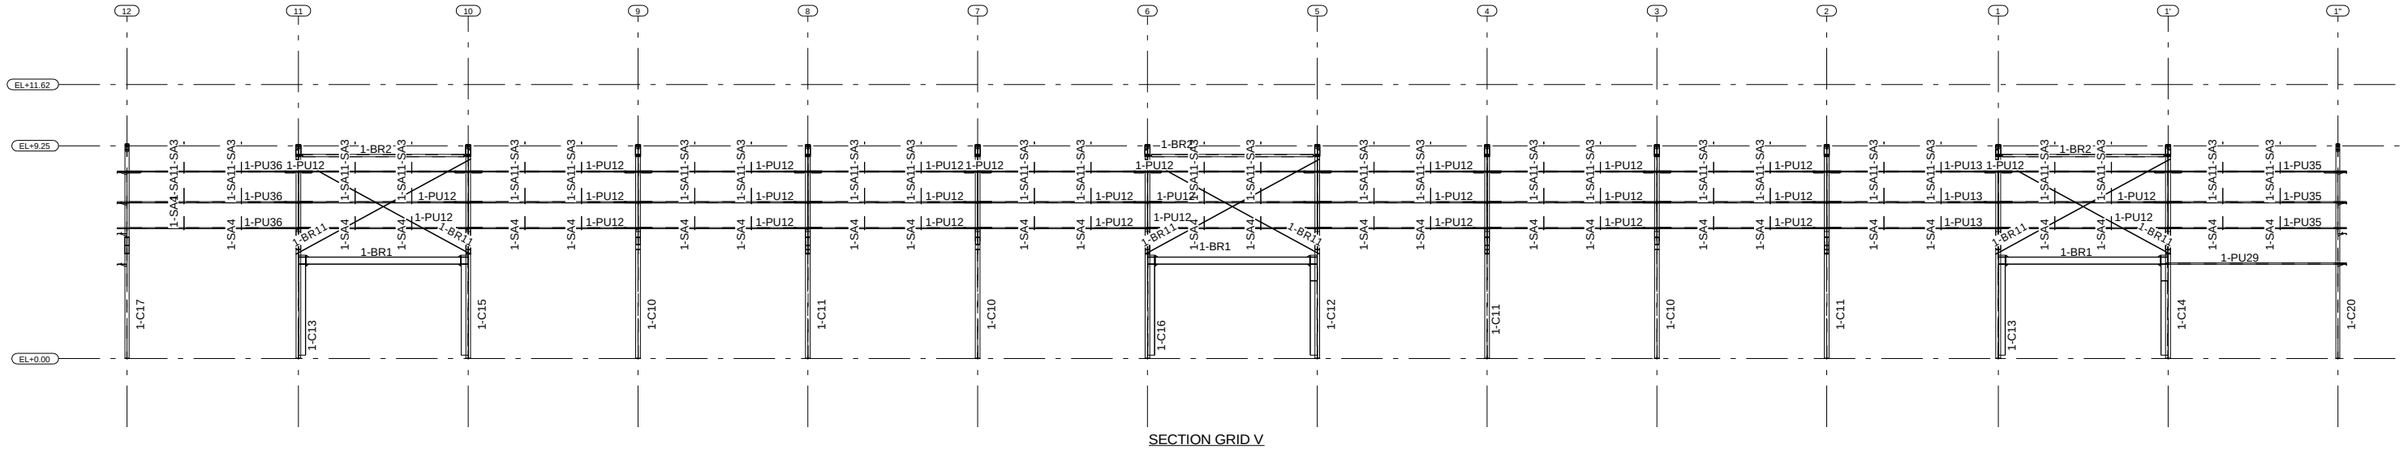

SECTION GRID V

REV	DATE	DESCRIPTION	DRN	CHK	DSN
1	12-06-2026	ISSUED FOR FABRICATION	A.A	H.H	

PROJECT NAME:
SCHOOL PROJECT

CONTRACTOR:
- -

DRAWING TITLE:
STEEL STRUCTURE
SECTION GRID (V + T + S)

CHECKED BY	A.A	SCALE	
DATE	A.A	SHEET NO.	E15

PDF created with pdfFactory Pro trial version pdffactory.com